


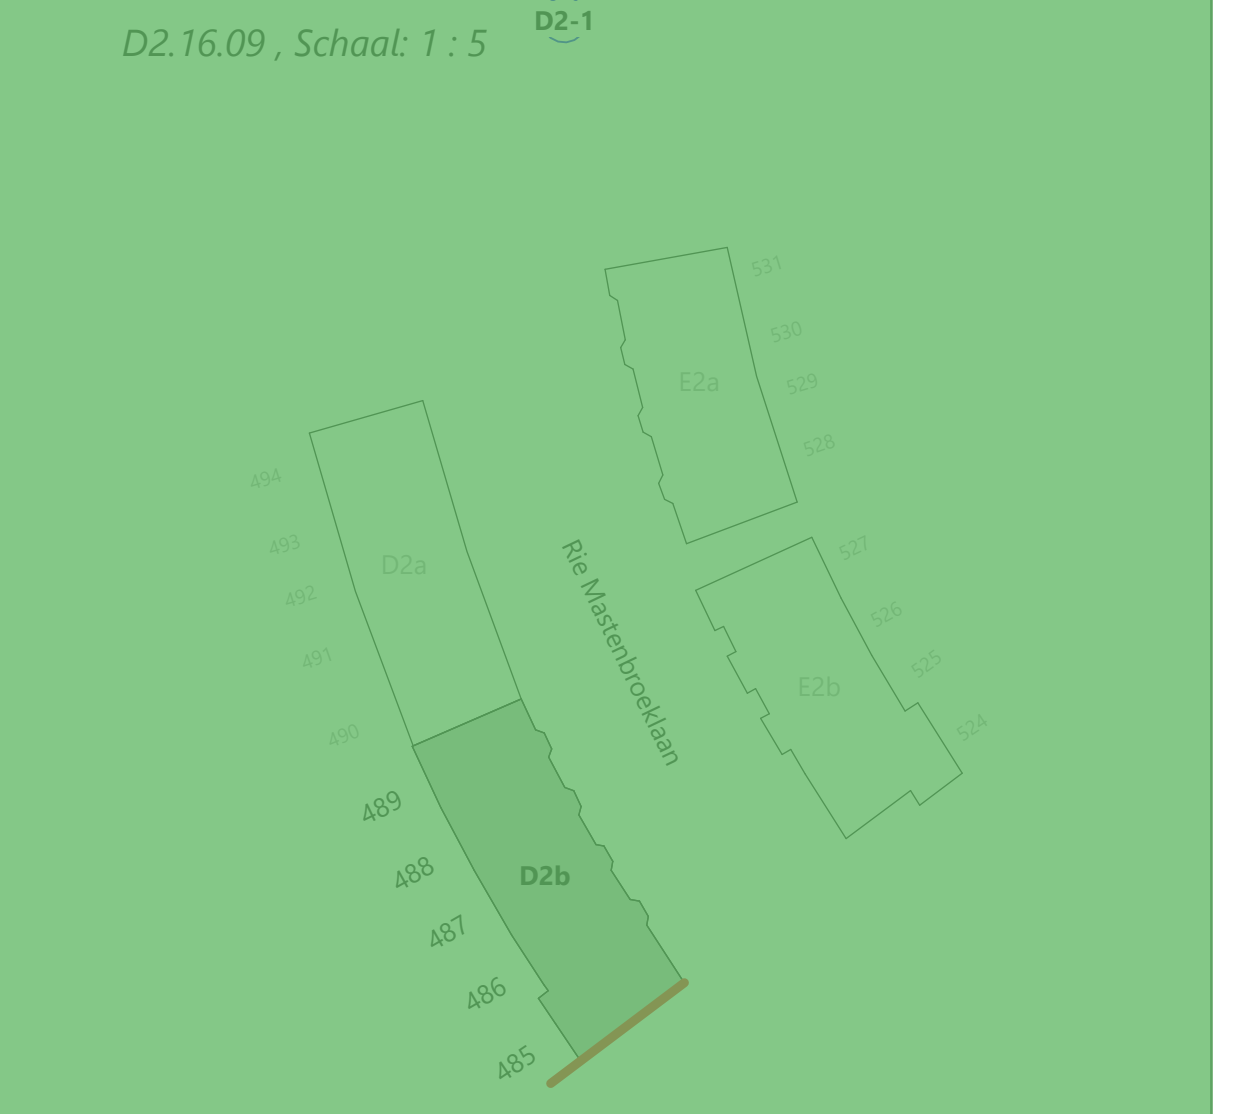
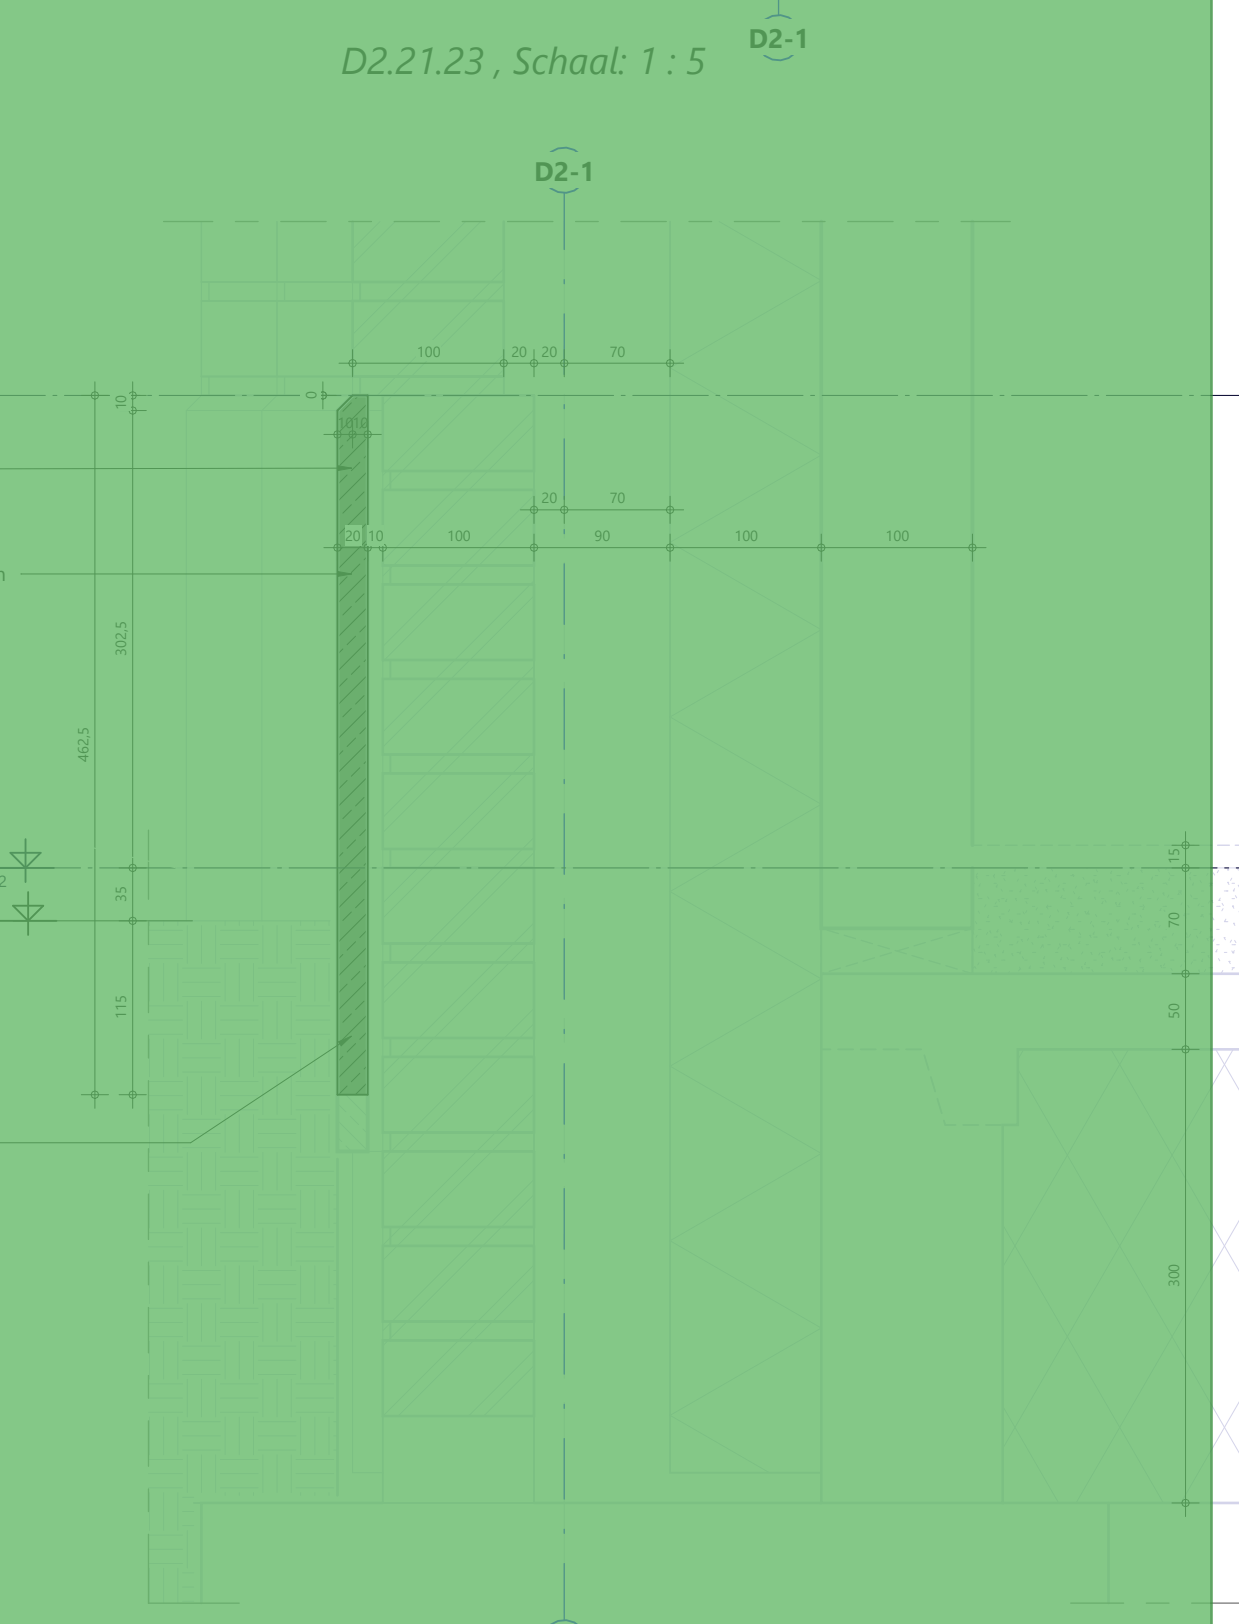
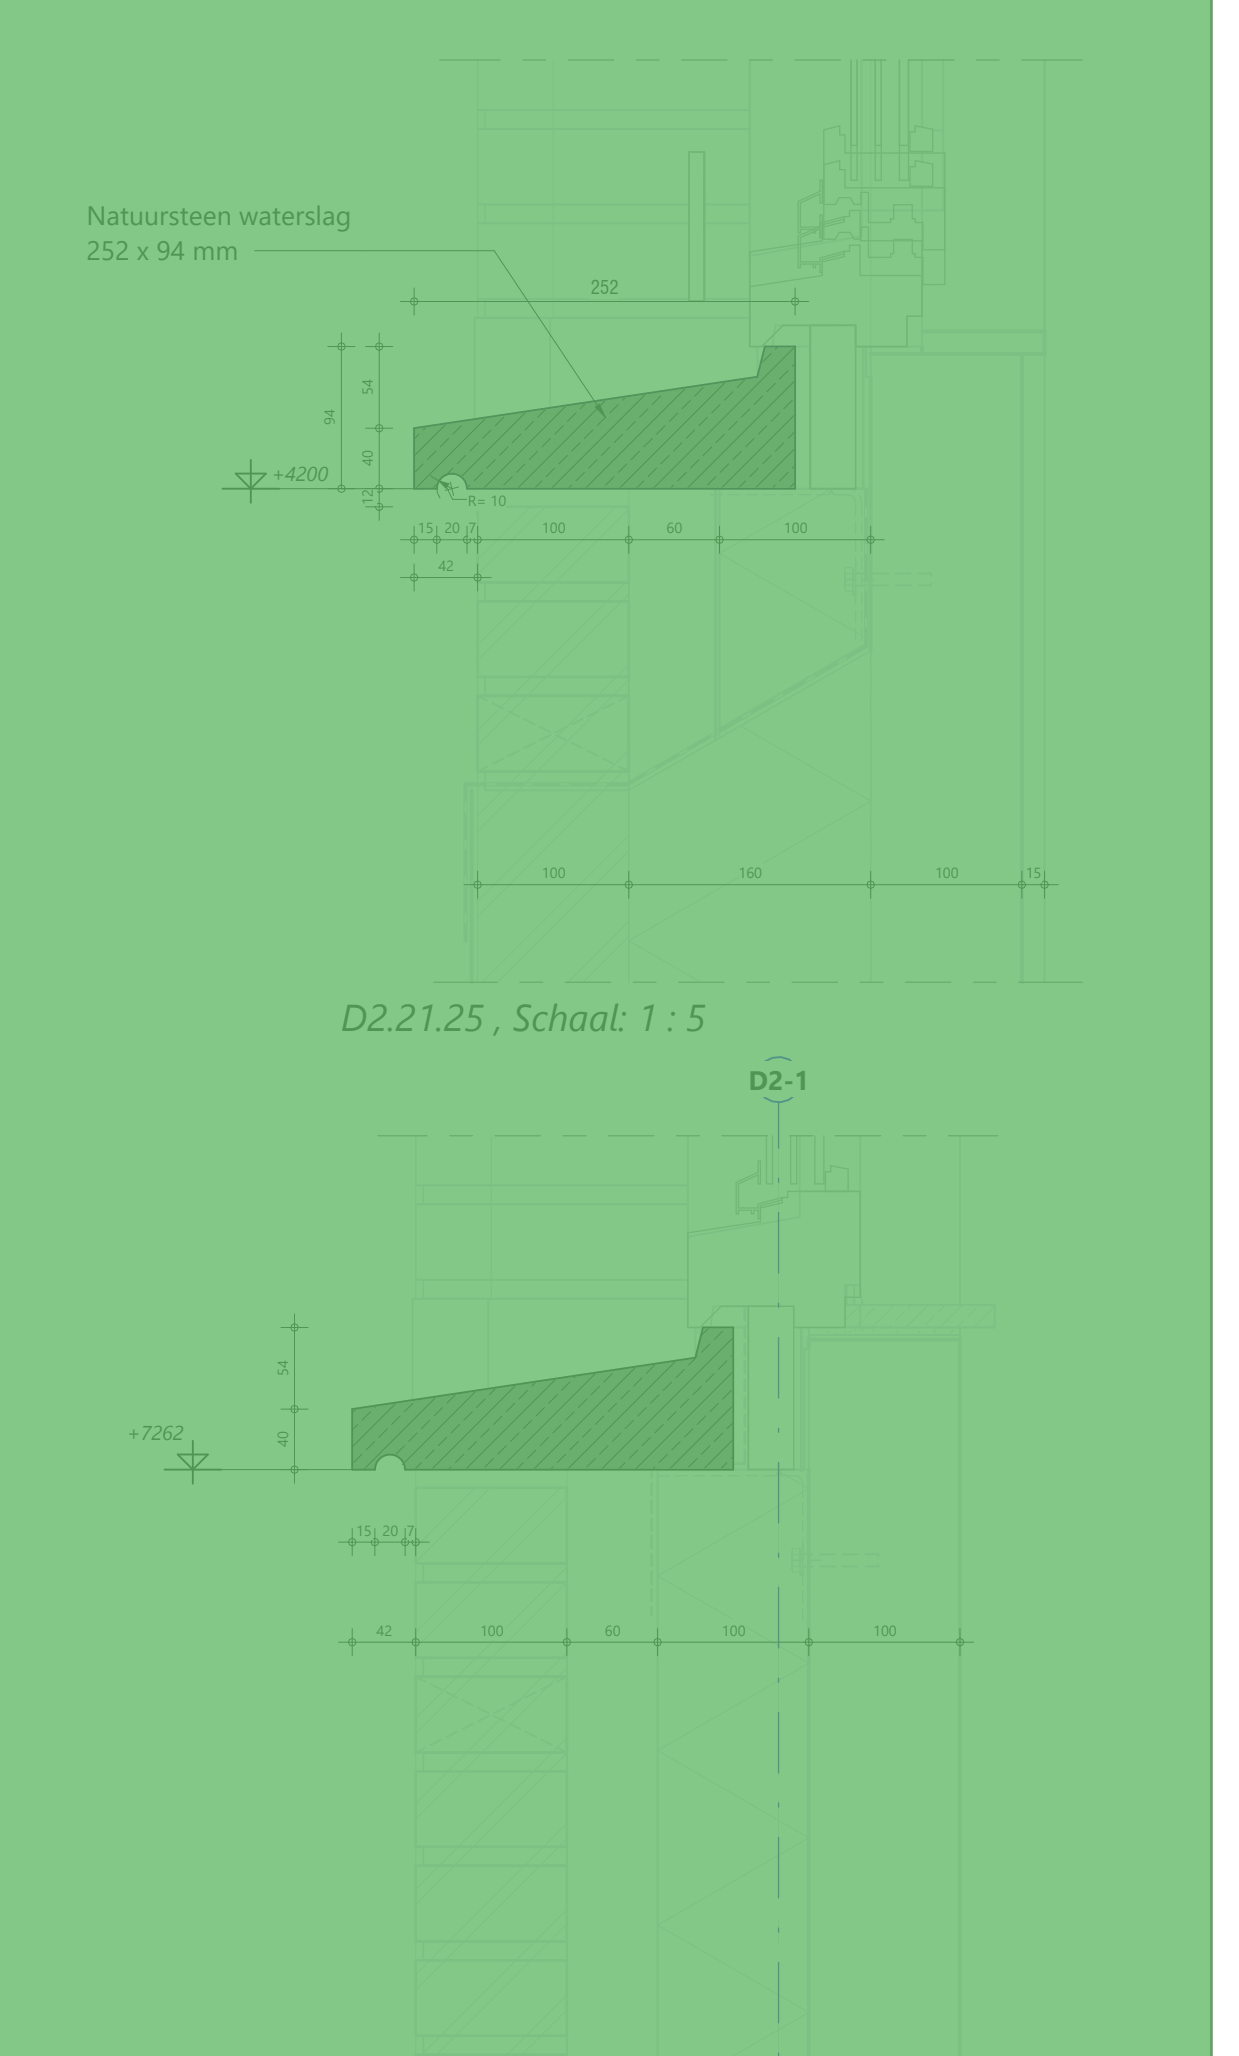




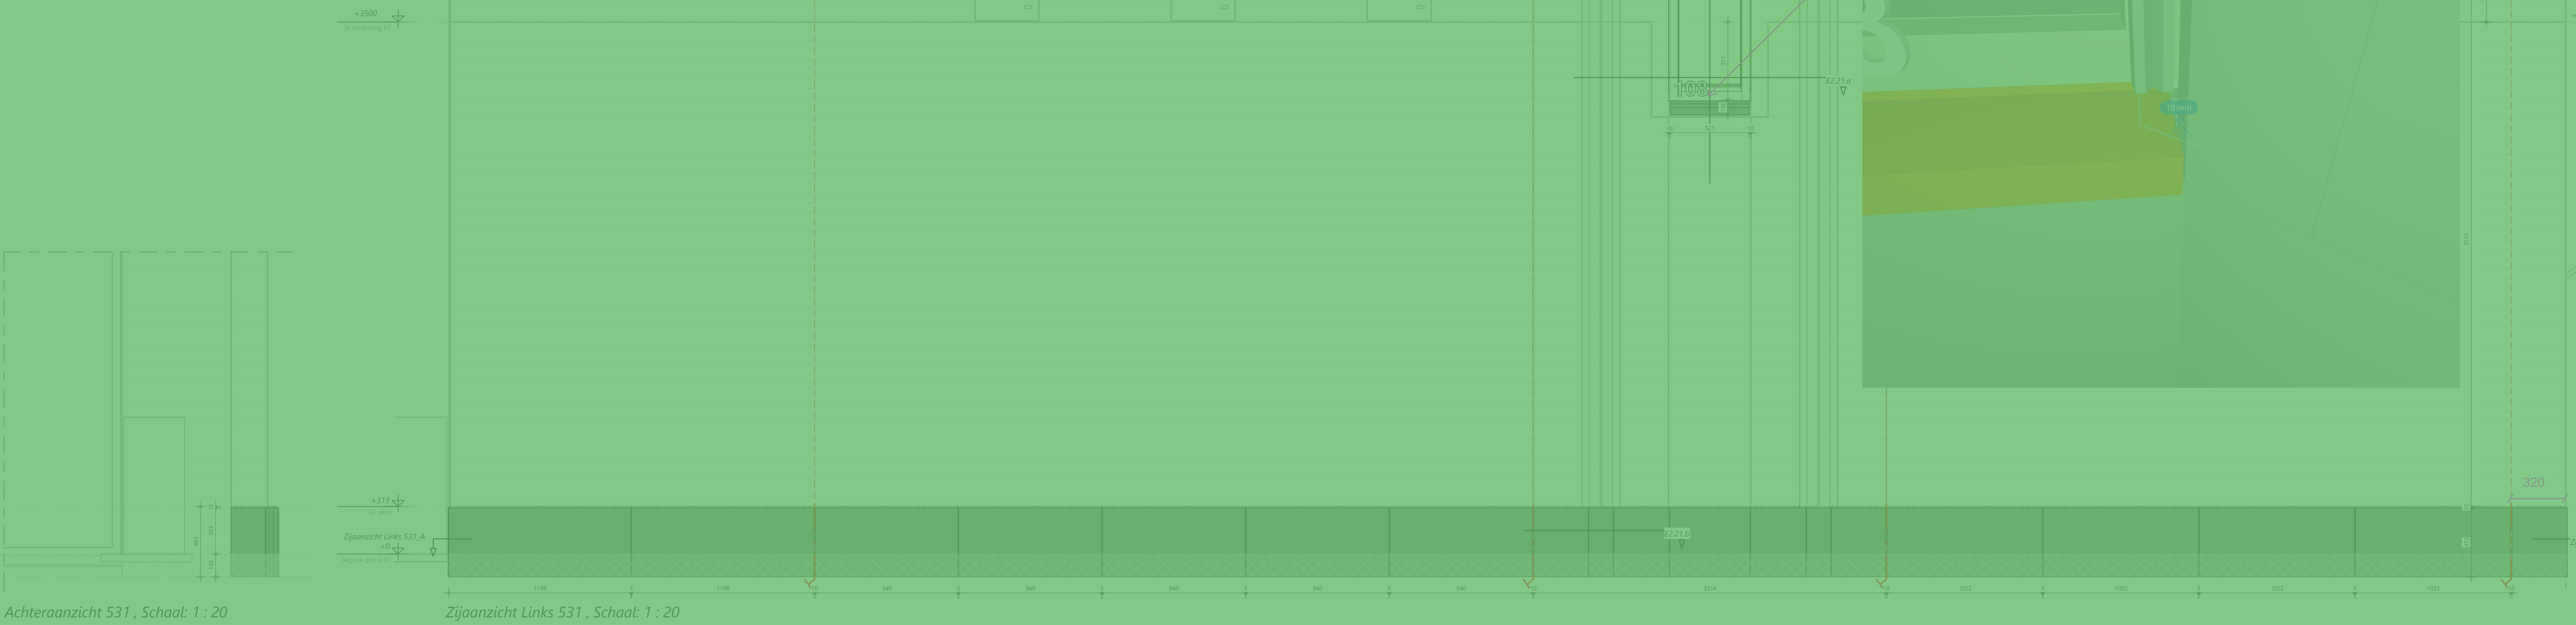


NATUURSTEN	
Gevolgtijl	Belgisch hardsteen bewerking: gris geschild / Mule Gris by hand gheschild dikte: 20 mm voggin: 5 mm standaard 10 mm t.p.v. open stootvoeg/stafatie
Overlegfne	Alle paravien met dit symbool hebben 50mm overlegfne Klinken door deuren aan te brengen. Het plaatsen van materiaal dient draadwerk minimaal 50 cm vrijgehouden te worden en voorzichtig aangeleid . Bewerkingen in natuurstein: randafstand minimaal 70 mm aangehouden. Natuurstein is spanningsoverveel; bewerkingsmet niet zorg en zonder spanning aandragen.

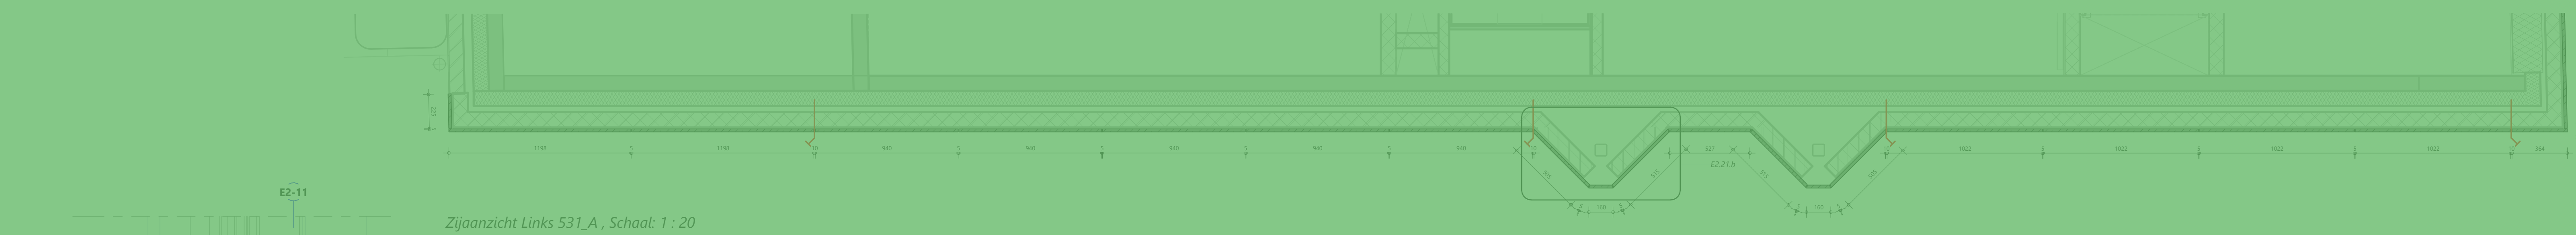


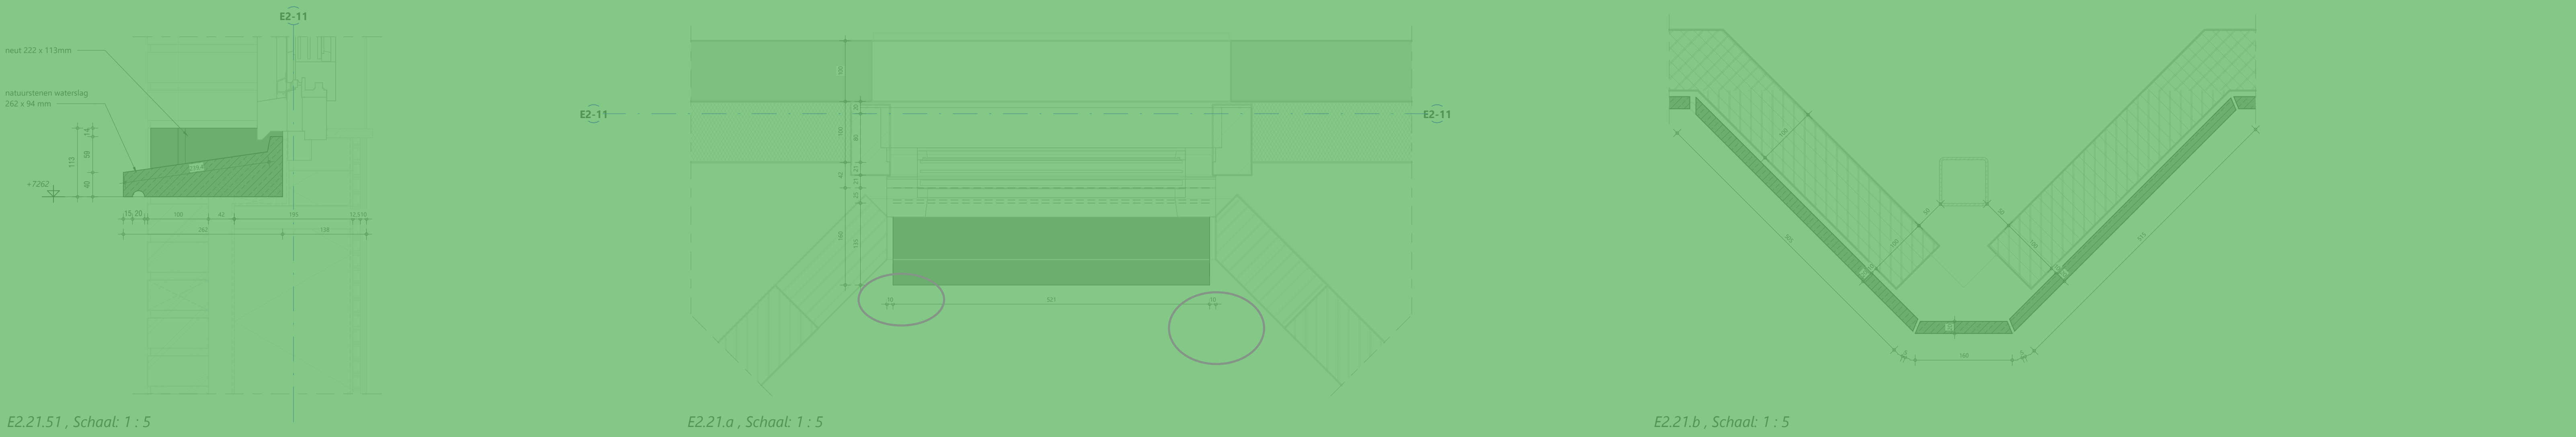


Achteraanzicht S31, Schaal: 1 : 20

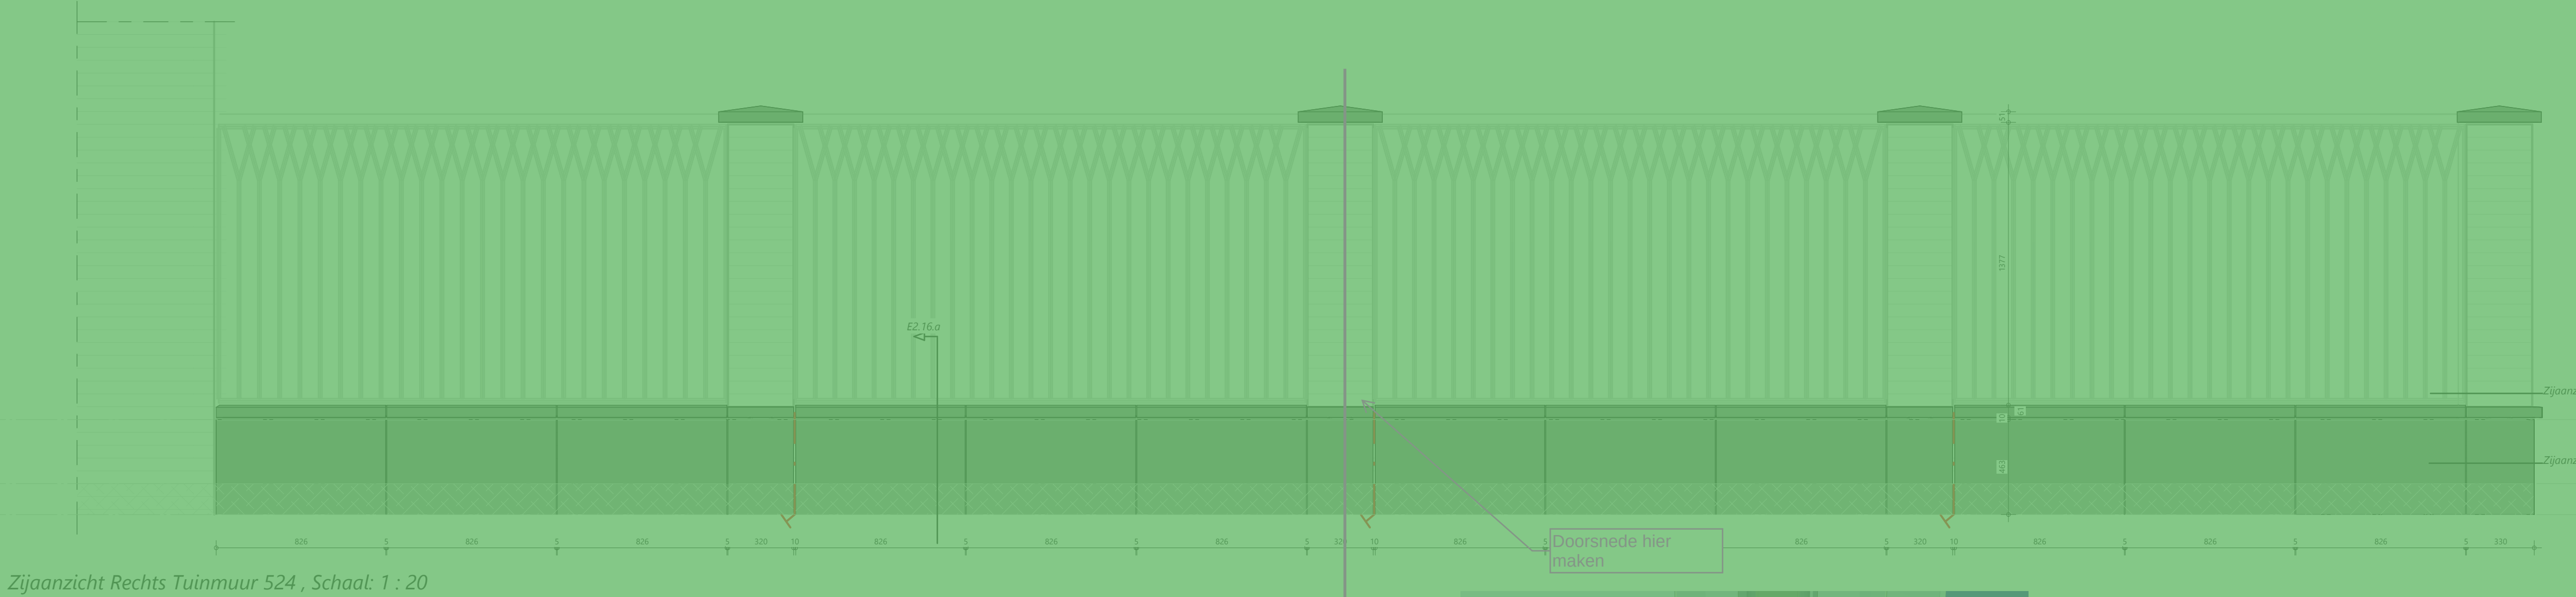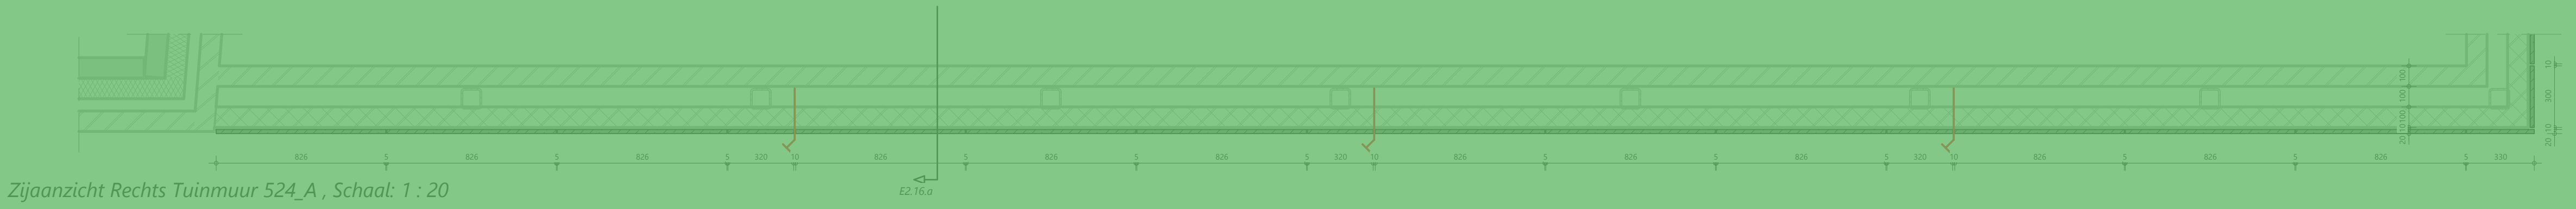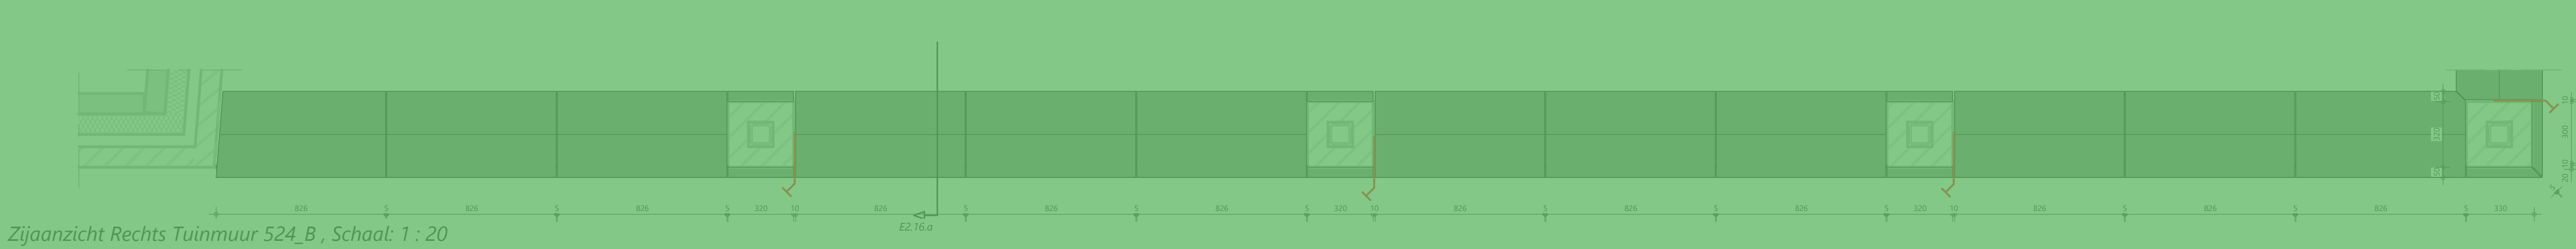




Zijaanzicht Rechts Tuinmuur 524, Schaal: 1 : 20

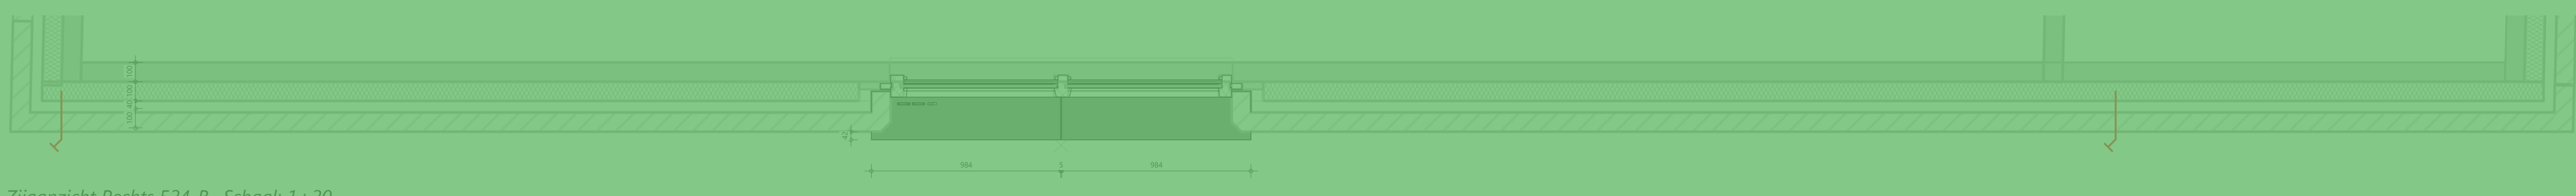


Zijaanzicht Rechts 524, Schaal: 1 : 20

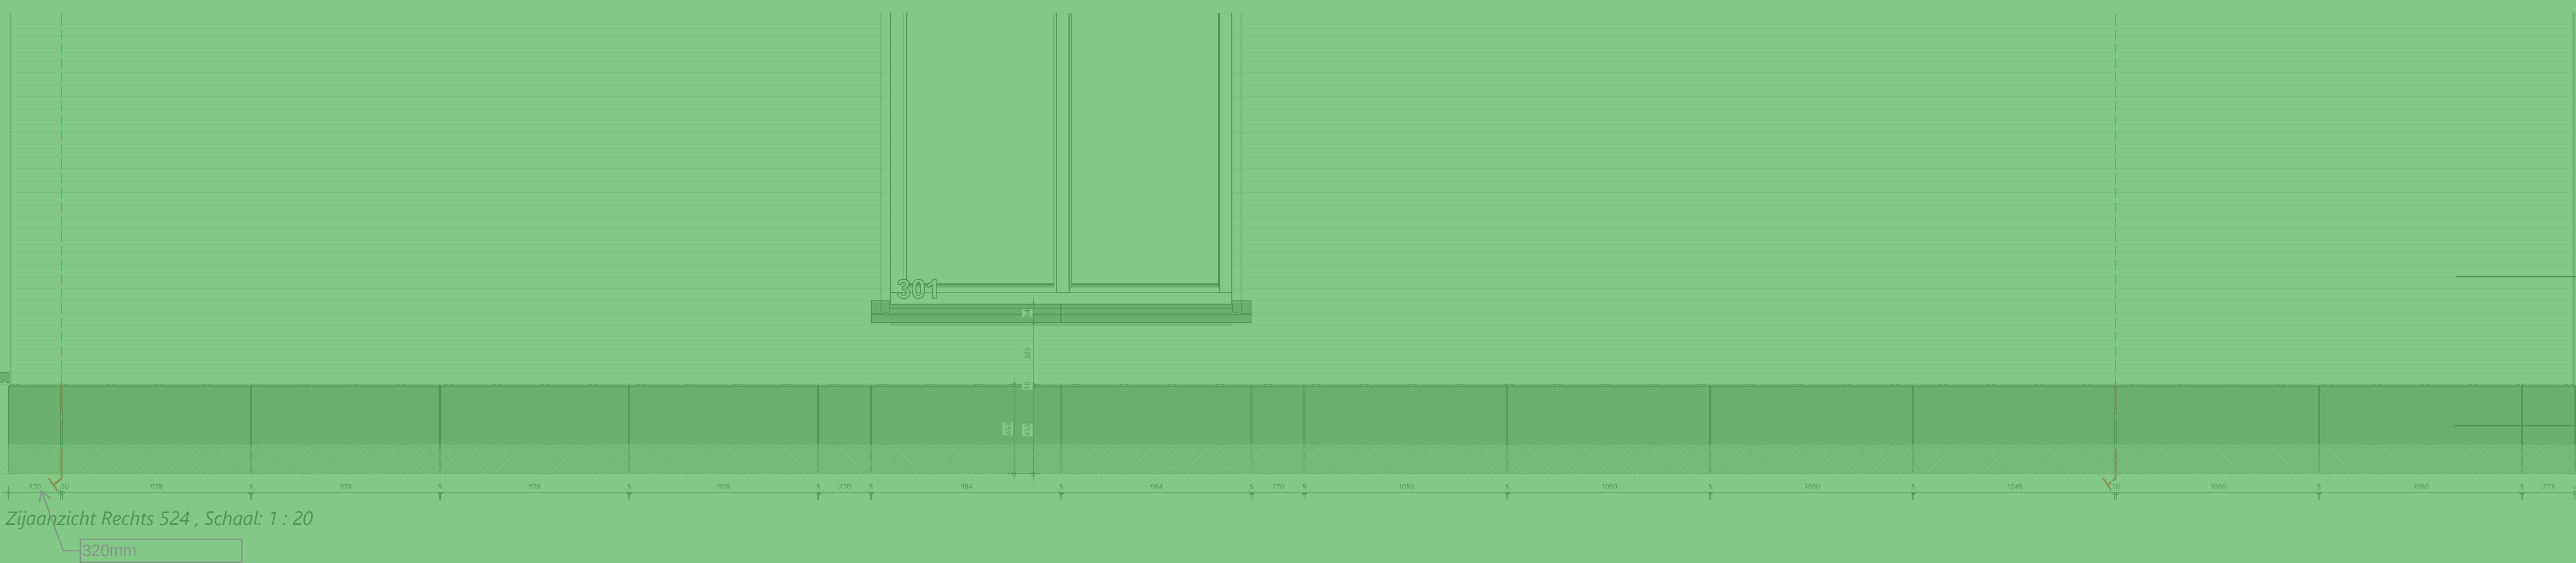

Zijaanzicht Rechts 524, Schaal: 1 : 20

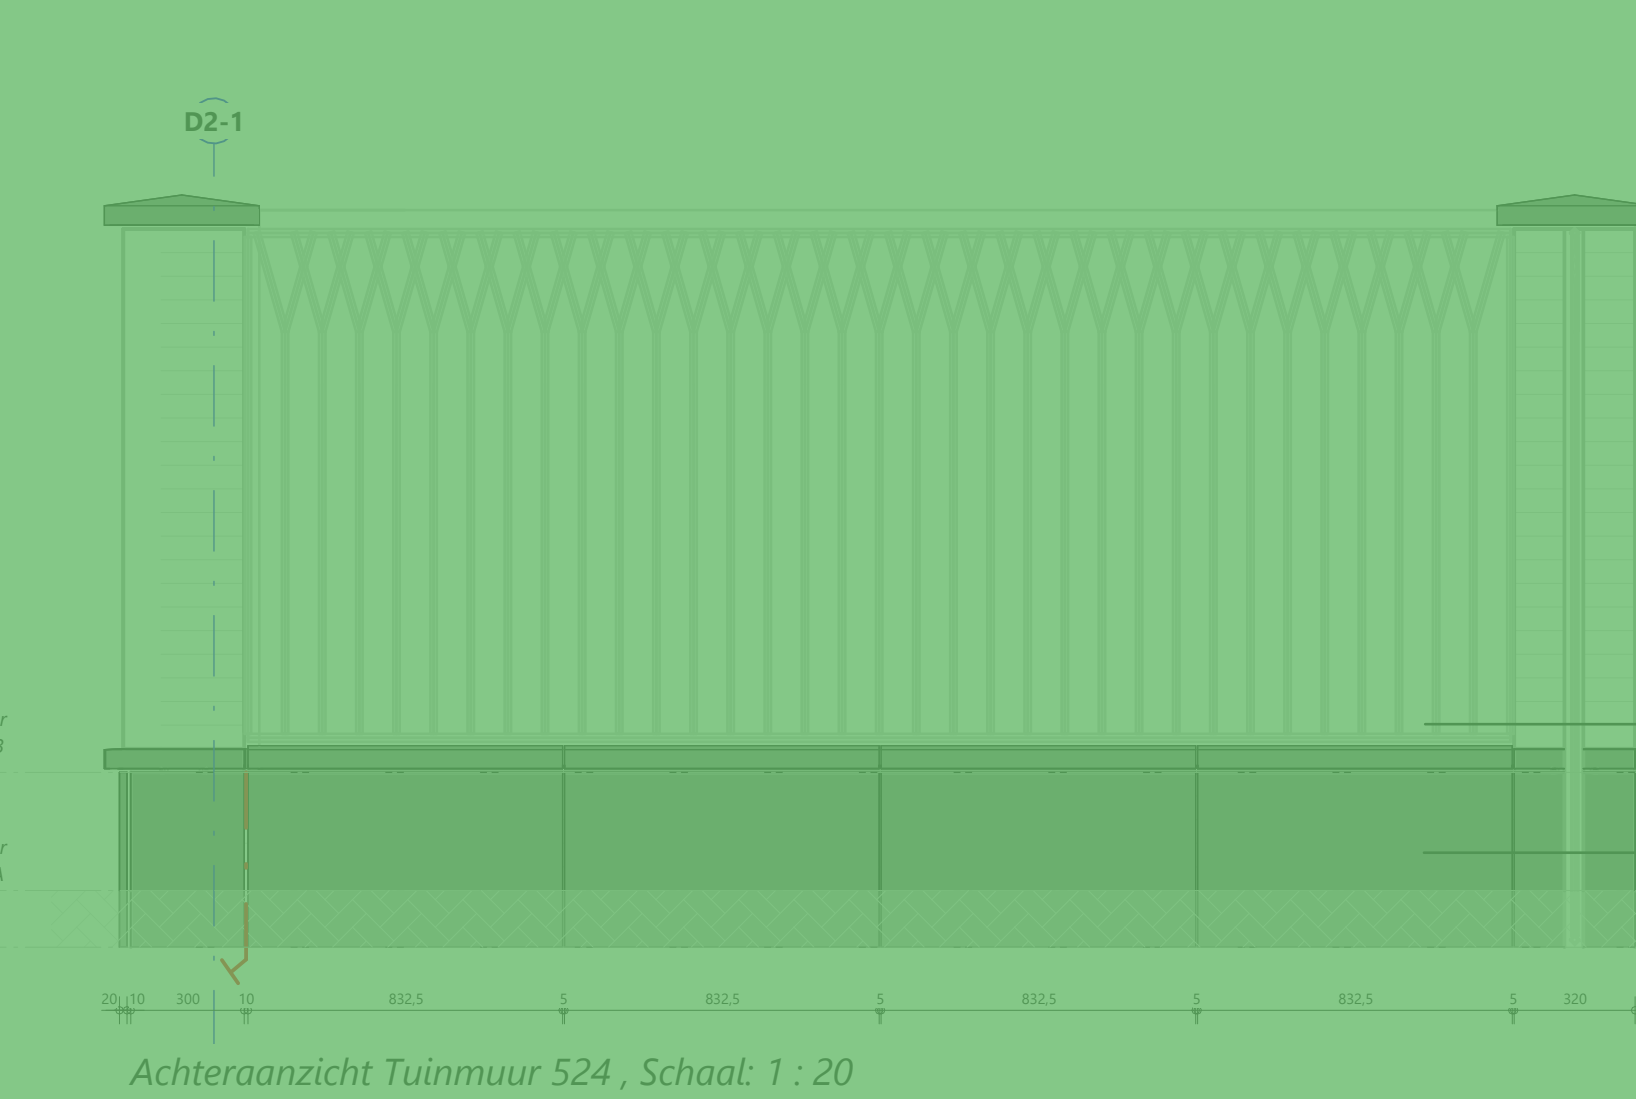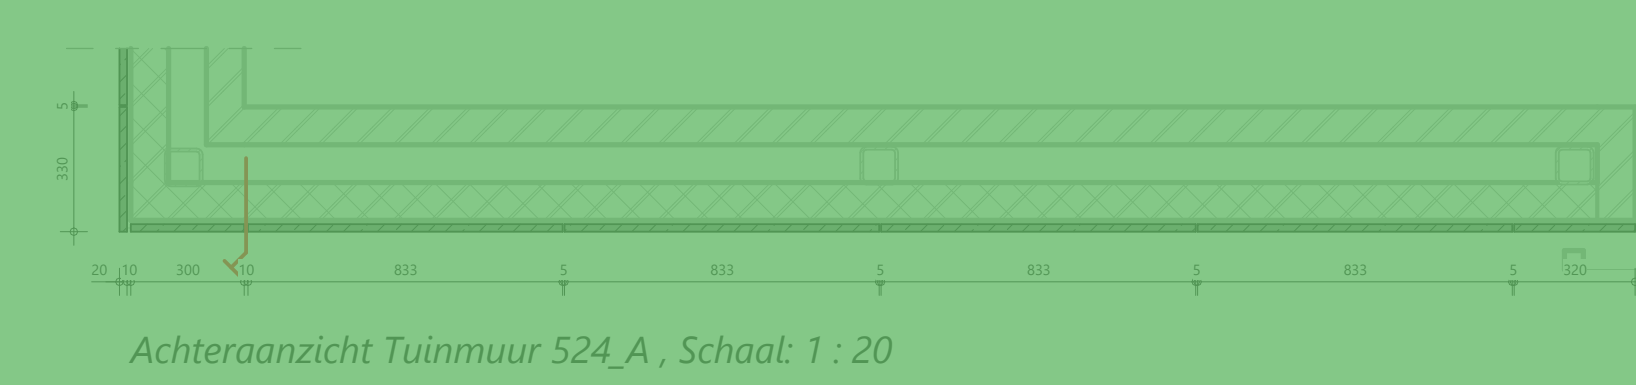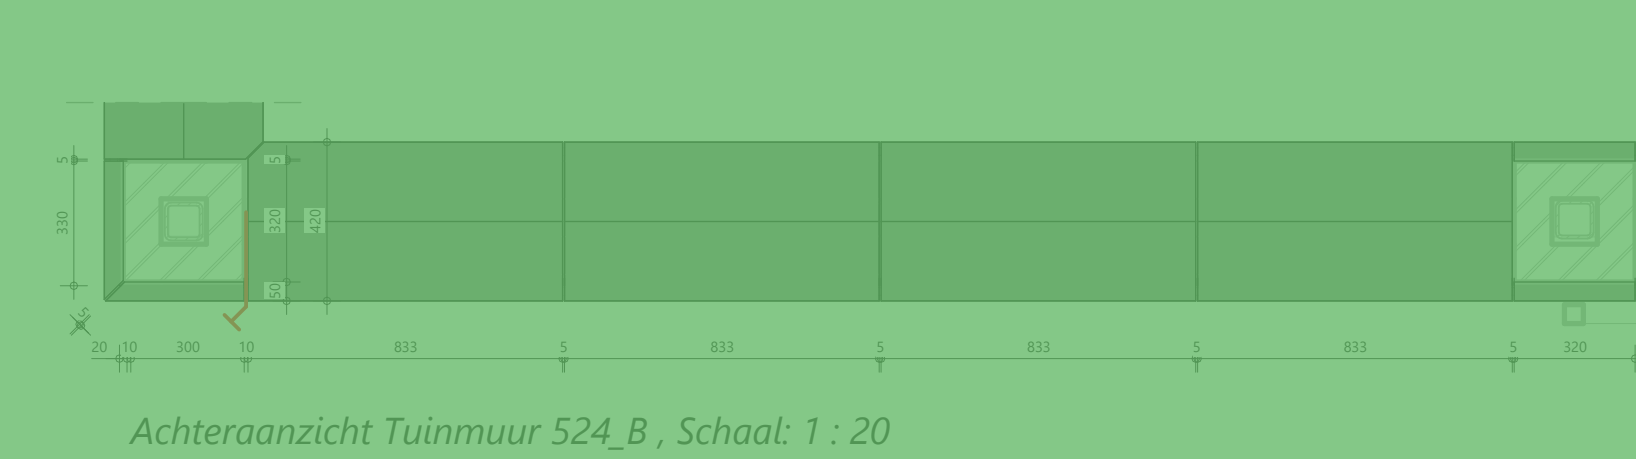

Achteraanzicht Tuinmuur 524, Schaal: 1 : 20

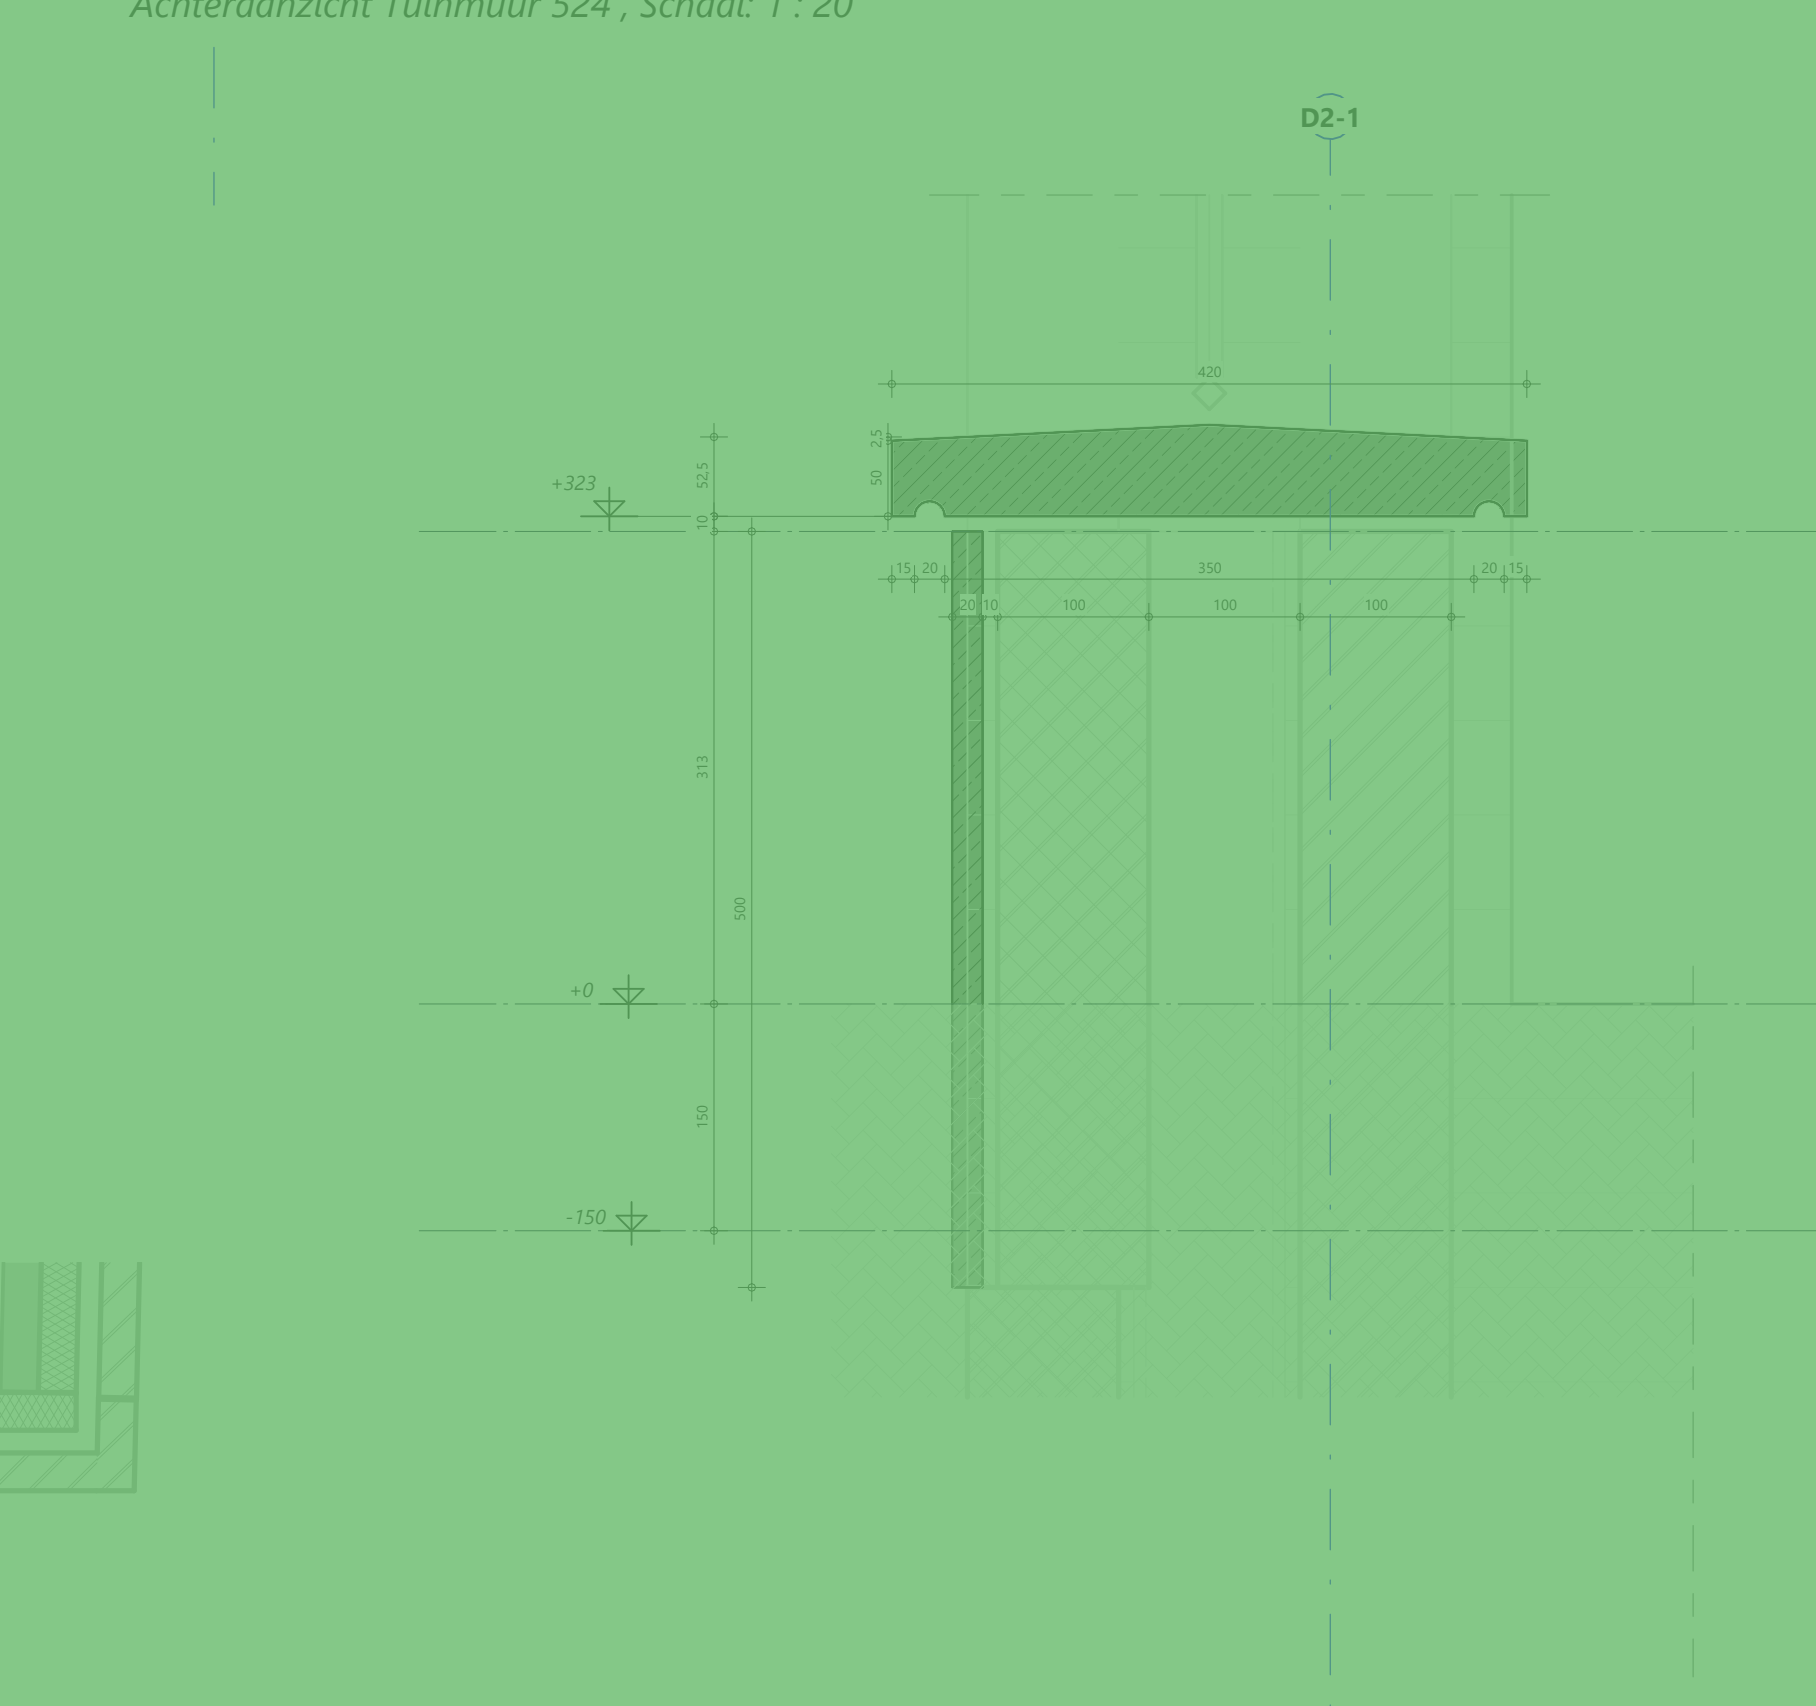

E2.16.a, Schaal: 1 : 5



NATUURSTEEN	
Gevelplint	Belgisch hardsteen bewerking: grip geschaurd / Mule Gris by hand nageschaurd dikte: 20 mm voegter: 5 mm standaard 10 mm s.p.v open steenvoegdilatatie
Overlengte	Alle panelen met dit symbool hebben 50mm overlengte
• Klouwk door dertien aan te brengen	
• Ter plaatse van muurveld dient straanwerk minimaal 50 mm vrijgehouden te worden en voorzichtig aangebracht	
• Bewestigten in natuursteen randafstand minimaal 70 mm aanhouden	
• Natuursteen is spanninggevoelig bewestigten met zorg en zonder spanning aandraaien	

Zijaanzichten E2

Nieuw Kralingen Fase 5
Ruud Lubberslaan 380-371, Rotterdam

Opdrachtgever: Ontwikkelcombinatie Nieuw Kralingen

Projectnr: 2932
Fase: UD
Auteur: IMol

Formaat: A3
Schaal: 1:20 / 1:5
17-02-2026
Status: Tekeningnr: 202

NEDERLANDSE
NATUURSTEEN
INDUSTRIE

Tekening opgesteld voor uitvoeringfase
Routen 17.0-2026-1433-1.0

De teek WMA 184 10091-06
Dierk van der Meulen
F. 06-1808011
E. info@nati.nl



NATUURSTEEN	
Gevelplint	Belgisch hardsteen bewerfing grijs-geschild / Mule Gris by hand nageschild dikte: 20 mm voegen: 5 mm standaard 10 mm i.p.v. open stootvoeg/dilatatie
Overlengte	* Alle panelen met dit symbool hebben 50mm overlengte
* Kwerk door derden aan te brengen. * Ter plaatse van maaiveld dient staalwerk minimaal 50 mm vrijgehouden te worden en voorzichtig aangelegd. * Bewegingen in natuursteen: randafstand minimaal 70 mm aanhouden. * Natuursteen is spanningsovereenkomstig bewaard met zorg en zonder spanning aandragen.	
Vooraanzichten E2	
Nieuw Kralingen Fase 5 Rood-tubberslaan-380-374, Rotterdam	
Opdrachtgever: Ontwikkelcombinatie Nieuw Kralingen	
Projectnr: 2332	Formaat: A0
Fase: UD	Schaal: 1:25 / 1:5
Auteur: PMOI	T1 datum: 17-02-2026
	Status: Tekening: 201
Tegening ongeschikt voor uitvoeringsfase Geprijsd 17-02-2026 14:56:10	