


03

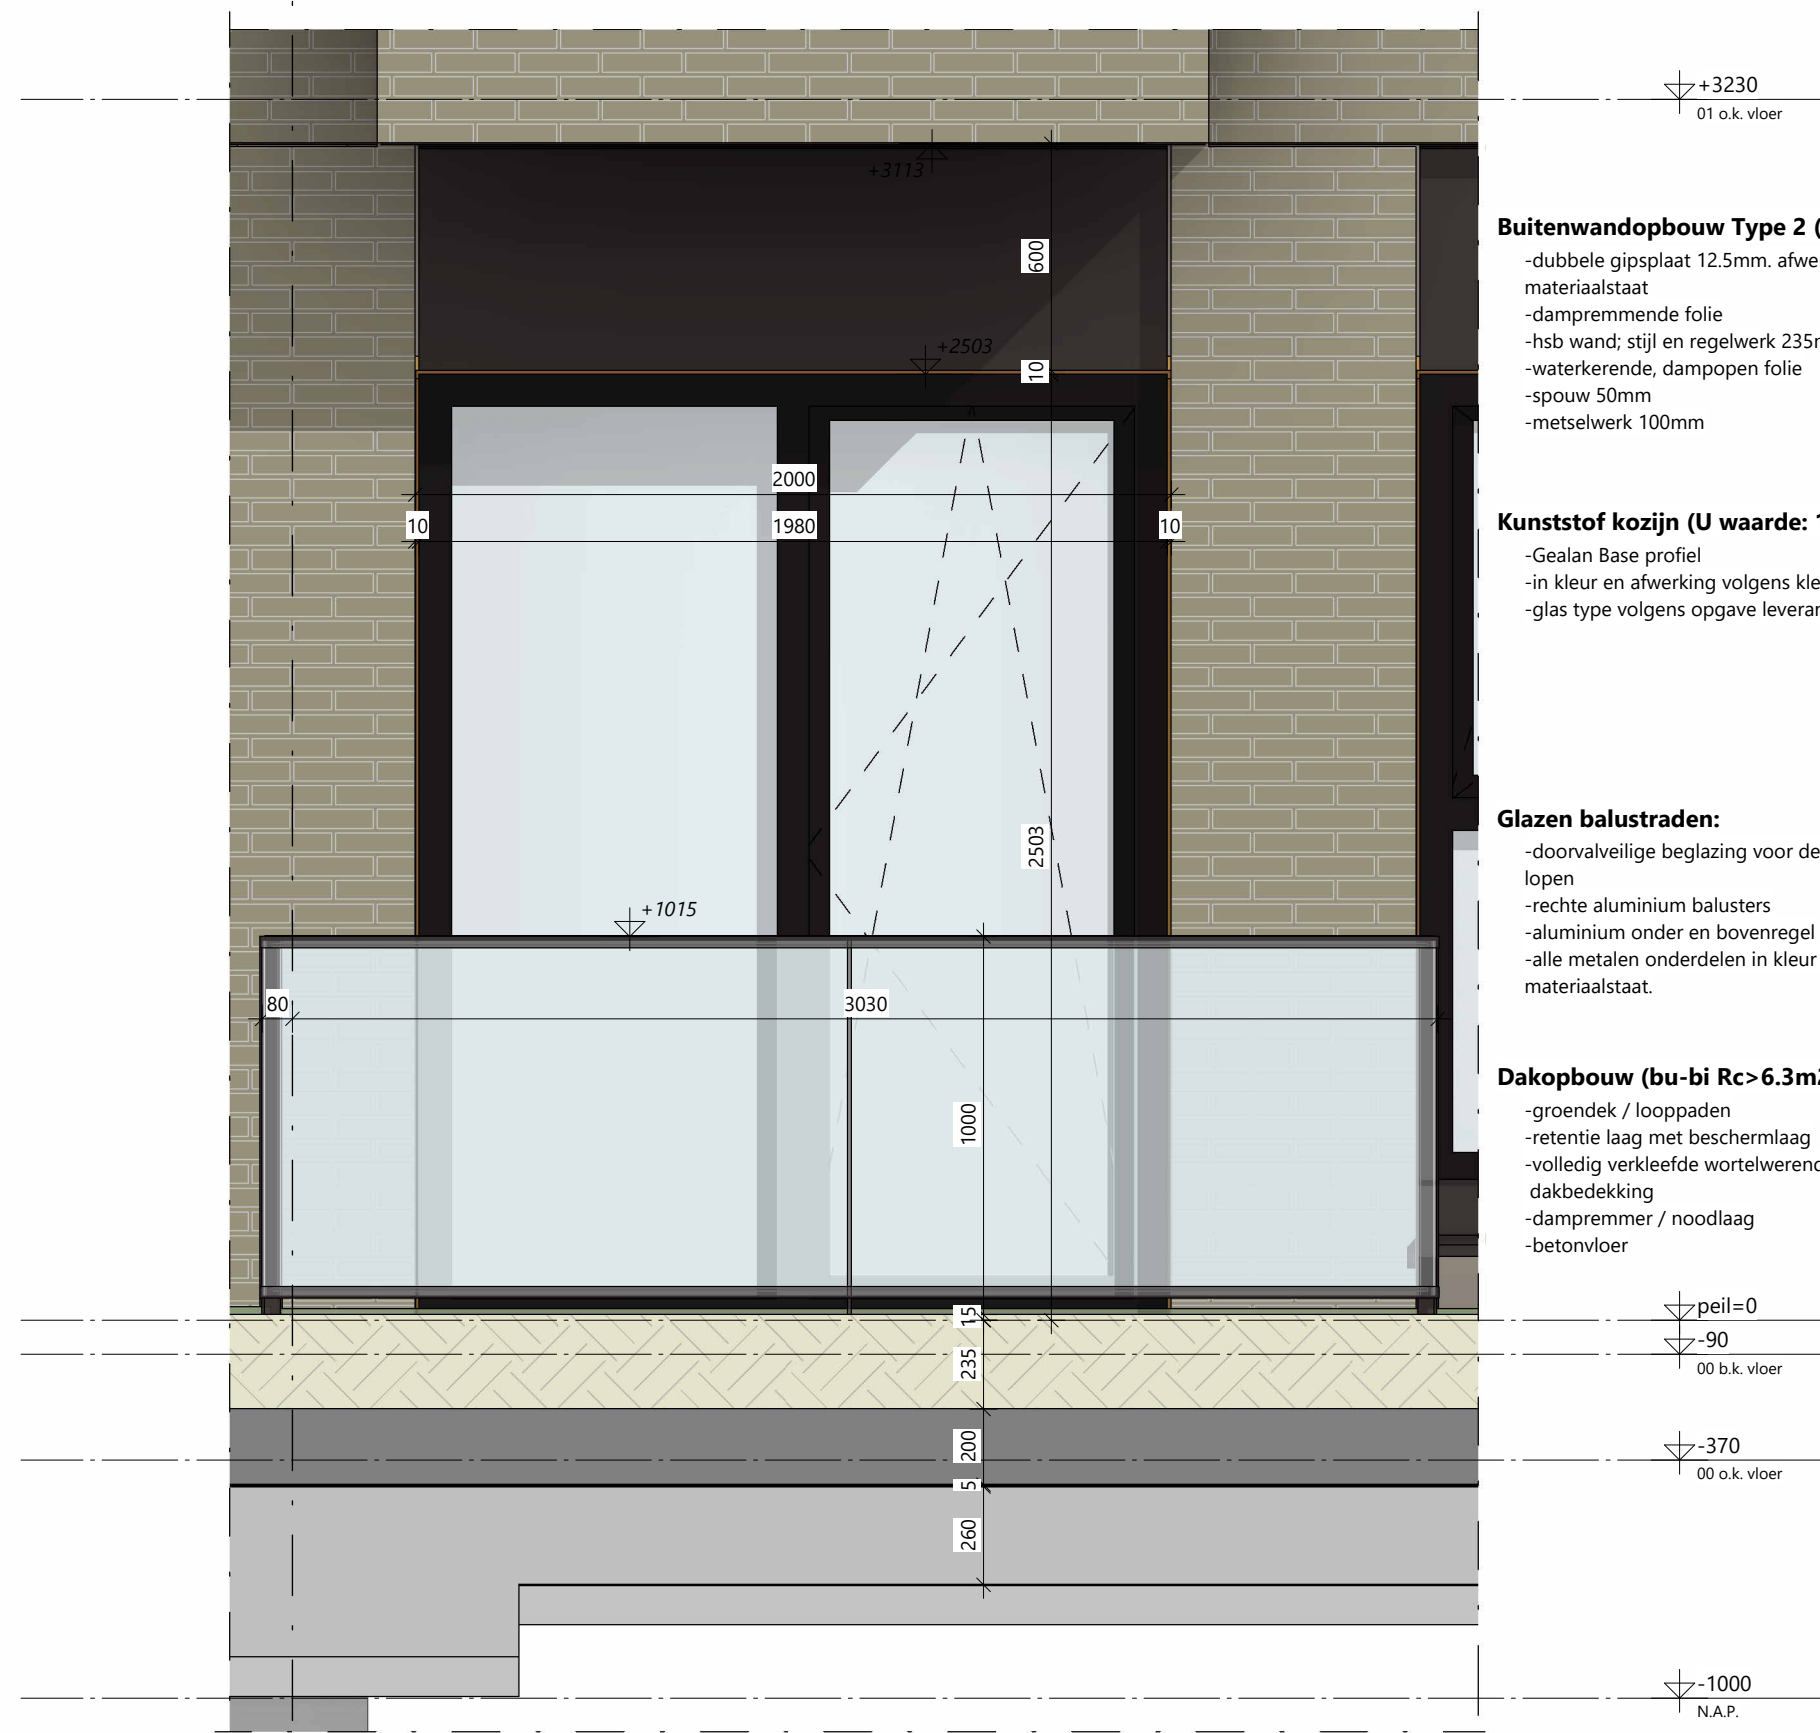

Buitenwandopbouw Type 2 (bi-bu $R_c > 4.7 \text{ m}^2 \text{ K} / \text{W}$):

- dubbele gipsplaat 12.5mm. afwerking volgens kleur en materiaalstaat
- dampremmende folie
- hsb wand; stijl en regelwerk 235mm,
- waterkerende, dampopen folie
- spouw 50mm
- metselwerk 100mm

Kunststof kozijn (U waarde: 1.1 W/mK)

- Gealan Base profiel
- in kleur en afwerking volgens kleur en materiaal staat
- glas type volgens opgave leverancier


Glazen balustraden:

- doorvalveilige beglazing voor de balusters langs laten lopen
- rechte aluminium balusters
- aluminium onder en bovenregel
- alle metalen onderdelen in kleur volgens kleur en materiaalstaat.

Dakopbouw (bu-bi $R_c > 6.3 \text{ m}^2 \text{ K} / \text{W}$):

- groendek / looppaden
- retentie laag met beschermlaag
- volledig verkleefde wortelwerende bitumeuze dakbedekking
- dampremmer / noodlaag
- betonvloer

03

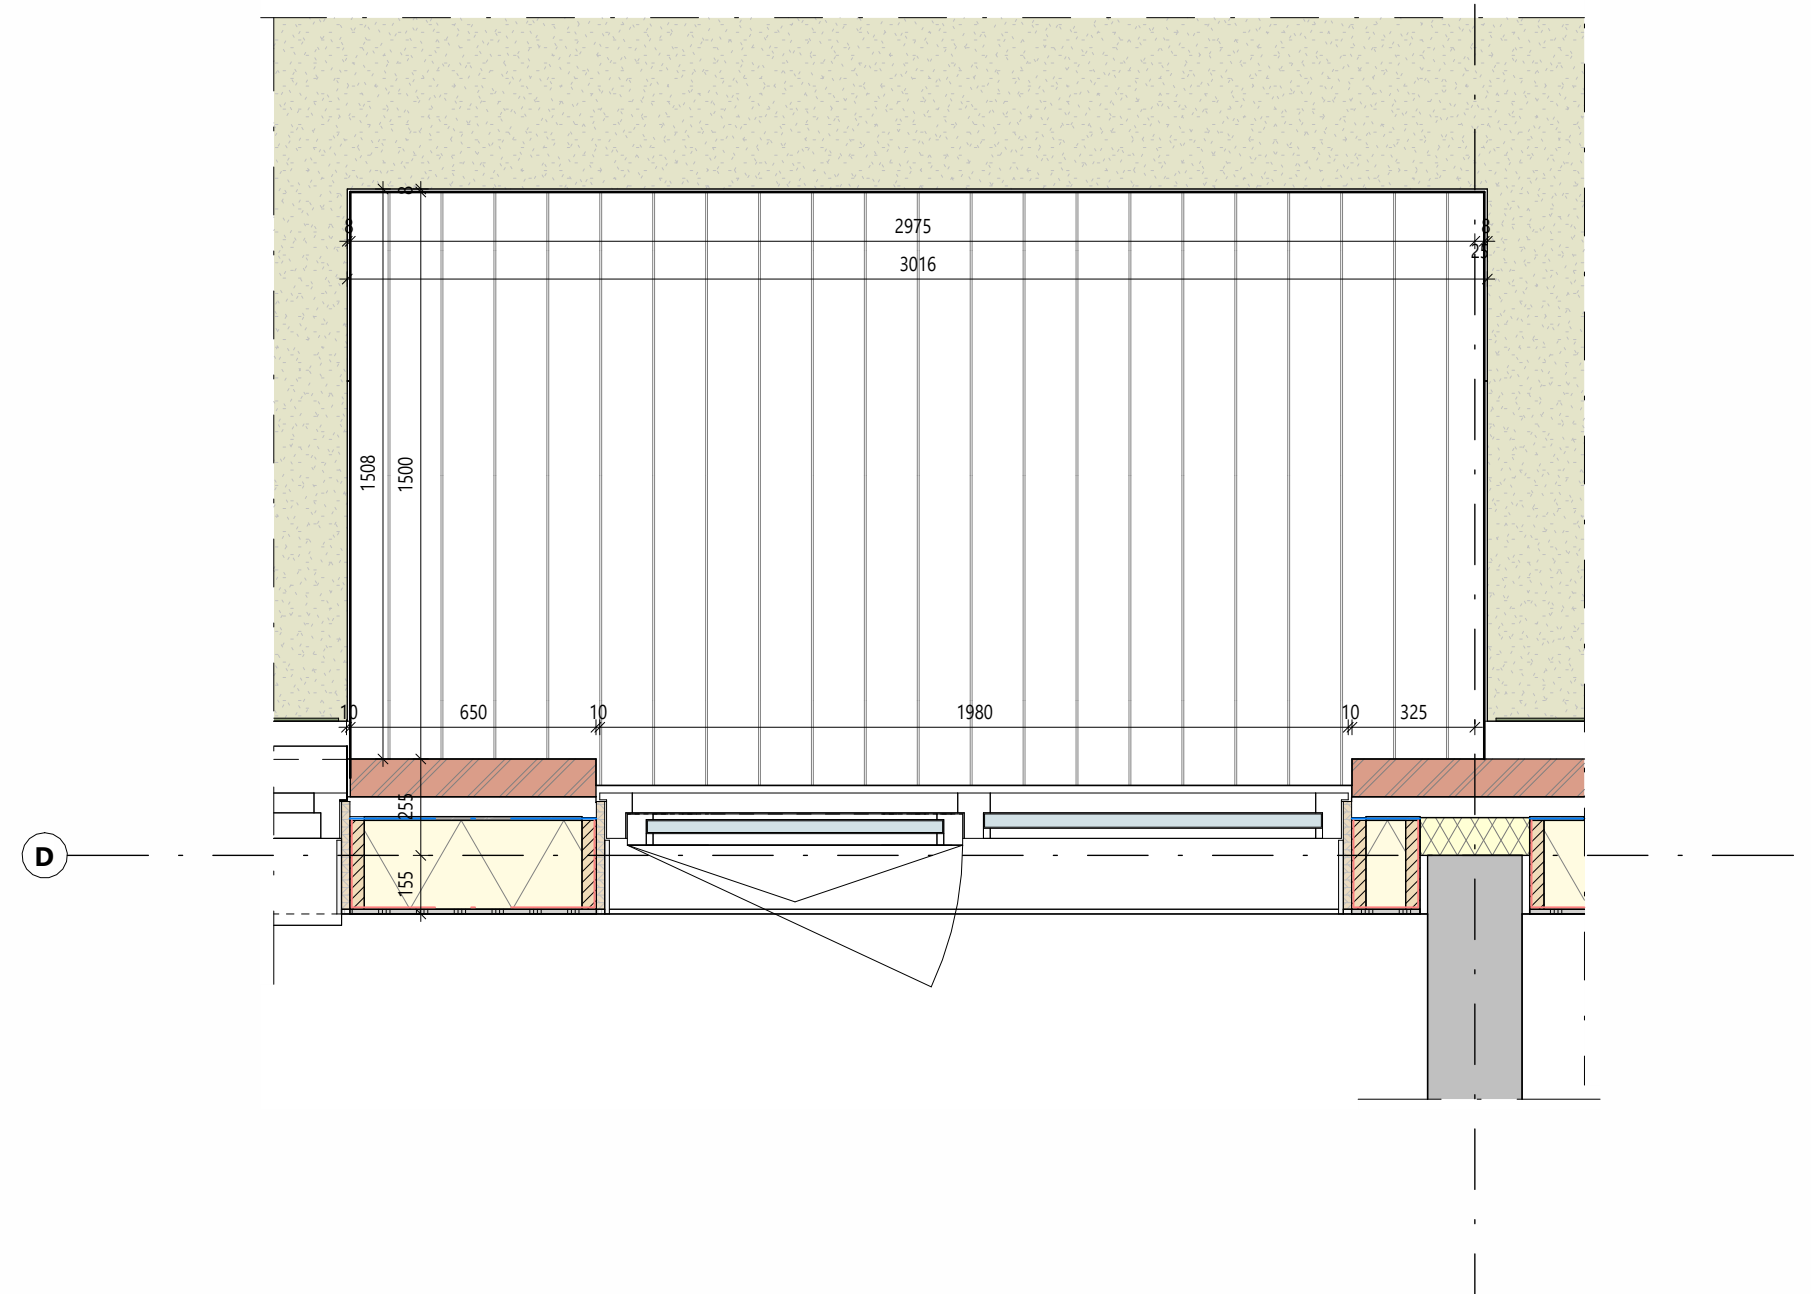

STUDIO
OXS

Piekstraat 27
3071 EL Rotterdam
+31 (0)6 41 23 22 49
info@studiooxs.com

fragment plg balkon bg

Gouda Harderwijkweg
Harderwijkweg 4, Gouda

Opdrachtgever: Create Realestate Raul Godron

Projectnr: 2459
Fase: TO
Auteur: JKolthof

Formaat: A2
Schaal: 1:20
1^e datum: 10-11-2025
Status: Definitief
Tekeningnr: TO-501


3bm
Ingenieurs van oplossingen

Tekening ongeschikt voor uitvoeringsfase
Geprint 8-11-2025 17:54:03

3BM Bouwkunde
Wattstraat 17
3335 LV Zwijndrecht

Tel: 078 7400 258
jochem@3bm.co.nl
www.3bm.co.nl



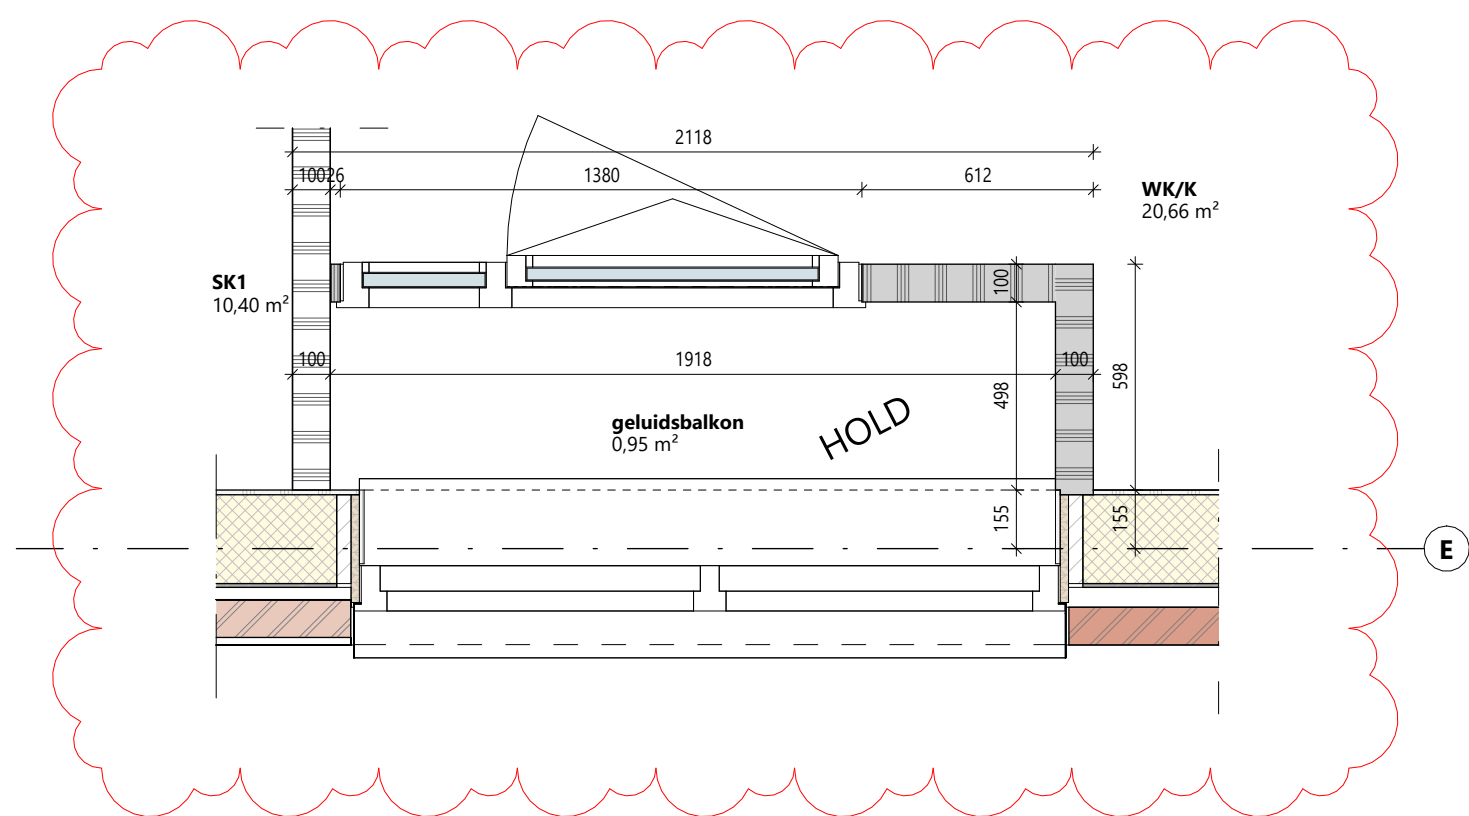

STUDIO
OXS

Piekstraat 27
3071 EL Rotterdam
+31 (0)6 41 23 22 49
info@studiooxs.com

A. **fagment plg balkon geluid**

B. Gouda Harderwijkweg
C. Harderwijkweg 4, Gouda

D. Opdrachtgever: Create Realestate Raul Godron

E. **Projectnr:** 2459
Fase: TO
Auteur: JKolthof

Formaat: A2
Schaal: 1:20
1^e datum: 10-11-2025
Status: Definitief
Tekeningnr: TO-502




F. **3bm**
Ingenieurs van oplossingen

Tekening ongeschikt voor uitvoeringsfase
Geprint 8-11-2025 17:54:03

3BM Bouwkunde
Wattstraat 17
3335 LV Zwijndrecht

Tel: 078 7400 258
jochem@3bm.co.nl
www.3bm.co.nl



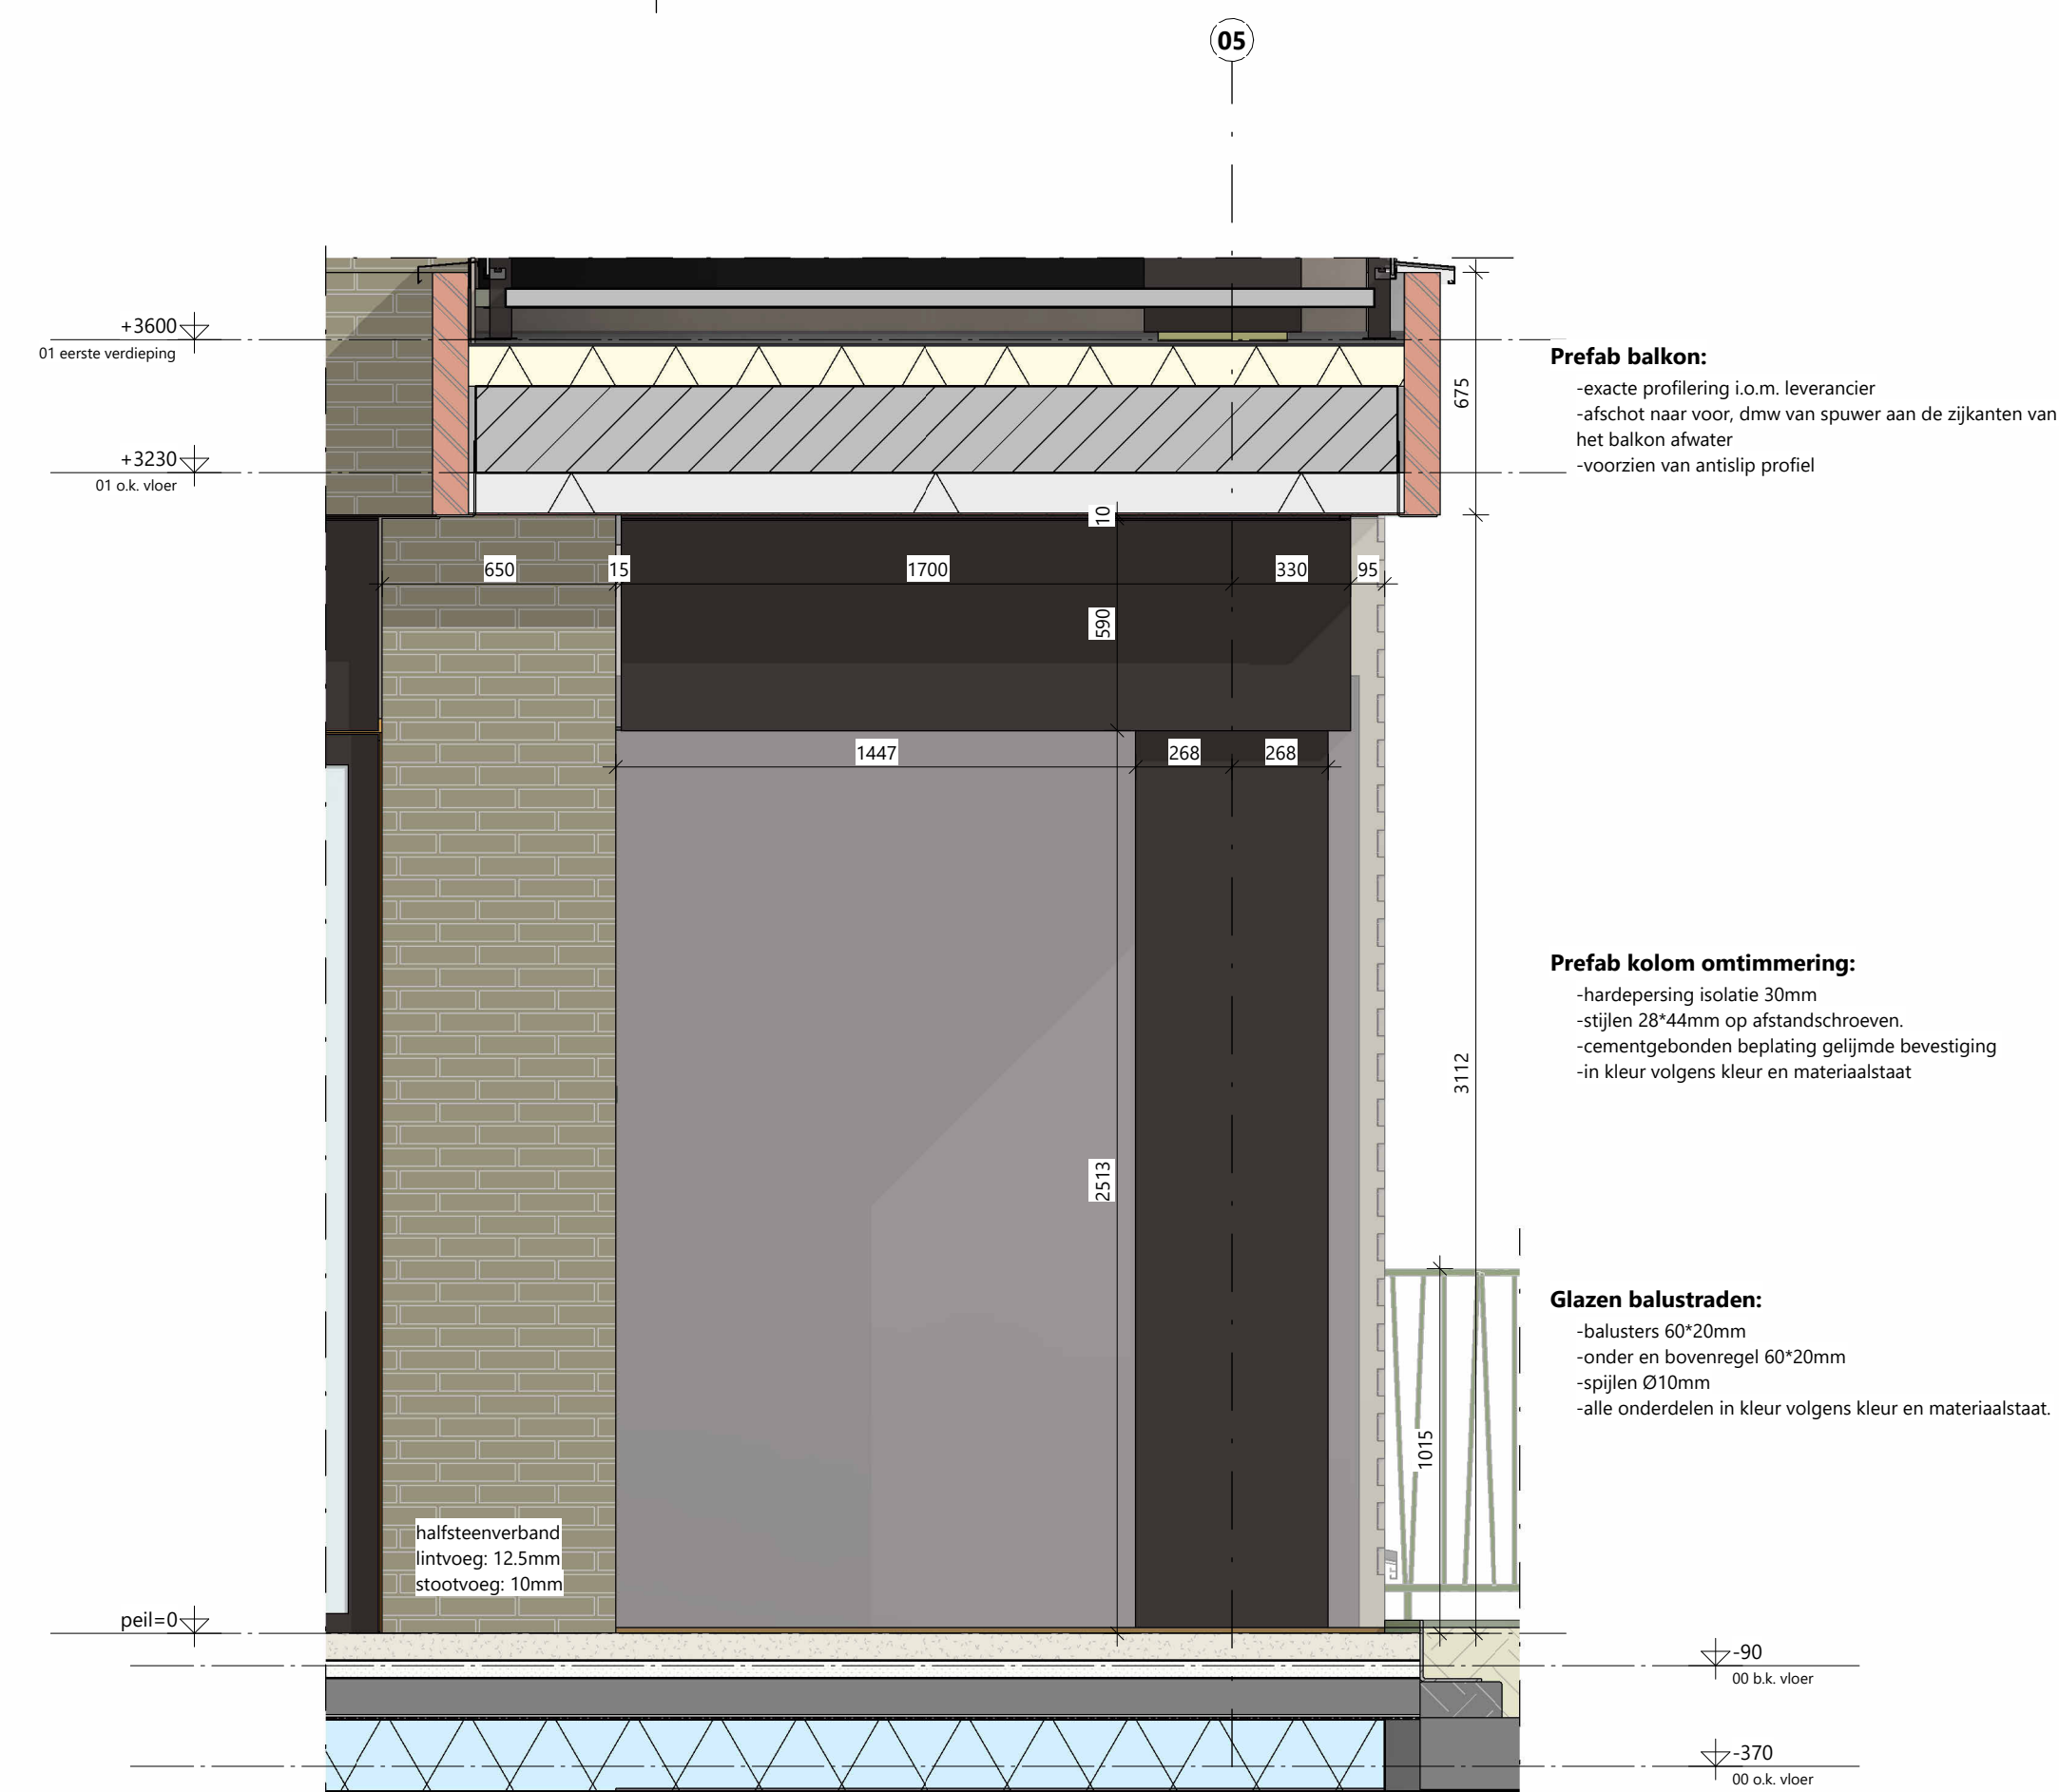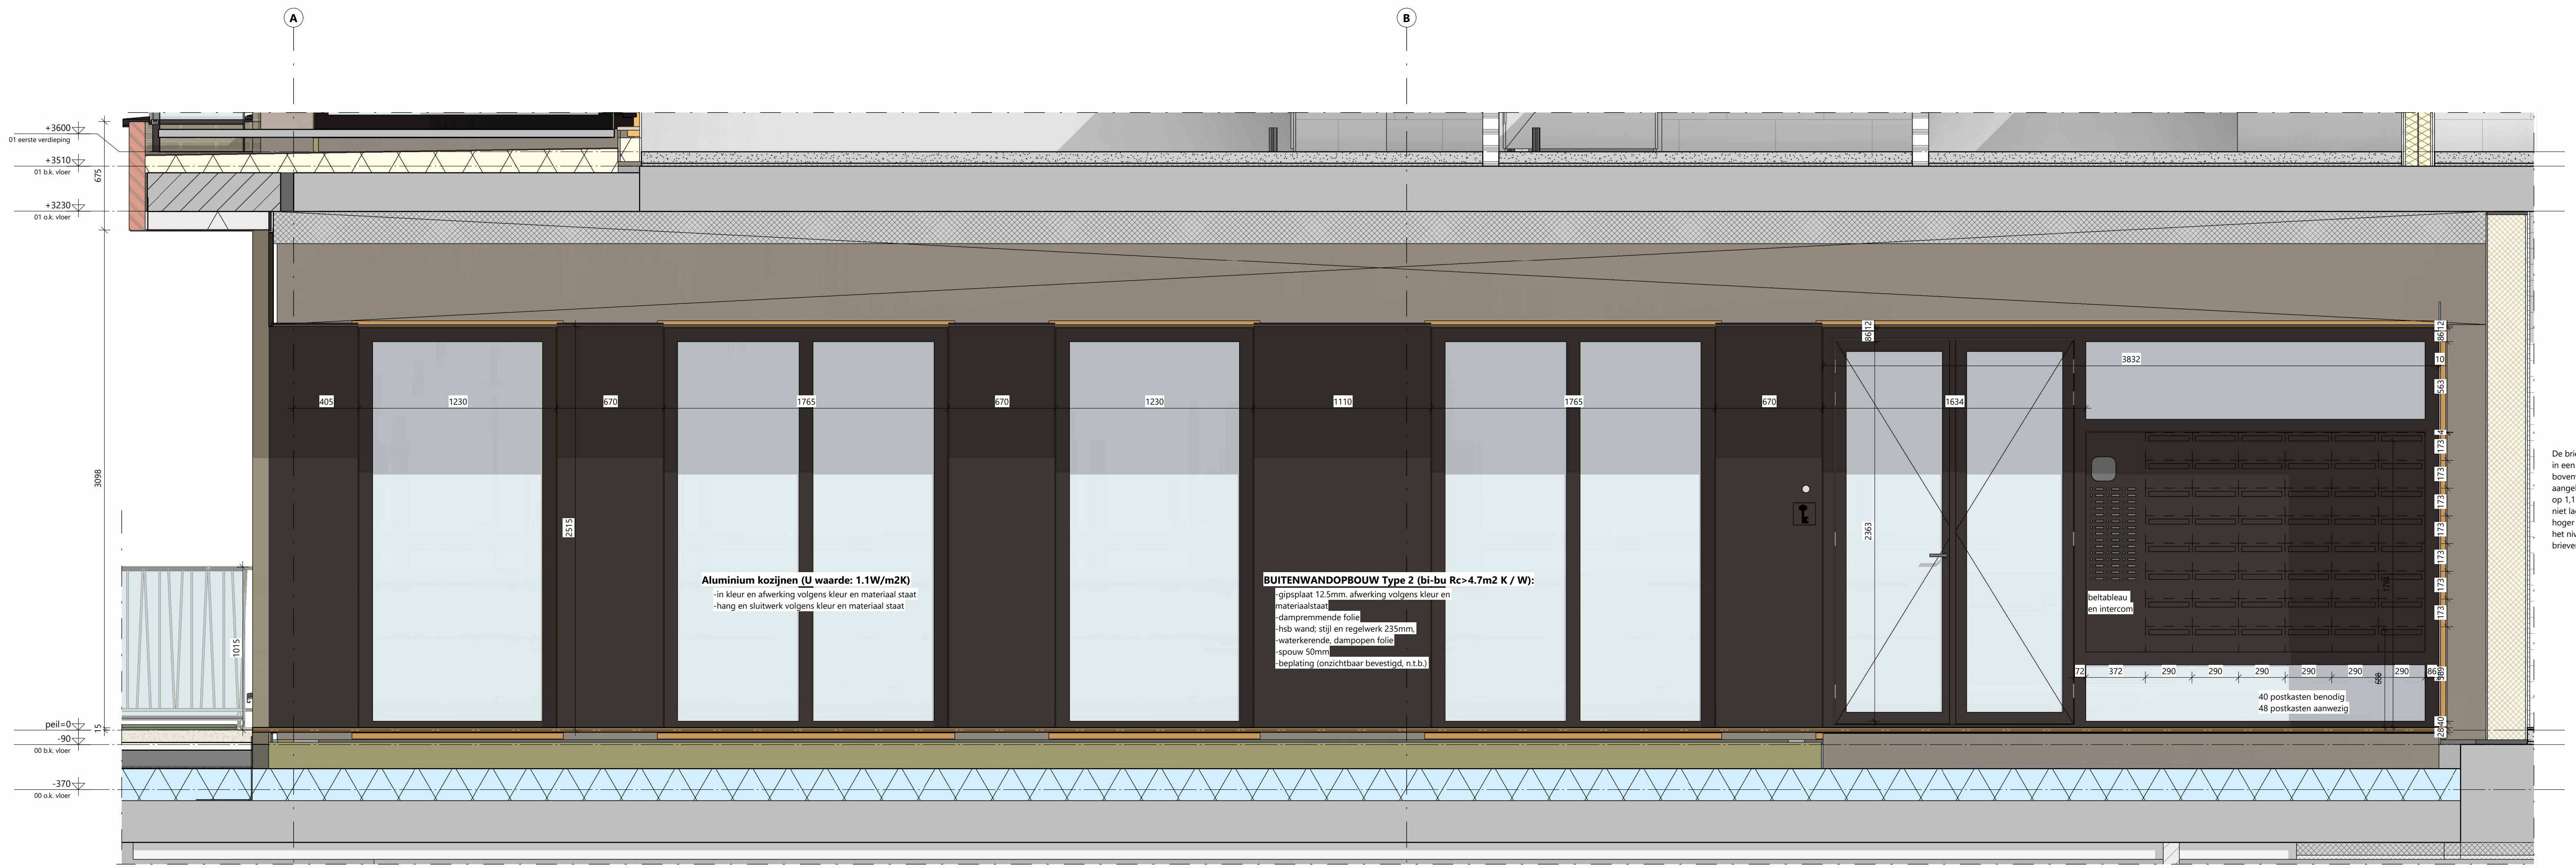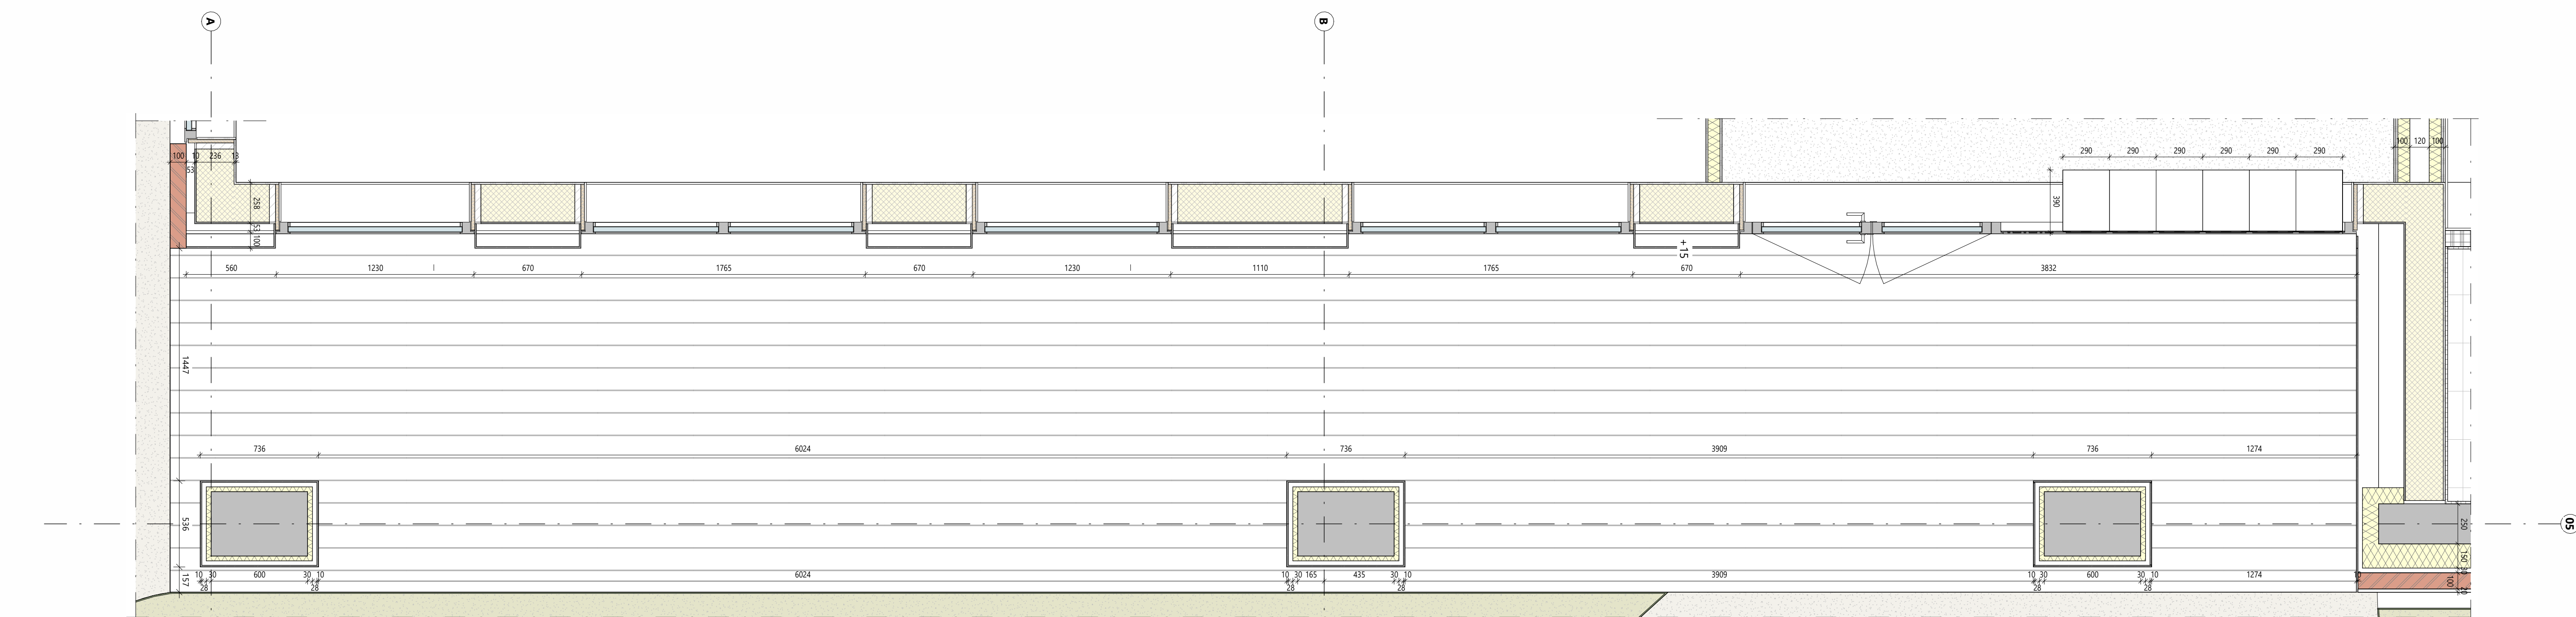

De binnenvloer is horizontaal en een verticaal vlak of in het bovenvlak van de binnenvloer aangebracht en bevindt zich op 1,1 meter of in ieder geval niet lager dan 0,6 meter of hoger dan 1,8 meter boven het niveau, waarop de binnenvloer wordt bedeld.


Aluminium kozijnen (U waarde: 1.1W/m2K)
in kleur en afwerking volgens kleur en materiaal staat
hang en dubbel volgens kleur en materiaal staat

BUITENWANDOPBOUW Type 2 (bi-bu Rc=4.7m2 K / W):
- typeplaat 12.5mm afwerking volgens kleur en materiaal staat
- dampremmende folie
- Hsb wand zij en regwerk 235mm
- waterkerende dampopen folie
- gewo 50mm
- bevestiging (onzichtbaar bevestigd, n.b.)

Prefab balkon:
- exacte profieling i.o.m. leverancier
- afsluit naar voor, dmv van spouwer aan de zijken van het balkon afsluit
- voorzien van antislip profiel

Prefab kolom omtimmering:
- wandopening isolatie 30mm
- stijlen 38x44mm op afstandschroeven
- cementgebonden beplating gefinide bevestiging
- in kleur volgens kleur en materiaal staat

Glazen balustraden:
- bakstenen 60x20mm
- onder en bovenzijde 60x20mm
- stijlen 38x44mm
- alle onderdelen in kleur volgens kleur en materiaal staat

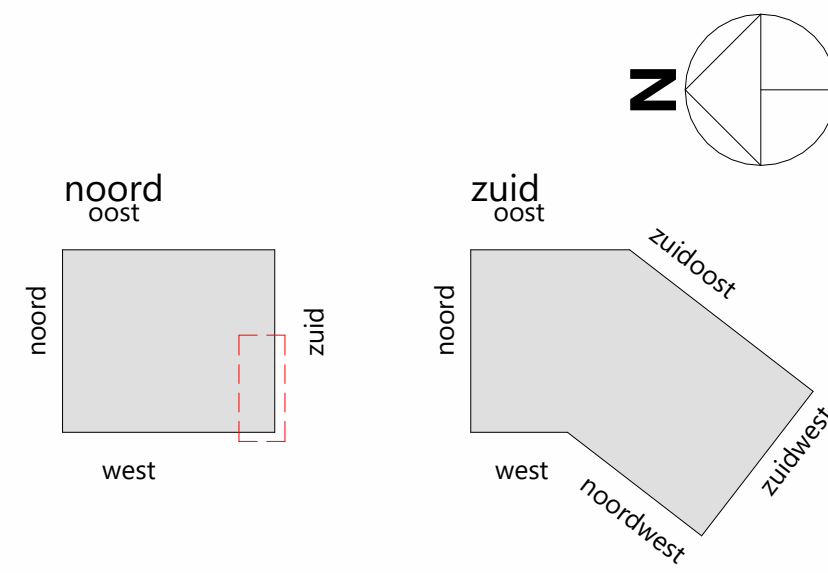

STUDIO
OXs

fragment entree noord

Gouda Harderwijkweg
Harderwijkweg 4, Gouda

Opdrachtgever: Create Realstate Raul Godron

Projectnr: 2459
Fase: TO
Auteur: JKethof

Formaat: A0
Schale: 1:20
1e datum: 10-11-2025
Status: Definitief
Tekeningnr: TO-S06

3bm
Ingenieurs van oplossingen

Tekening ongeschikt voor uitvoeringsfase
Gedrukt: 8-11-2025 17:54:18
PLOT: Architectuur-TO-S06-001-001 - Gouda KOLPWS TO-BMW-005-001

Piekstraat 27
3071 EL Rotterdam
+31 (0)6 41 23 22 49
info@studiooxs.com

3BM Bouwkunde
Watersstraat 17
3335 LV Zoetermeer
Tel: 078 7400 250
jochem@3bm.nl
www.3bm.nl





Kunststof kozijn (U waarde: 1.1 W/mK)

-Gulden Base profiel
-in kleur en afwerking volgens kleur en materiaal staat
-glas type volgens opgave leverancier



Kunststof kozijn (U waarde: 1.1 W/mK)

-Gulden Base profiel
-in kleur en afwerking volgens kleur en materiaal staat
-glas type volgens opgave leverancier

Buitenwandoopbouw Type 1 (bi-bu Rc=4.7m2 K / W):

-betonwand rhwg 250mm
-isolatie 152mm
-spouw 48mm
-waterkerende dampopen folie
-metaalwerk 100mm



Kunststof kozijn (U waarde: 1.1 W/mK)

-Gulden Base profiel
-in kleur en afwerking volgens kleur en materiaal staat
-glas type volgens opgave leverancier

Prefab gevelbanden


-Prefab betonvorm elementen
-voorzien van steerstrips
-haken uitvoeren met bodestrips
-Beweging i.o.m. leverancier

Gevelopbouw Type 4 (bi-bu Rc=4.7m2 K / W):

-betonvorm
-isolatie d=20mm
-luchtopbouw d=28mm
-regelwerk op afstandschroeven
-beplating volgens kleur en materiaalstaat
-onzichtbare (fijn) beweeging

Glazen balustraden:

-doorvallende beglazing voor de balustrade lange lopen
-rechte aluminium balustrade
-aluminium onder en bovenregel
-alle metalen onderdelen in kleur volgens kleur en materiaalstaat

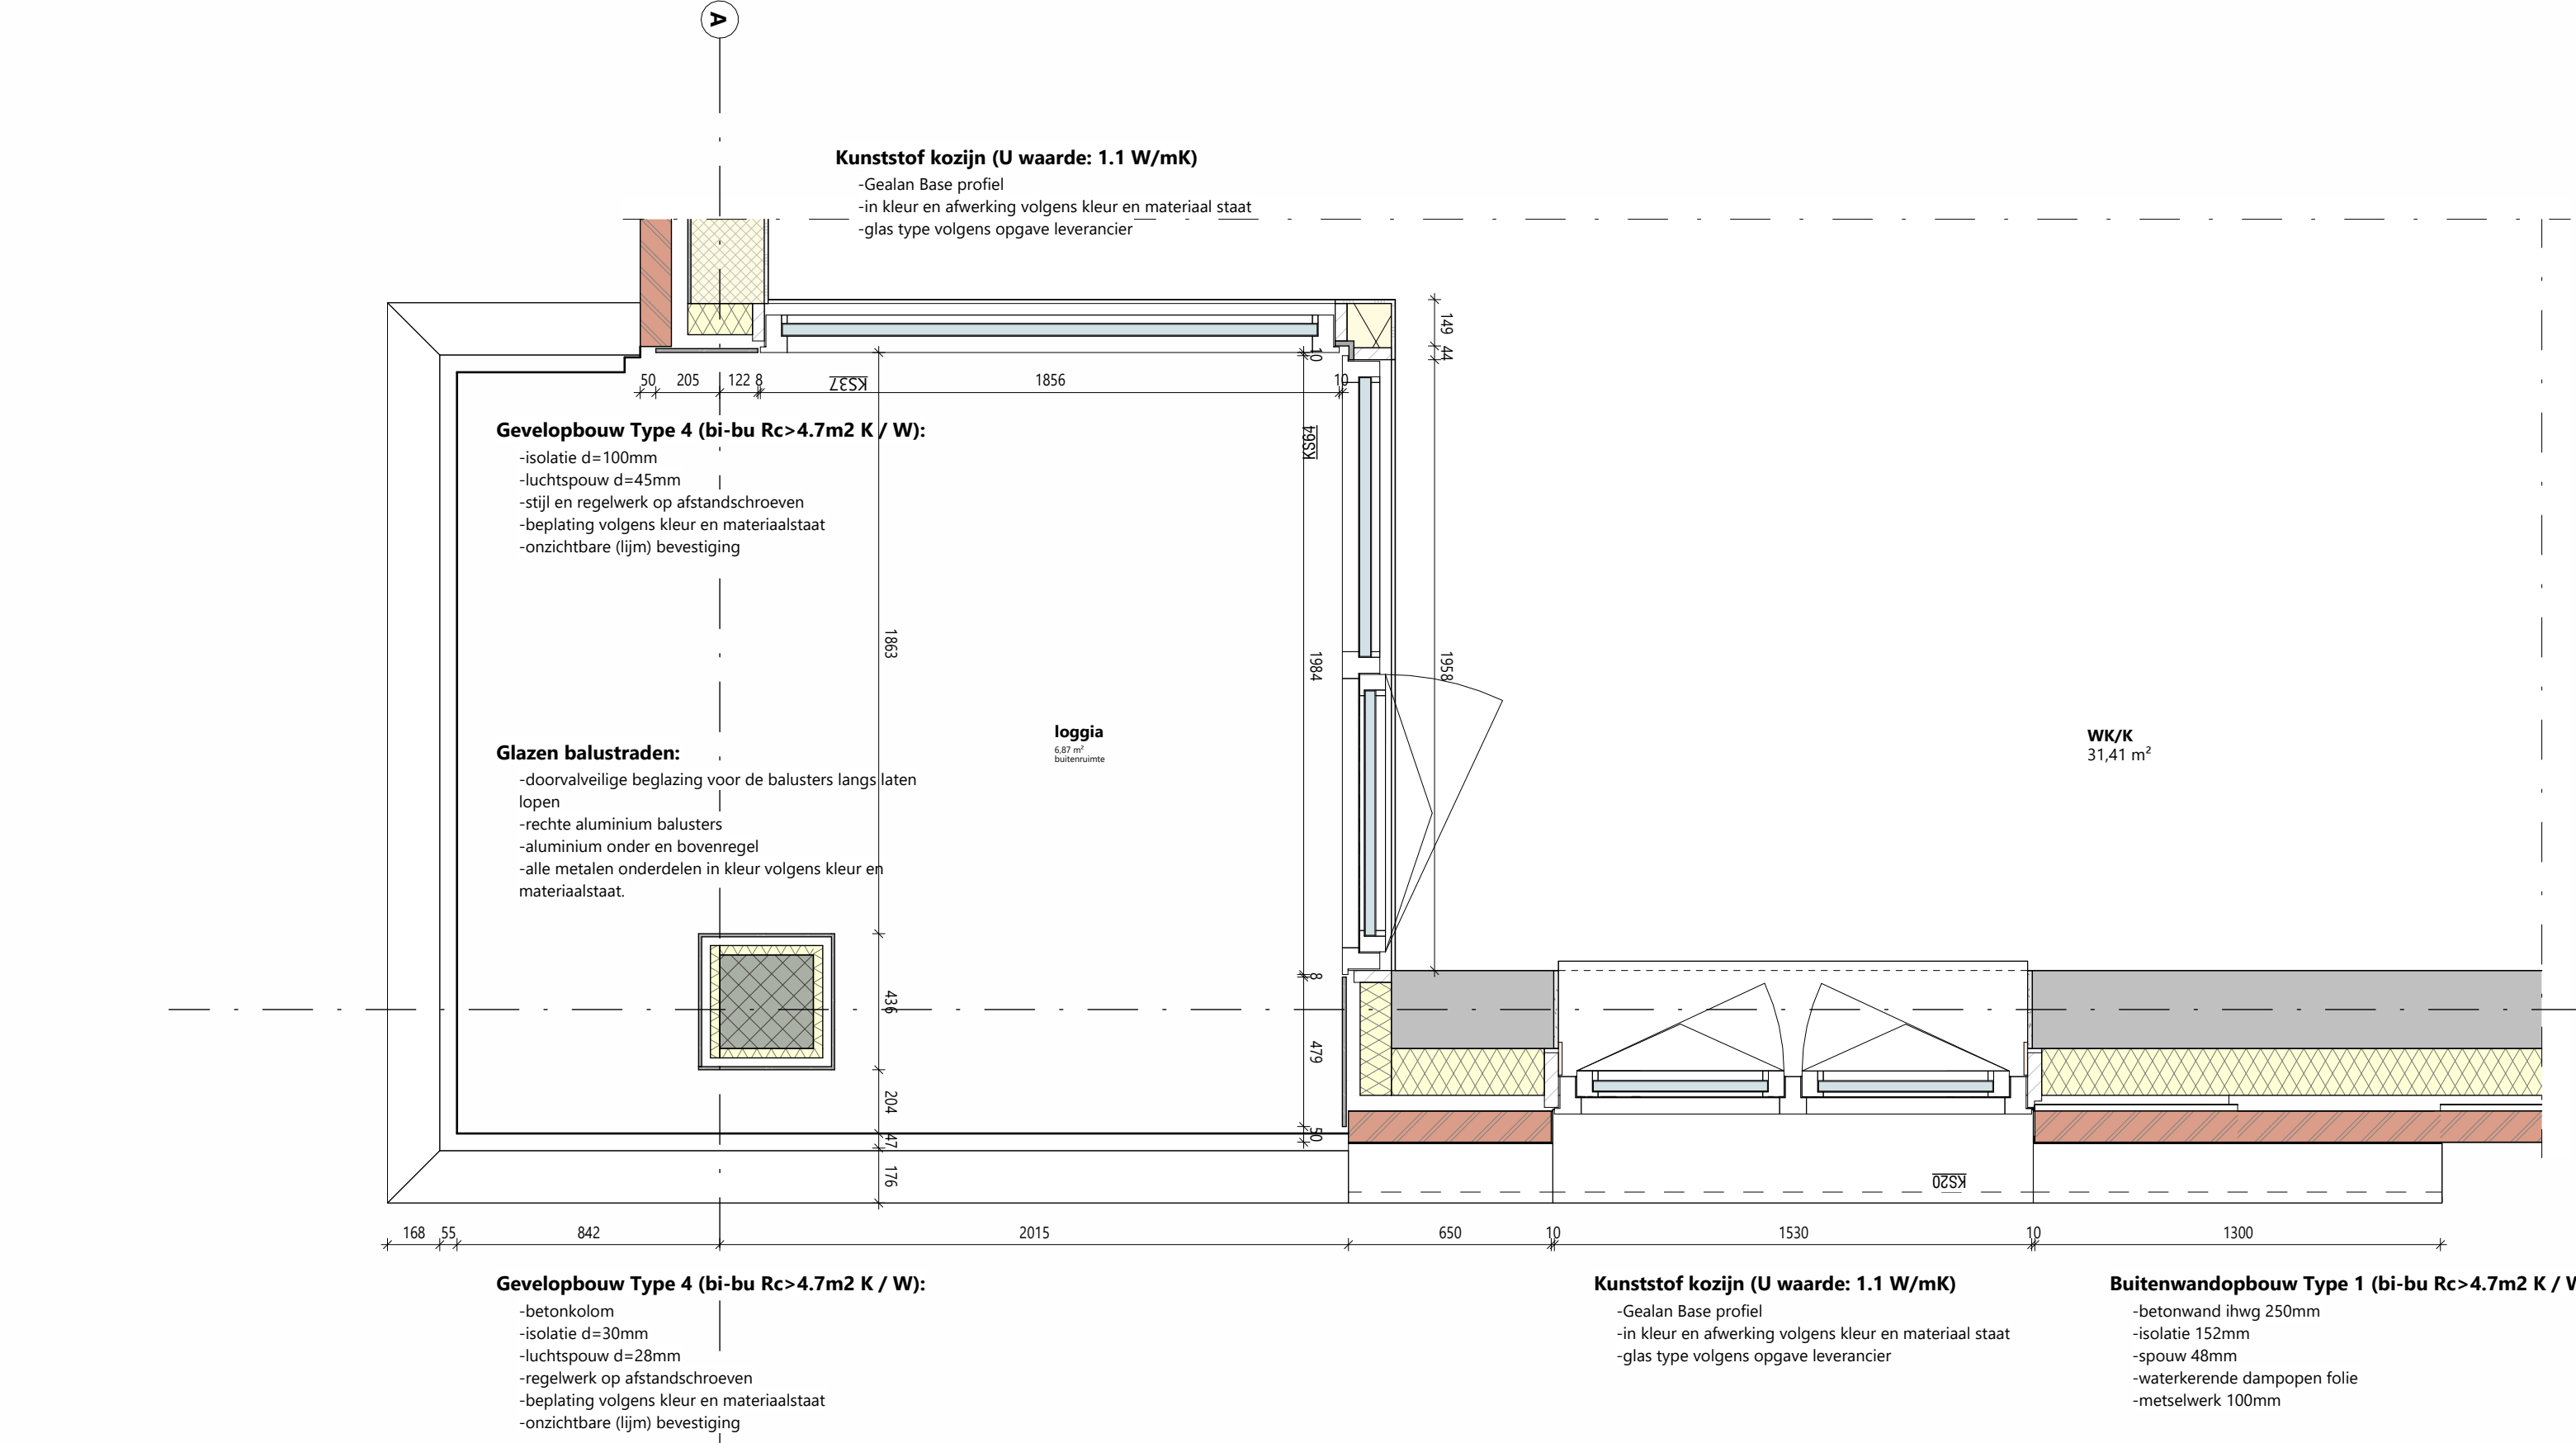

Kunststof kozijn (U waarde: 1.1 W/mK)

-Gulden Base profiel
-in kleur en afwerking volgens kleur en materiaal staat
-glas type volgens opgave leverancier

Gevelopbouw Type 4 (bi-bu Rc=4.7m2 K / W):

-betonvorm
-isolatie d=20mm
-luchtopbouw d=28mm
-regelwerk op afstandschroeven
-beplating volgens kleur en materiaalstaat
-onzichtbare (fijn) beweeging

Glazen balustraden:


-doorvallende beglazing voor de balustrade lange lopen
-rechte aluminium balustrade
-aluminium onder en bovenregel
-alle metalen onderdelen in kleur volgens kleur en materiaalstaat

Kunststof kozijn (U waarde: 1.1 W/mK)

-Gulden Base profiel
-in kleur en afwerking volgens kleur en materiaal staat
-glas type volgens opgave leverancier

Buitenwandoopbouw Type 1 (bi-bu Rc=4.7m2 K / W):

-betonwand rhwg 250mm
-isolatie 152mm
-spouw 48mm
-waterkerende dampopen folie
-metaalwerk 100mm

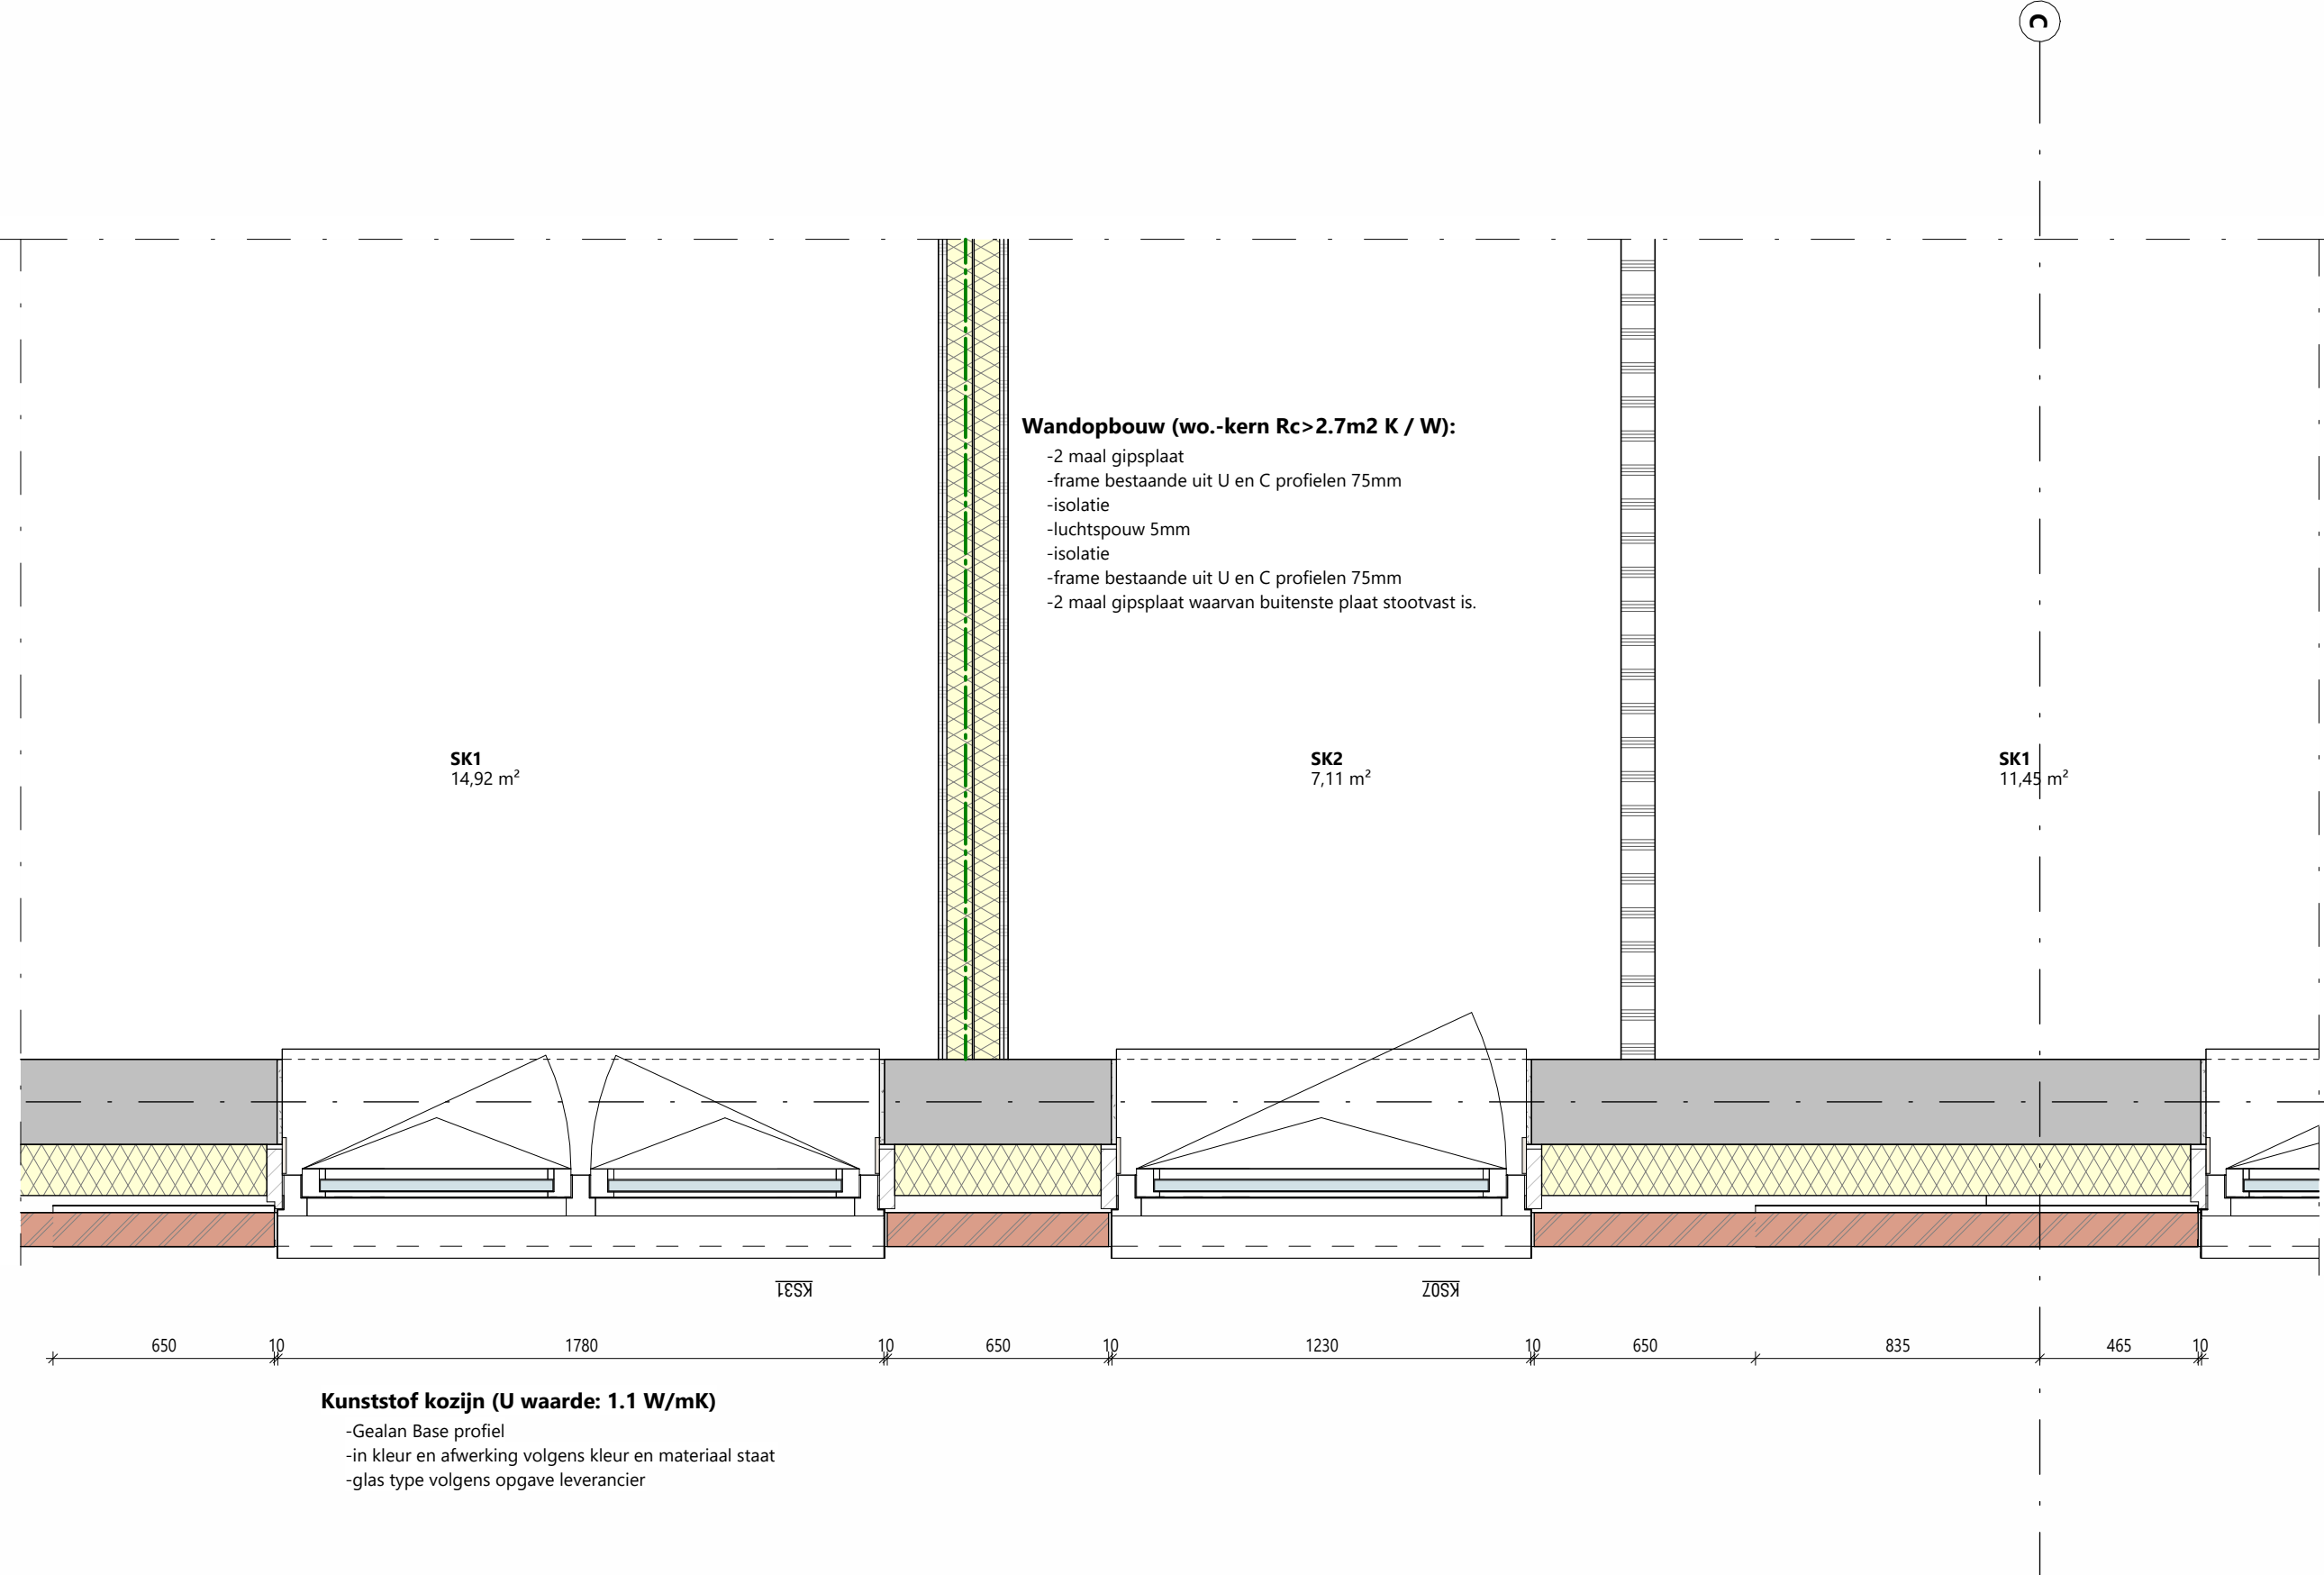


Kunststof kozijn (U waarde: 1.1 W/mK)

-Gulden Base profiel
-in kleur en afwerking volgens kleur en materiaal staat
-glas type volgens opgave leverancier

Wandopbouw (wo-kern Rc=2.7m2 K / W):

-2 maal gipsplaat
-Rame bestaande uit U en C profielen 75mm
-isolatie 152mm
-spouw 48mm
-waterkerende dampopen folie
-metaalwerk 100mm

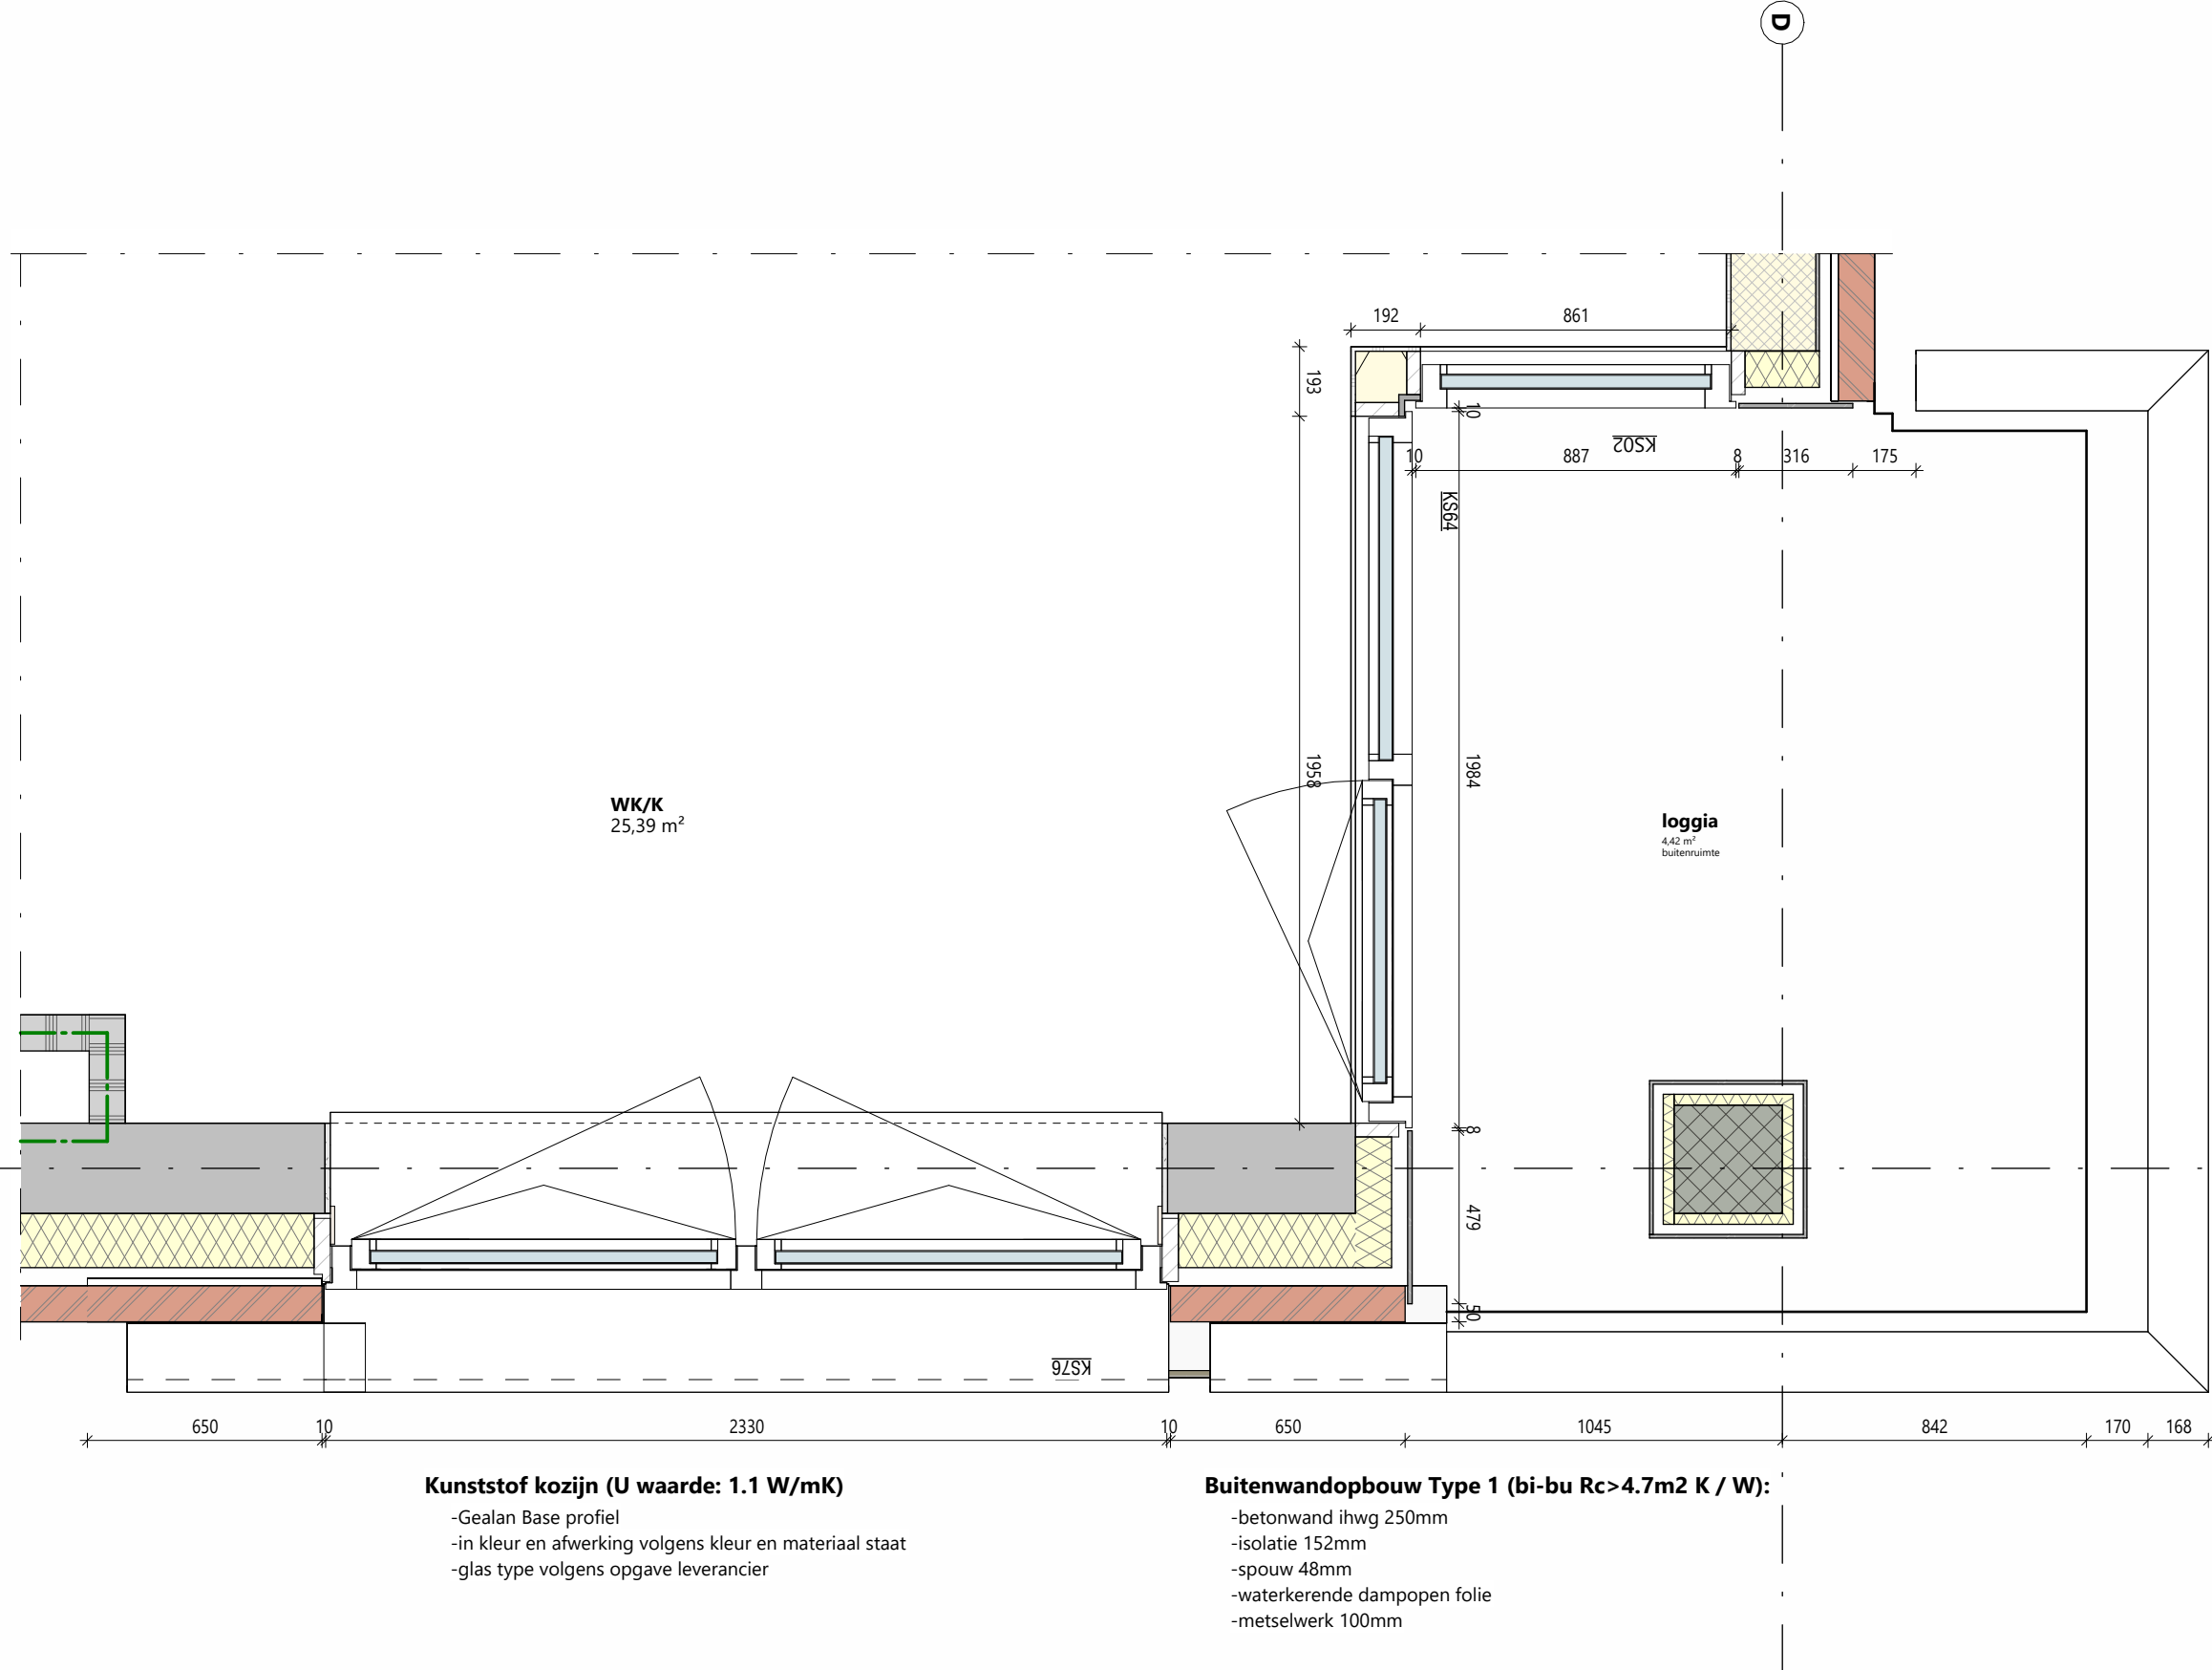


Kunststof kozijn (U waarde: 1.1 W/mK)

-Gulden Base profiel
-in kleur en afwerking volgens kleur en materiaal staat
-glas type volgens opgave leverancier

Buitenwandoopbouw Type 1 (bi-bu Rc=4.7m2 K / W):

-betonwand rhwg 250mm
-isolatie 152mm
-spouw 48mm
-waterkerende dampopen folie
-metaalwerk 100mm

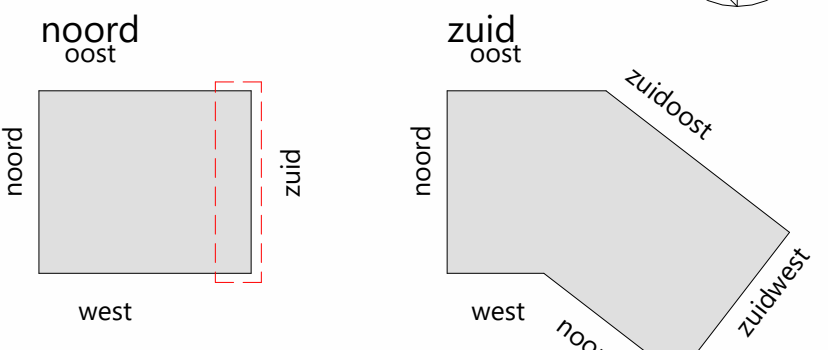

STUDIO
OXs

fragment gev noord

Gouda Harderwijkweg
Harderwijkweg 4, Gouda

Opdrachtgever: Create Realestate Raul Godron

Projectnr: 2459

Fase: TO

Auteur: J.Koithof

Formaat: A0
Schaal: 1:20
1st datum: 10-11-2025
Status: Definitief
Tekeningsnr: TO-507

3bm
Ingenieurs van oplossingen

Tekening ongeschikt voor uitvoeringsfase
Copieer 8-11-2025 17:54:30

Piekstraat 27
3071 EL Rotterdam
+31 (0)6 41 23 22 49
info@studiooxs.com

3BM Bouwkunde
Watstraat 17
3395 LV Zeijndrecht
Tel: 078 7400 258
jochen@3bm.co.nl
www.3bm.co.nl



STUDIO
OXs

fragment entree zuid

Gouda Harderwijkweg
Harderwijkweg 4, Gouda

Opdrachtgever: Create Realstate Raul Godron

Projectnr: 2459
Fase: TO
Auteur: J.Kalhof

Formaat: A0
Schale: 1:20
1* datum: 10-11-2025
Status: Definitief
Tekeningnr: TO-508

Tekening ongeschikt voor uitvoeringsfase
Geprint: 8-11-2025 17:54:42
Ploeg: Architect: StudioOXs Architect: Gouda KOLPWS TO-BMW_OXS.nl

3bm
Ingenieurs van oplossingen

Piekstraat 27
3071 EL Rotterdam
+31 (0)6 41 23 22 49
info@studiooxs.com

3BM Bouwkunde
Watersstraat 17
3335 LV Zoetermeer
Tel: 078 7460 256
jochem@3bm.co.nl
www.3bm.co.nl









- Prefab gevelbanden**
- Prefab bodemplaat
 - voorzien van steerstrips
 - hoeken uitvoeren met hoekstrips
 - Beweging i.o.m. leunwaaier
- Kunststof kozijn (U waarde: 1.1 W/mk)**
- Gralen Base profiel
 - in kleur en afwerking volgens kleur en materiaal staat
 - glas type volgens opgave leunwaaier
- Buitenwandopbouw Type 1 (bi-bu Rc=4.7m2 K / W):**
- betonwand 17mg 250mm
 - isolatie 120mm
 - spouw 40mm
 - waterkerende dampopen folie
 - metselwerk 100mm

- Kunststof kozijn (U waarde: 1.1 W/mk)**
- Gralen Base profiel
 - in kleur en afwerking volgens kleur en materiaal staat
 - glas type volgens opgave leunwaaier

- Kunststof kozijn (U waarde: 1.1 W/mk)**
- Gralen Base profiel
 - in kleur en afwerking volgens kleur en materiaal staat
 - glas type volgens opgave leunwaaier
- Prefab gevelbanden**
- Prefab bodemplaat
 - voorzien van steerstrips
 - hoeken uitvoeren met hoekstrips
 - Beweging i.o.m. leunwaaier

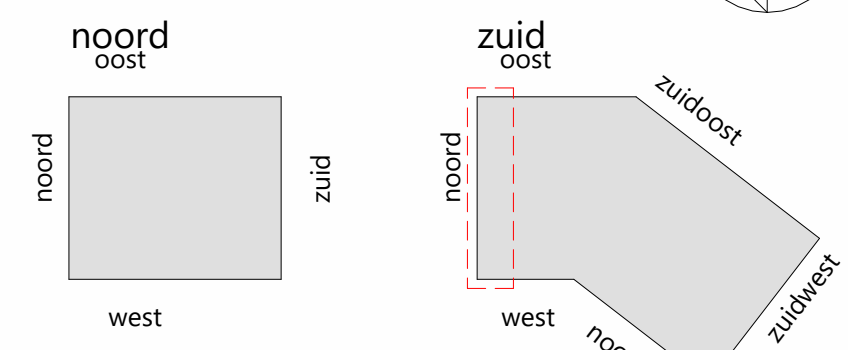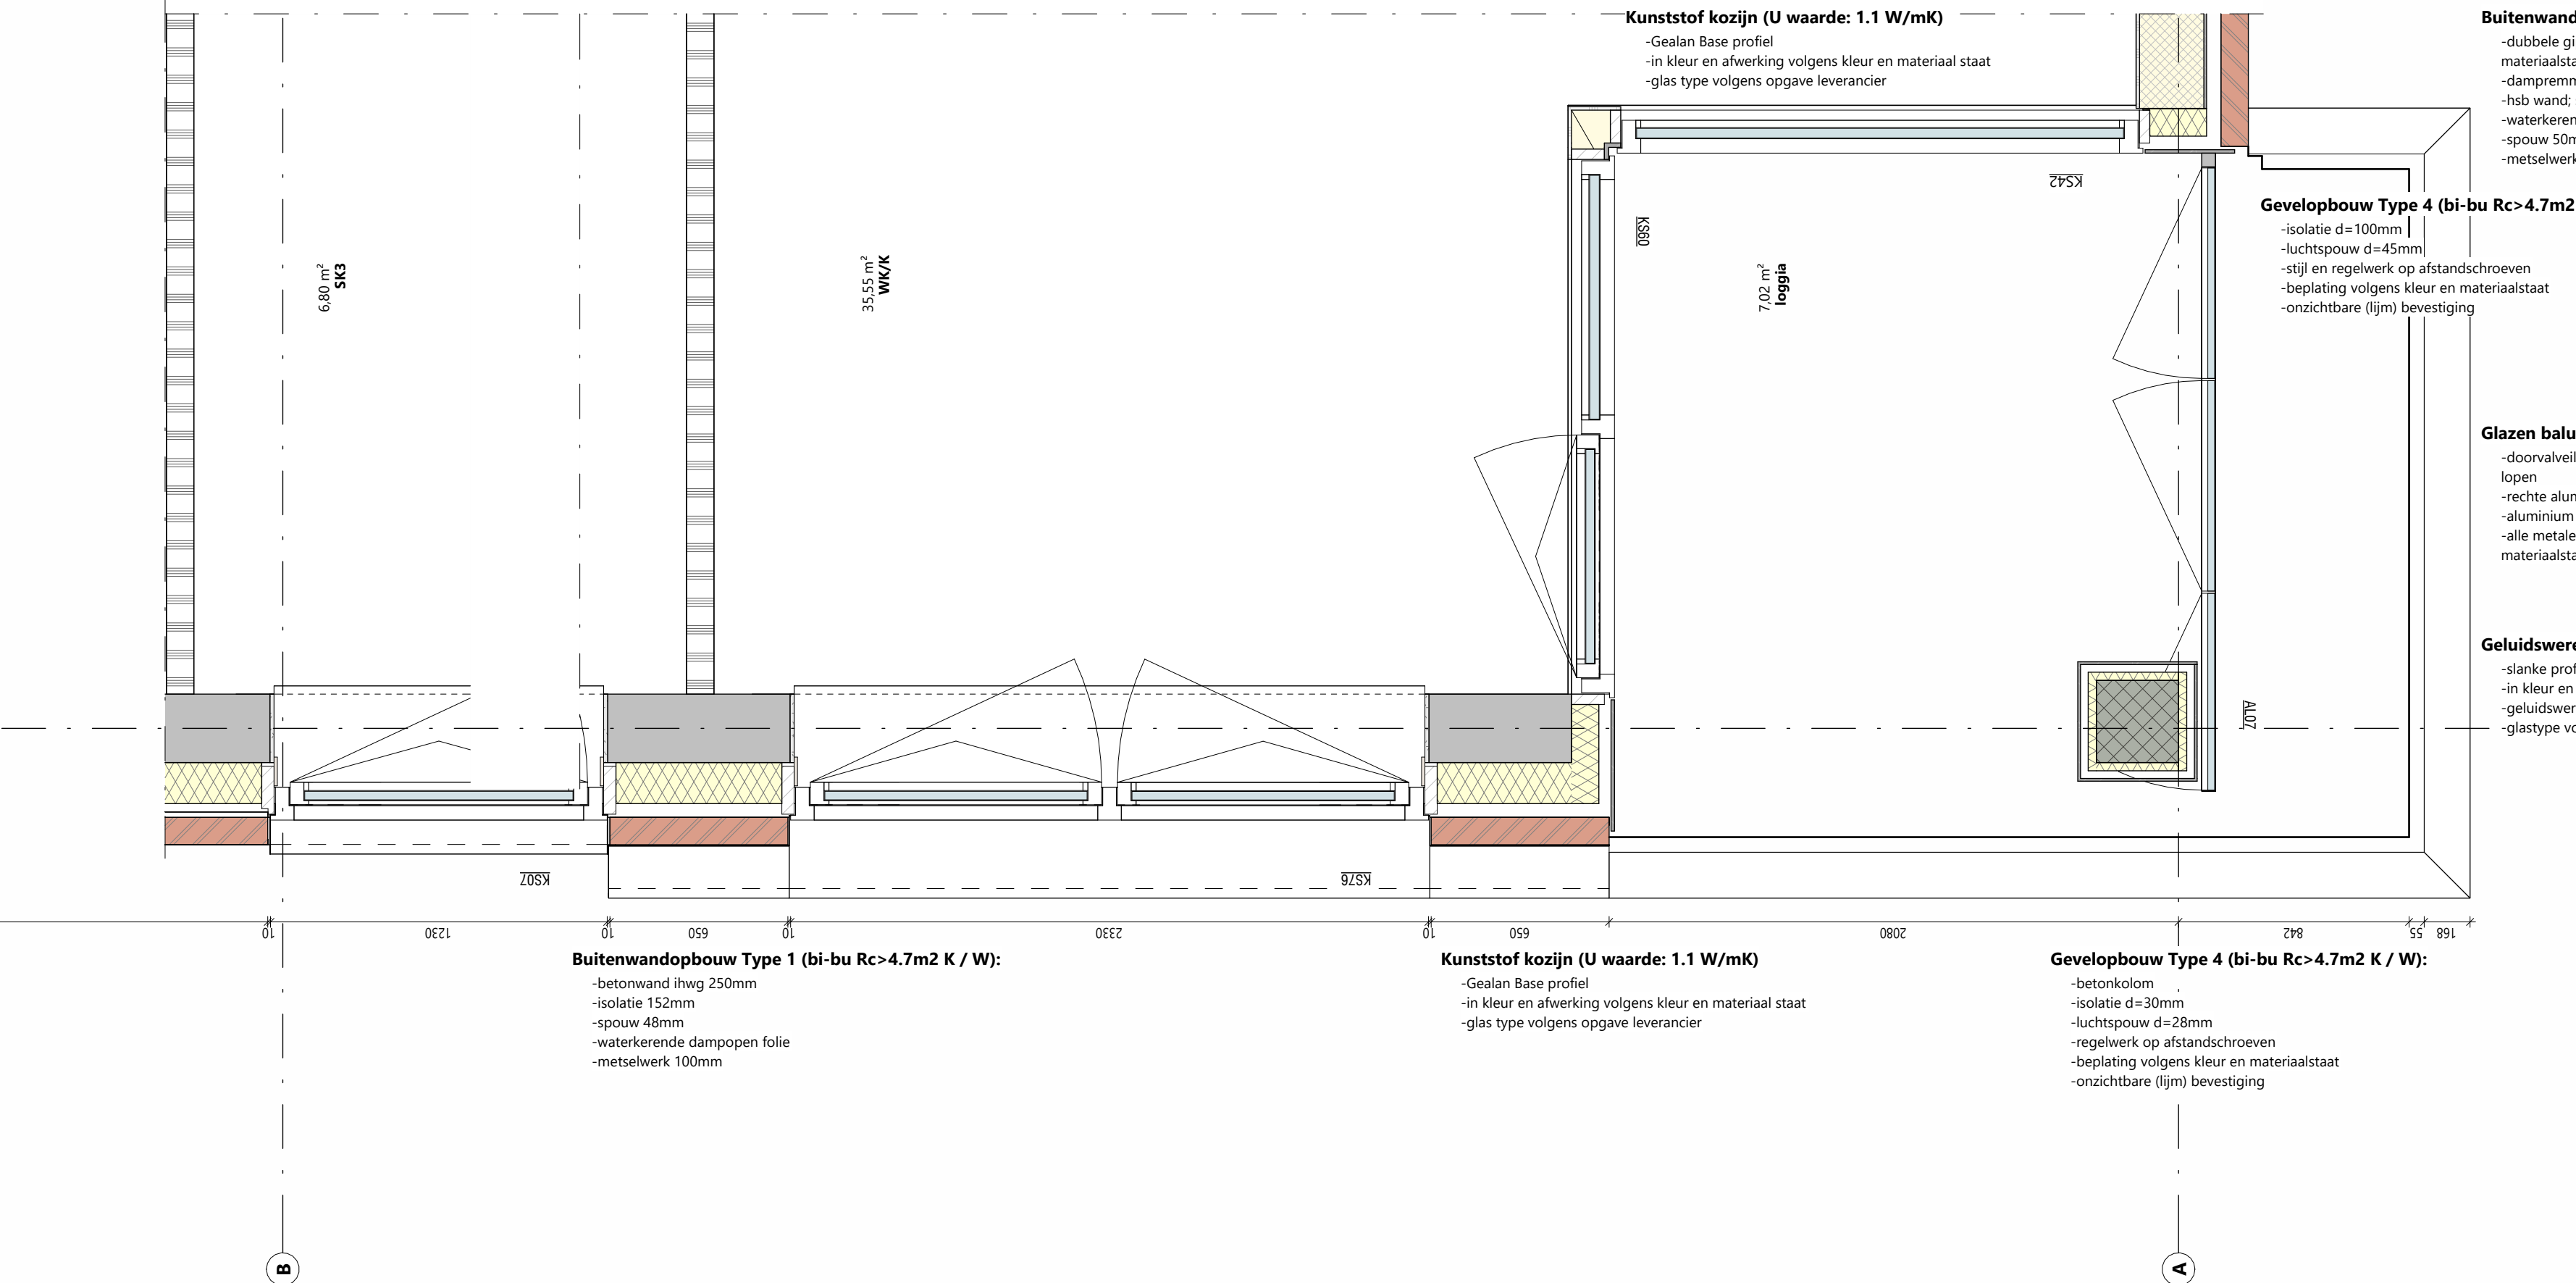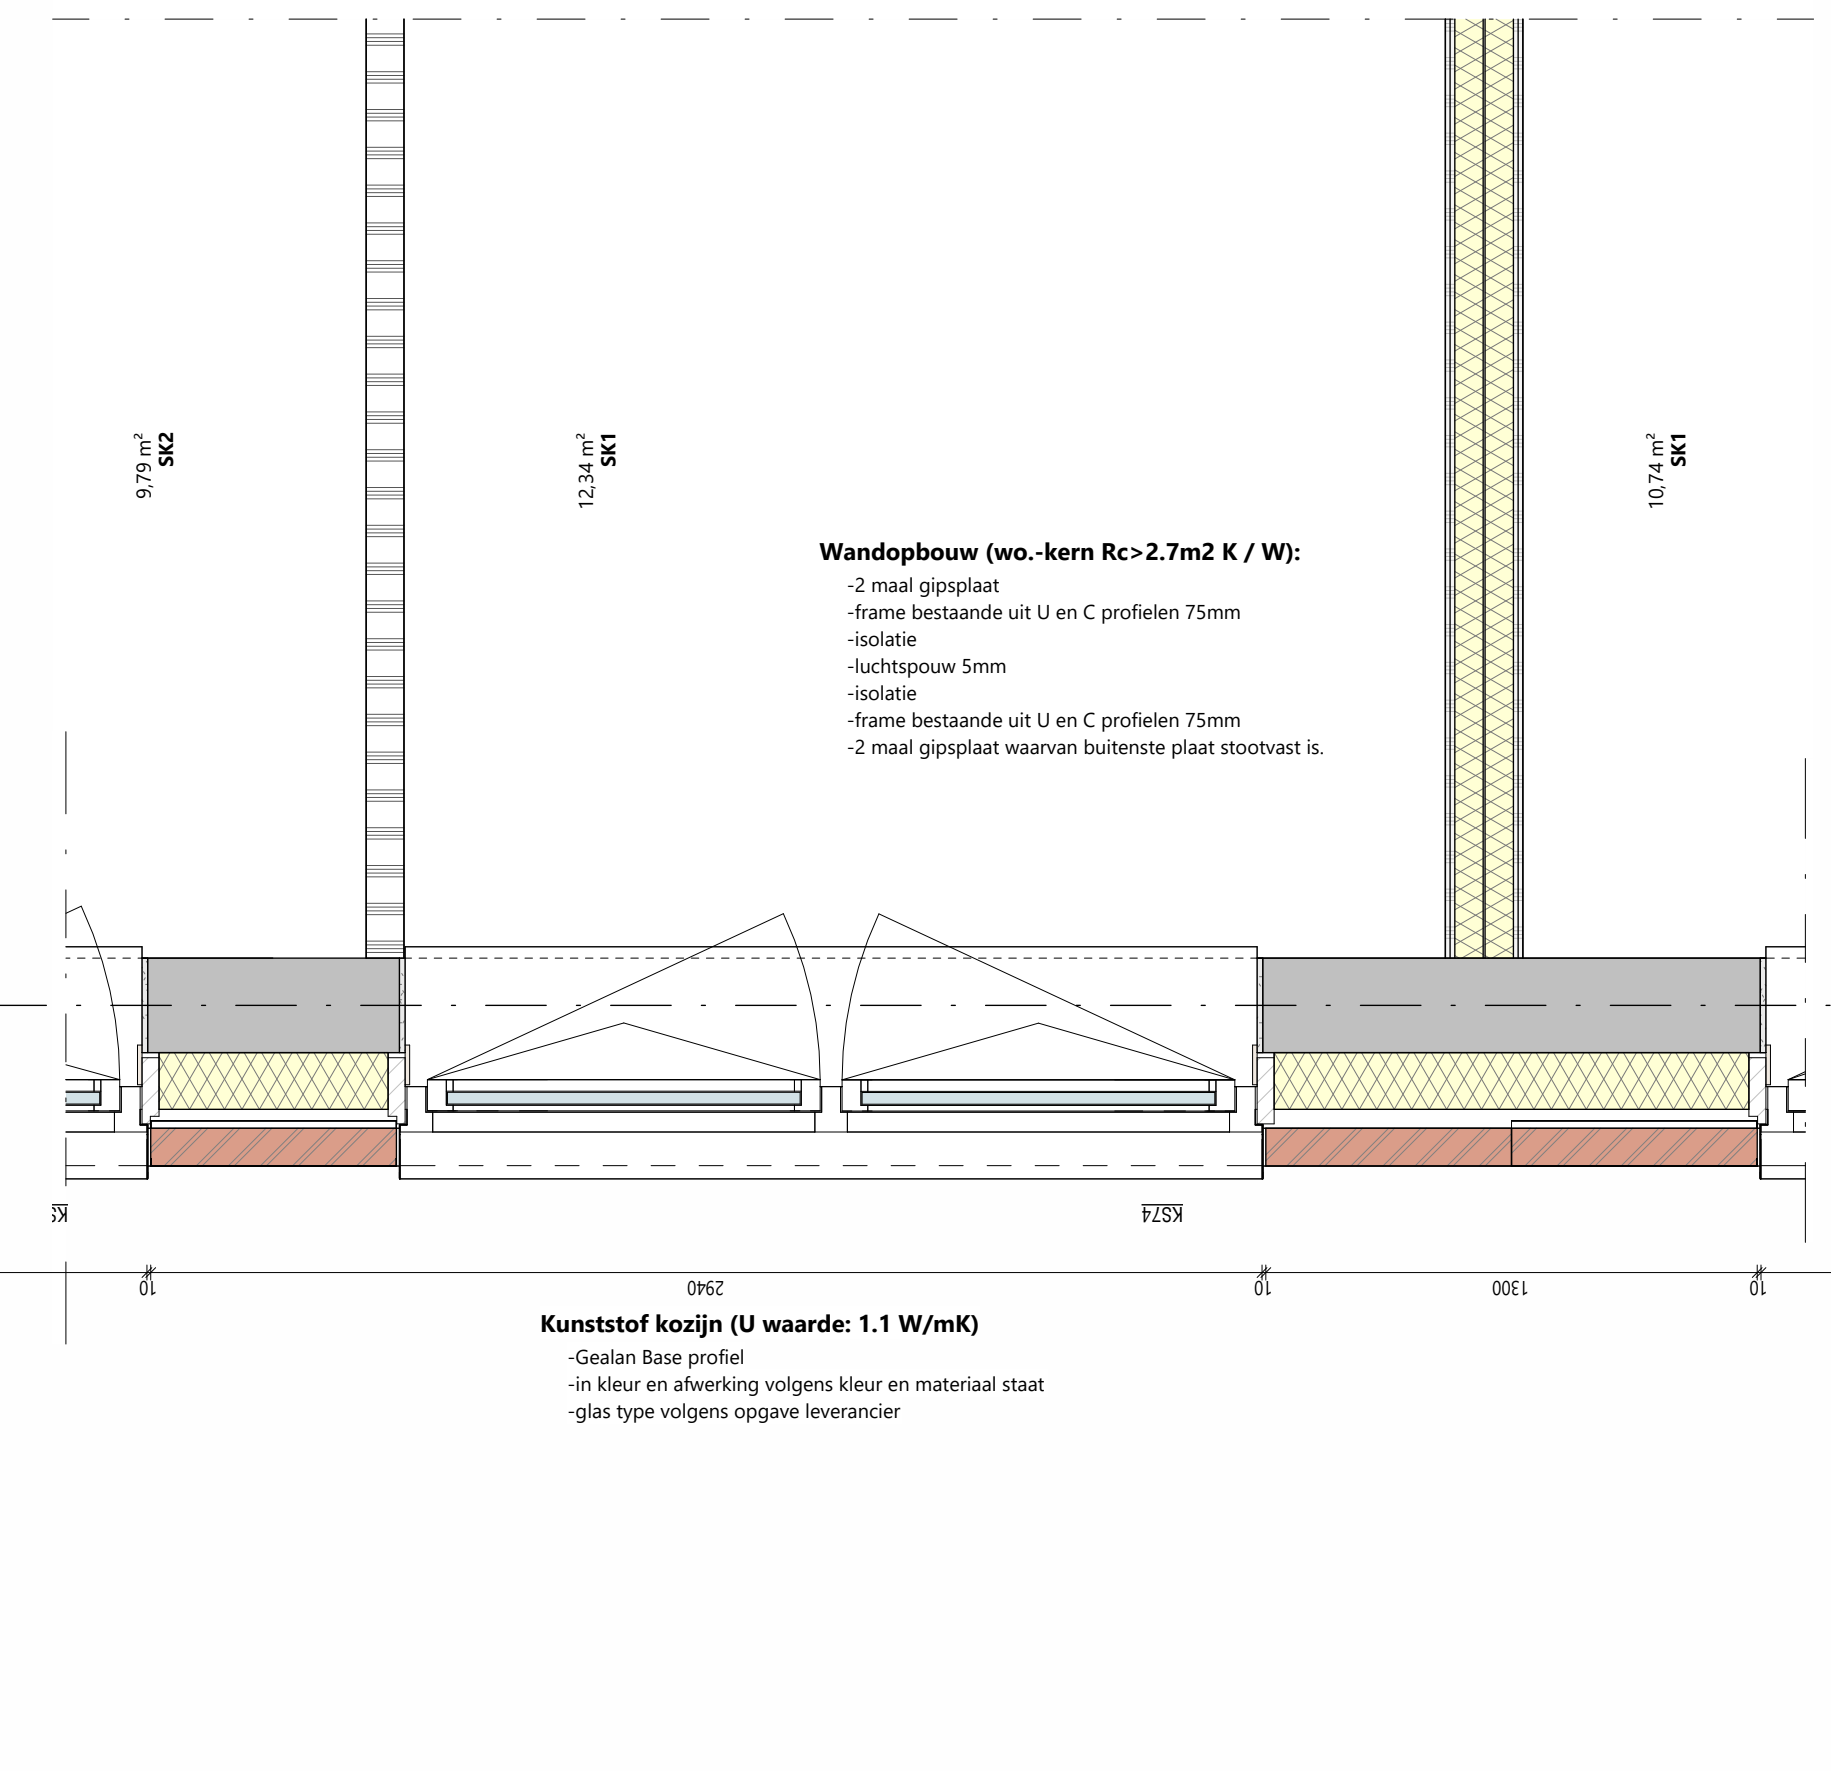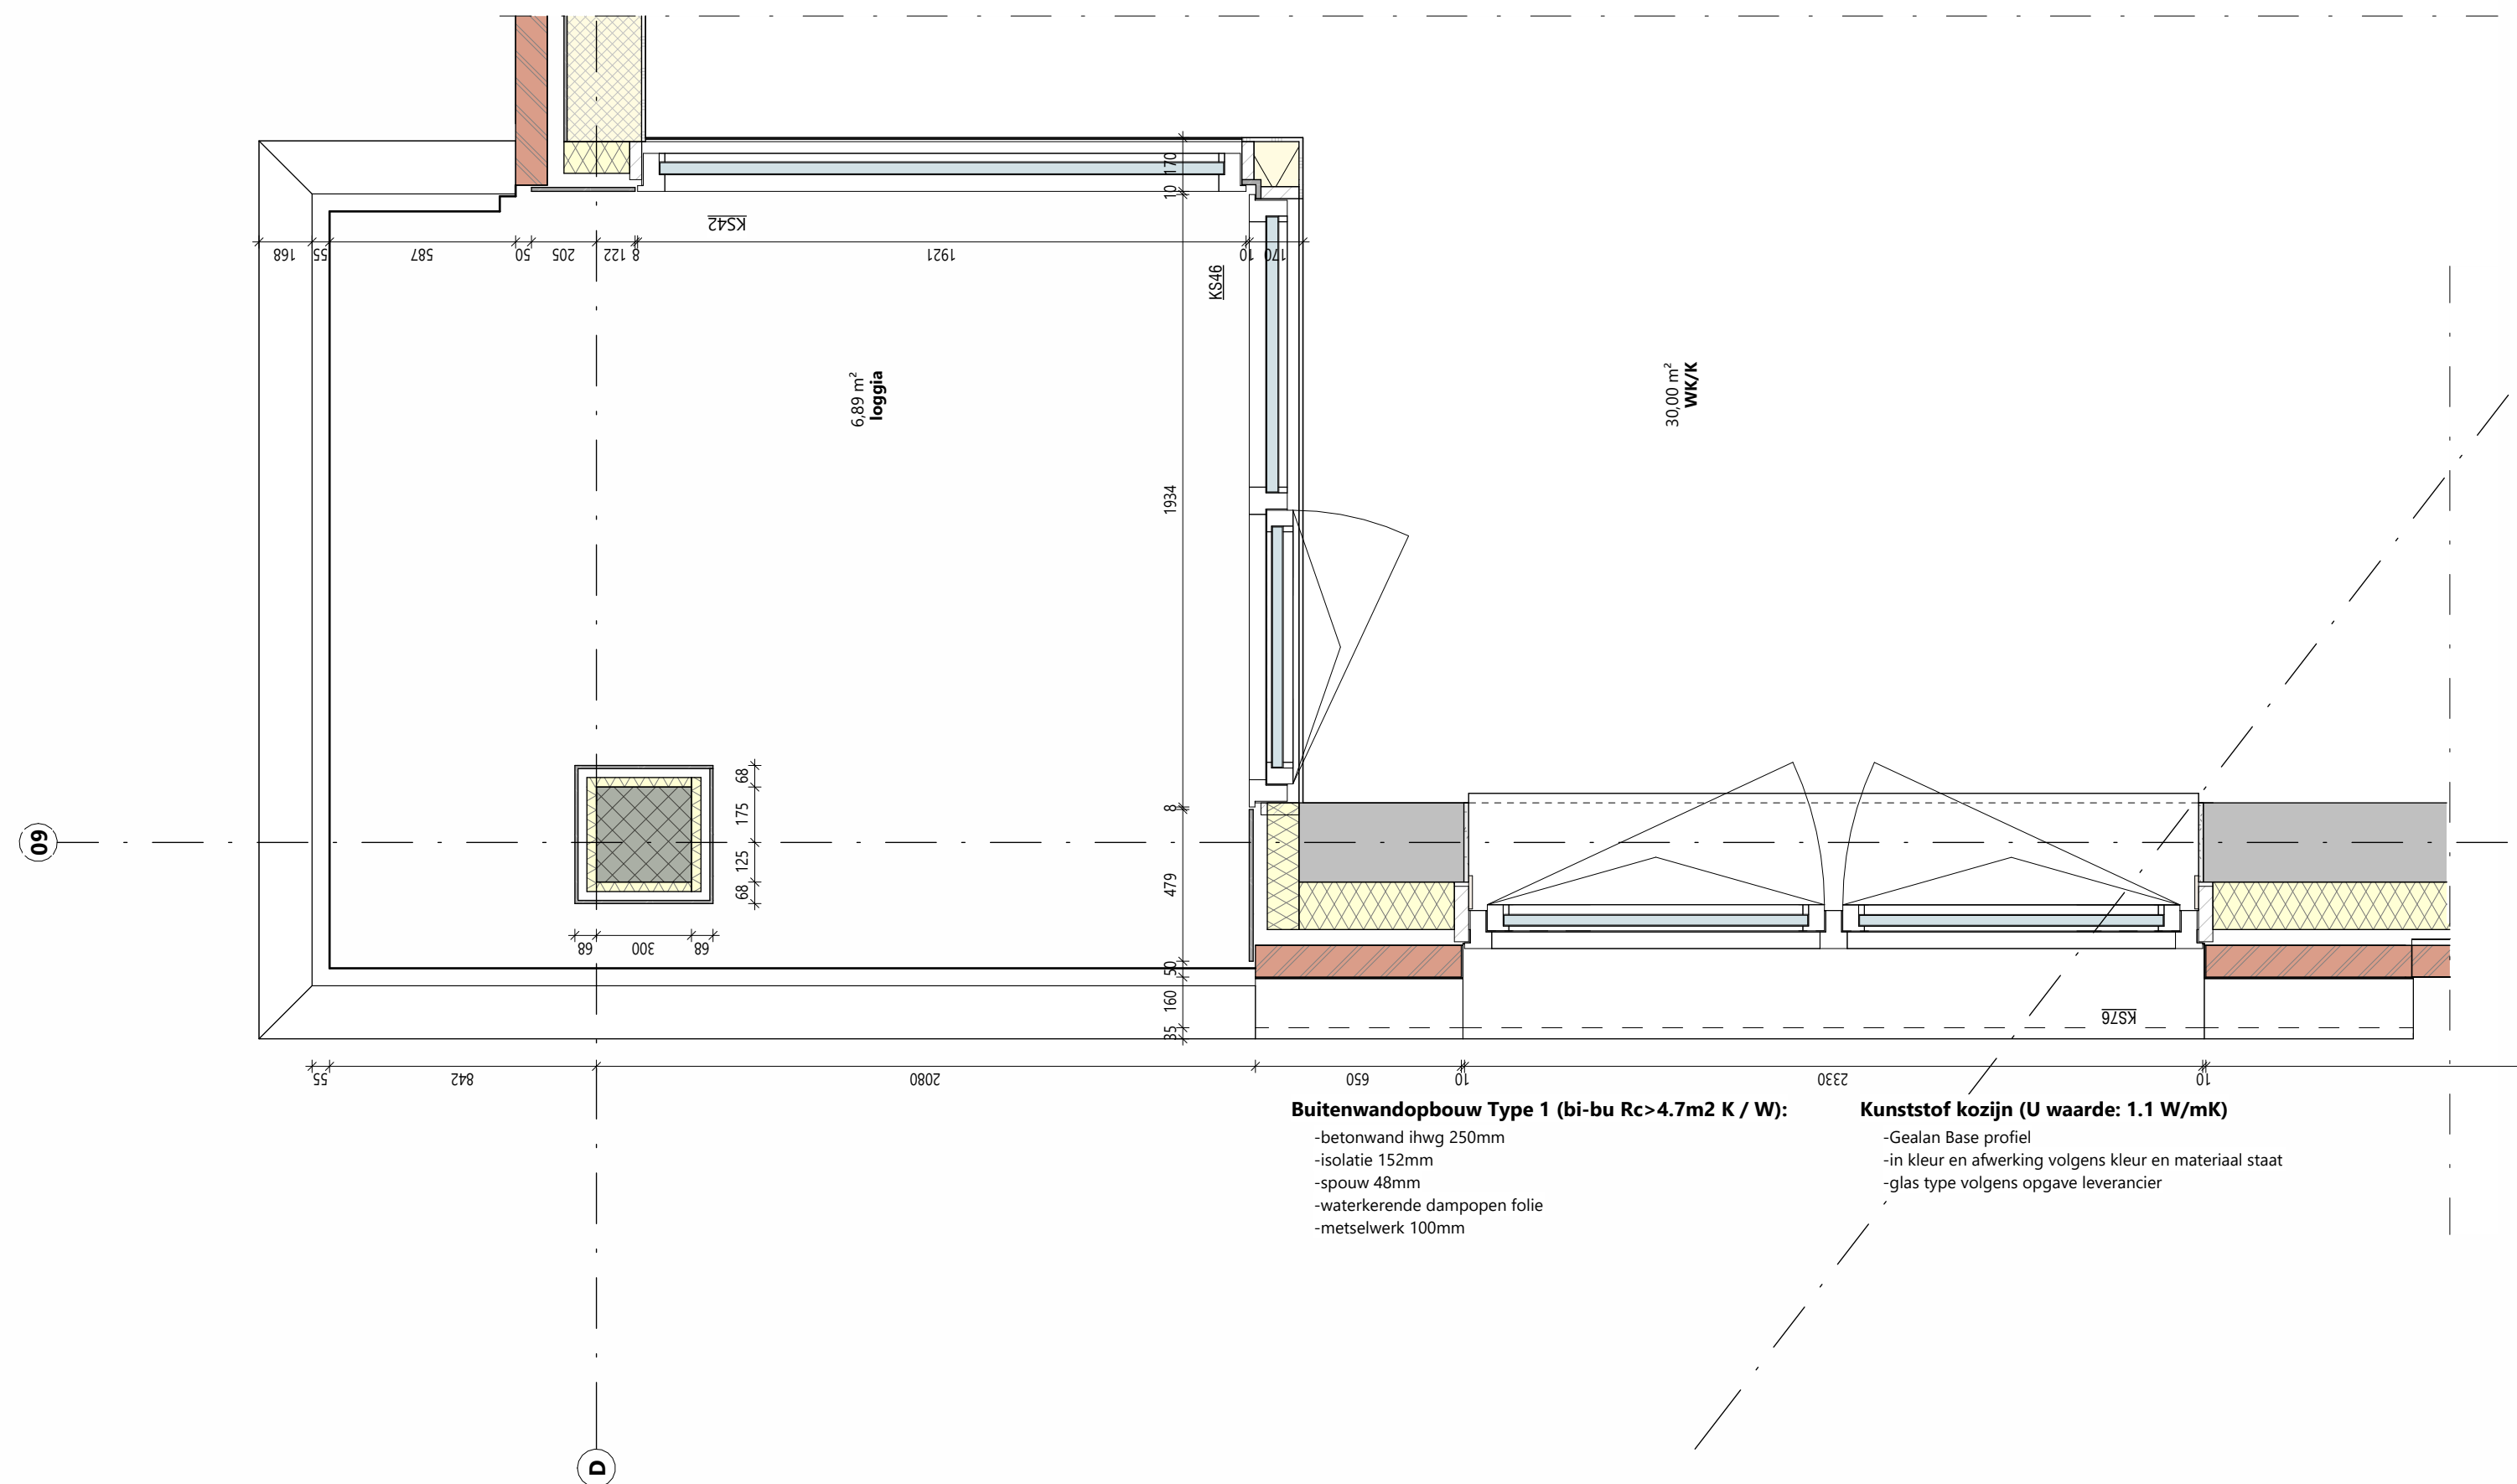

STUDIO
OXs

fragment gev Zuid

Gouda Harderwijkweg
Harderwijkweg 4, Gouda

Opdrachtgever: Create Realstate Raul Godron

Projectnr: 2459
Fase: TO
Auteur: J.Kolthof


Formaat: A0
Schaal: 1:20
1e datum: 10-11-2025
Status: Definitief
Tekeningsnr: TO-509

3bm
Ingenieurs van oplossingen

Tekening ongeschikt voor uitvoeringsfase
Copyright 8-11-2025 17:54:55

Piektstraat 27
3071 EL Rotterdam
+31 (0)6 41 23 22 49
info@studiooxs.com

JBW Bouwkunde
Watstraat 17
3395 LV Zwijndrecht
Tel: 078 7400 258
jochen@jbw.nl
www.jbw.nl

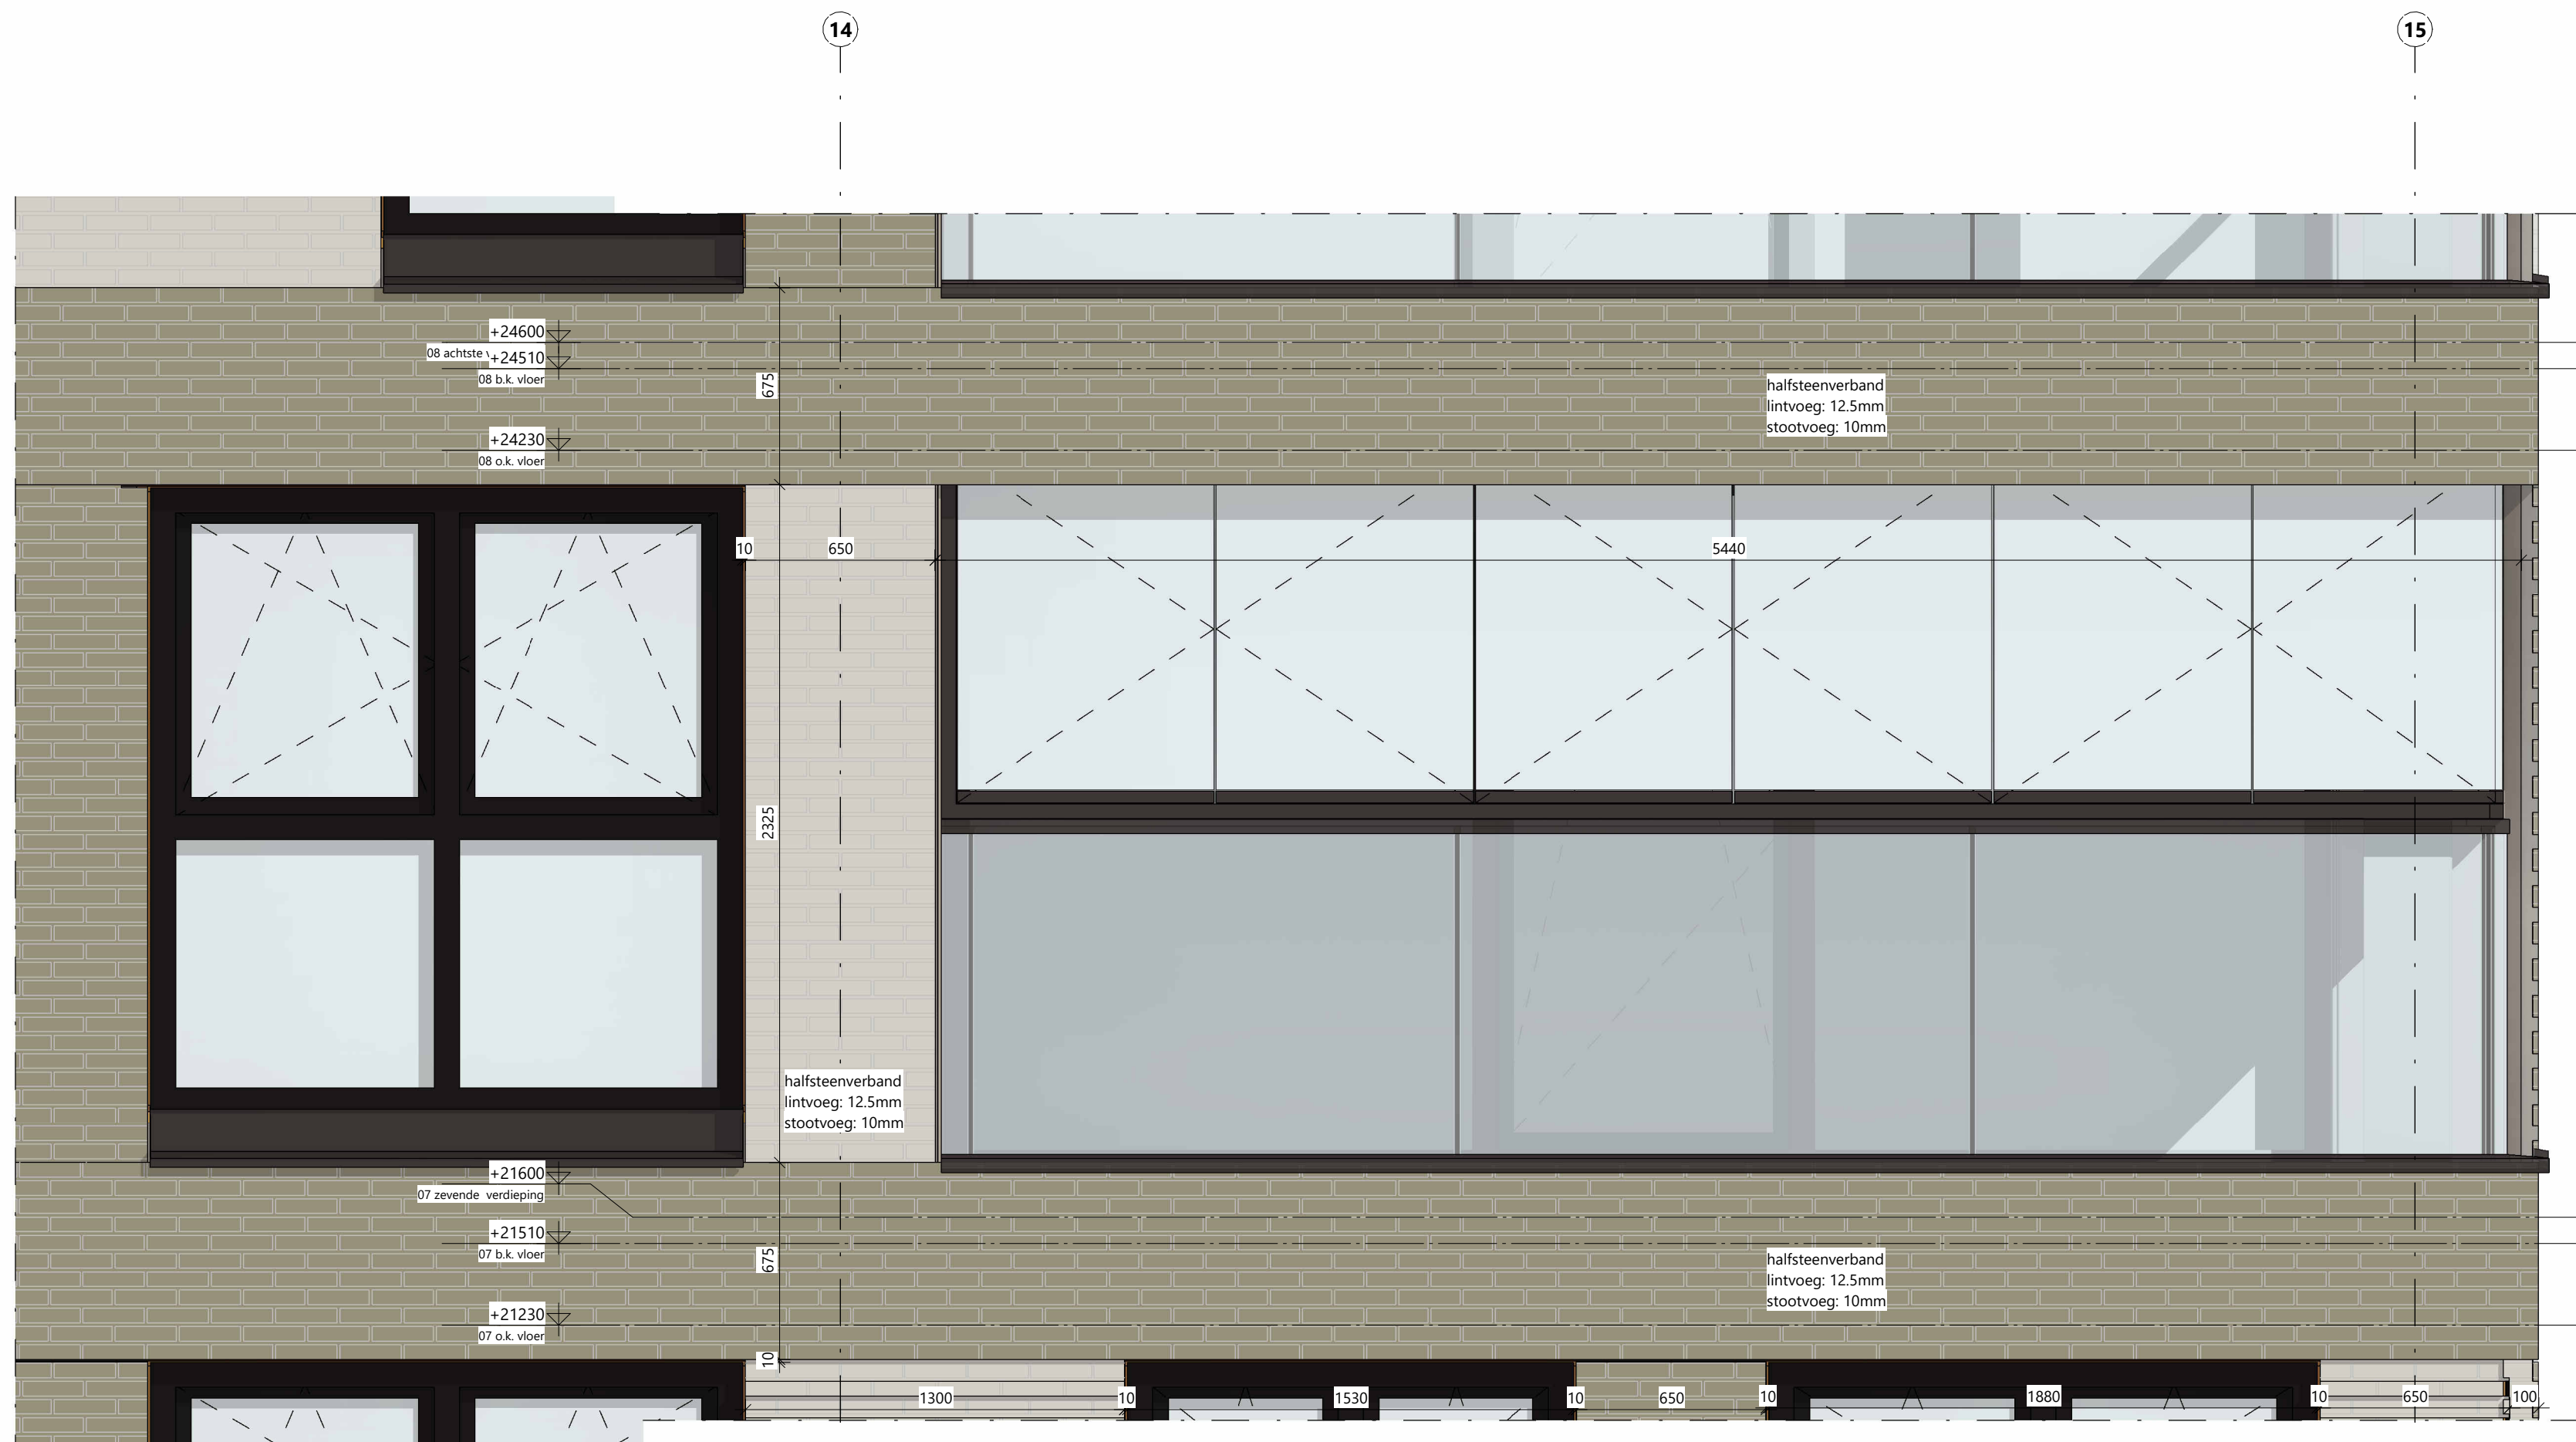

Geluidswerende balkon beglazing:
-slanke profilering n.t.b.
-in kleur en afwerking volgens kleur en materiaal staat
-geluidswerende eigenschappen volgens geluidsrapport
-glastype volgens opgave leverancier

Kunststof kozijn (U waarde: 1.1 W/mK)
-Gealan Base profiel
-in kleur en afwerking volgens kleur en materiaal staat
-glas type volgens opgave leverancier




Buitenwandopbouw Type 2 (bi-bu Rc>4.7m2 K / W):
-dubbele gipsplaat 12.5mm. afwerking volgens kleur en materiaalstaat
-dampremmende folie
-hwb wand; stijl en regelwerk 235mm,
-waterkerende, dampoppn folie
-spouw 50mm
-metselwerk 100mm

Kunststof kozijn (U waarde: 1.1 W/mK)
-Gealan Base profiel
-in kleur en afwerking volgens kleur en materiaal staat
-glas type volgens opgave leverancier

Wandopbouw (wo.-kern Rc>2.7m2 K / W):
-2 maal gipsplaat
-frame bestaande uit U en C profielen 75mm
-isolatie
-luchtsponw 5mm
-isolatie
-frame bestaande uit U en C profielen 75mm
-2 maal gipsplaat waarvan buitenste plaat stootvast is.

Kunststof kozijn (U waarde: 1.1 W/mK)
-Gealan Base profiel
-in kleur en afwerking volgens kleur en materiaal staat
-glas type volgens opgave leverancier

Geluidswerende balkon beglazing:
-slanke profilering n.t.b.
-in kleur en afwerking volgens kleur en materiaal staat
-geluidswerende eigenschappen volgens geluidsrapport
-glastype volgens opgave leverancier

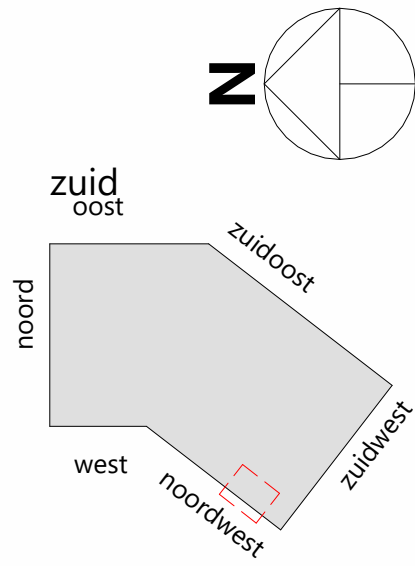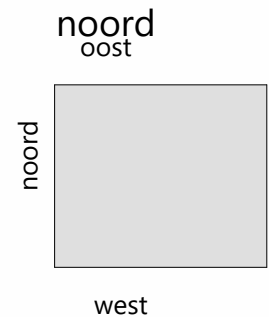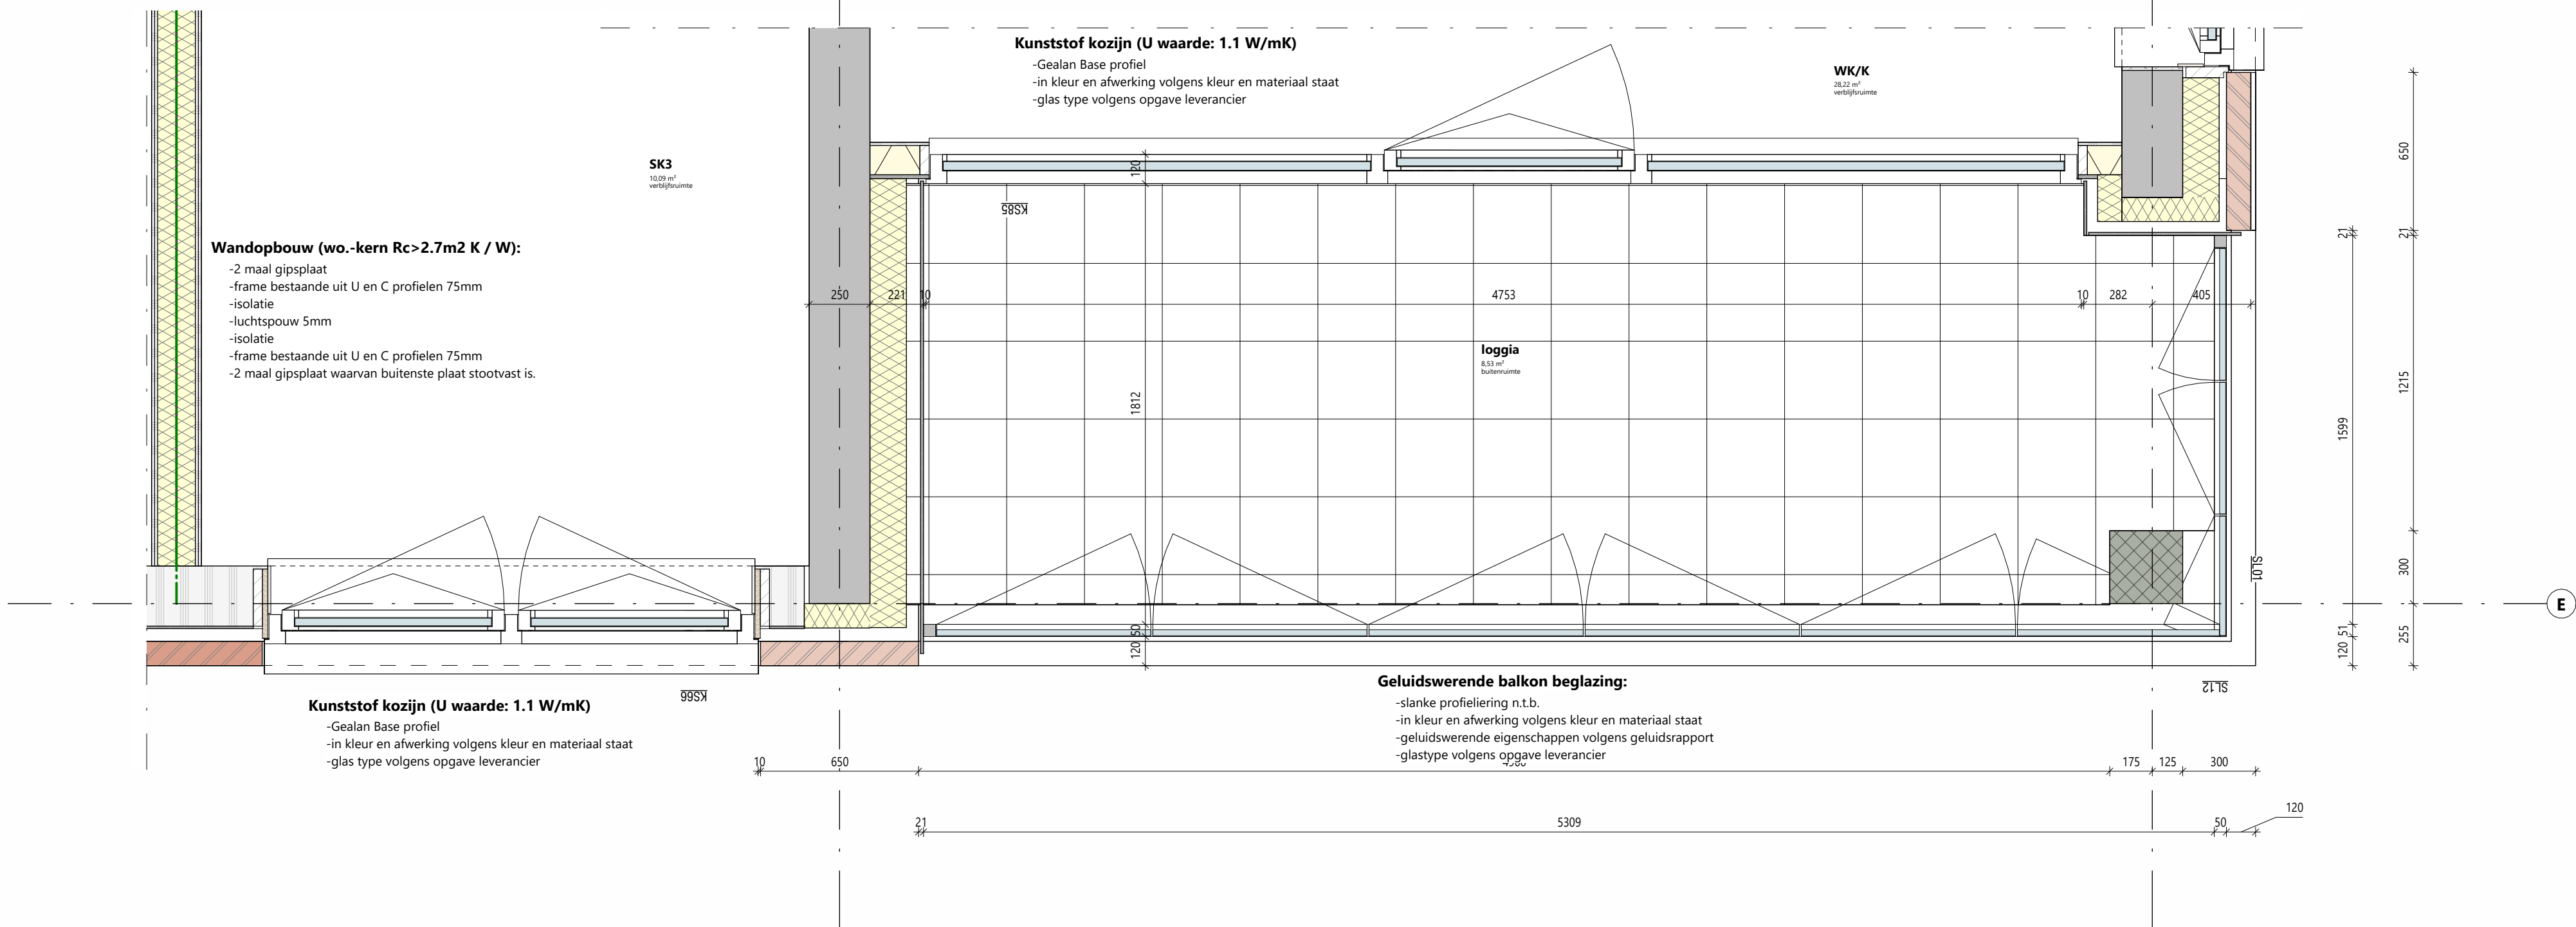

STUDIO
OXs

fragment gev zuid

Gouda Harderwijkweg
Harderwijkweg 4, Gouda

Opdrachtgever: Create Realstate Raul Godron

Projectnr: 2459
Fase: TO
Auteur: JKolthof
Formaat: A1
Schaal: 1:20
1^e datum: 10-11-2025
Status: Definitief
Tekeningnr: TO-510



3bm
Ingenieurs van oplossingen

Tekening ongeschikt voor uitvoeringsfase
Geprint 8-11-2025 17:55:01

Piekstraat 27
3071 EL Rotterdam
+31 (0)6 41 23 22 49
info@studiooxs.com

3BM Bouwkunde
Wattstraat 17
3335 LV Zwijndrecht
Tel: 078 7400 258
jochem@3bm.co.nl
www.3bm.co.nl



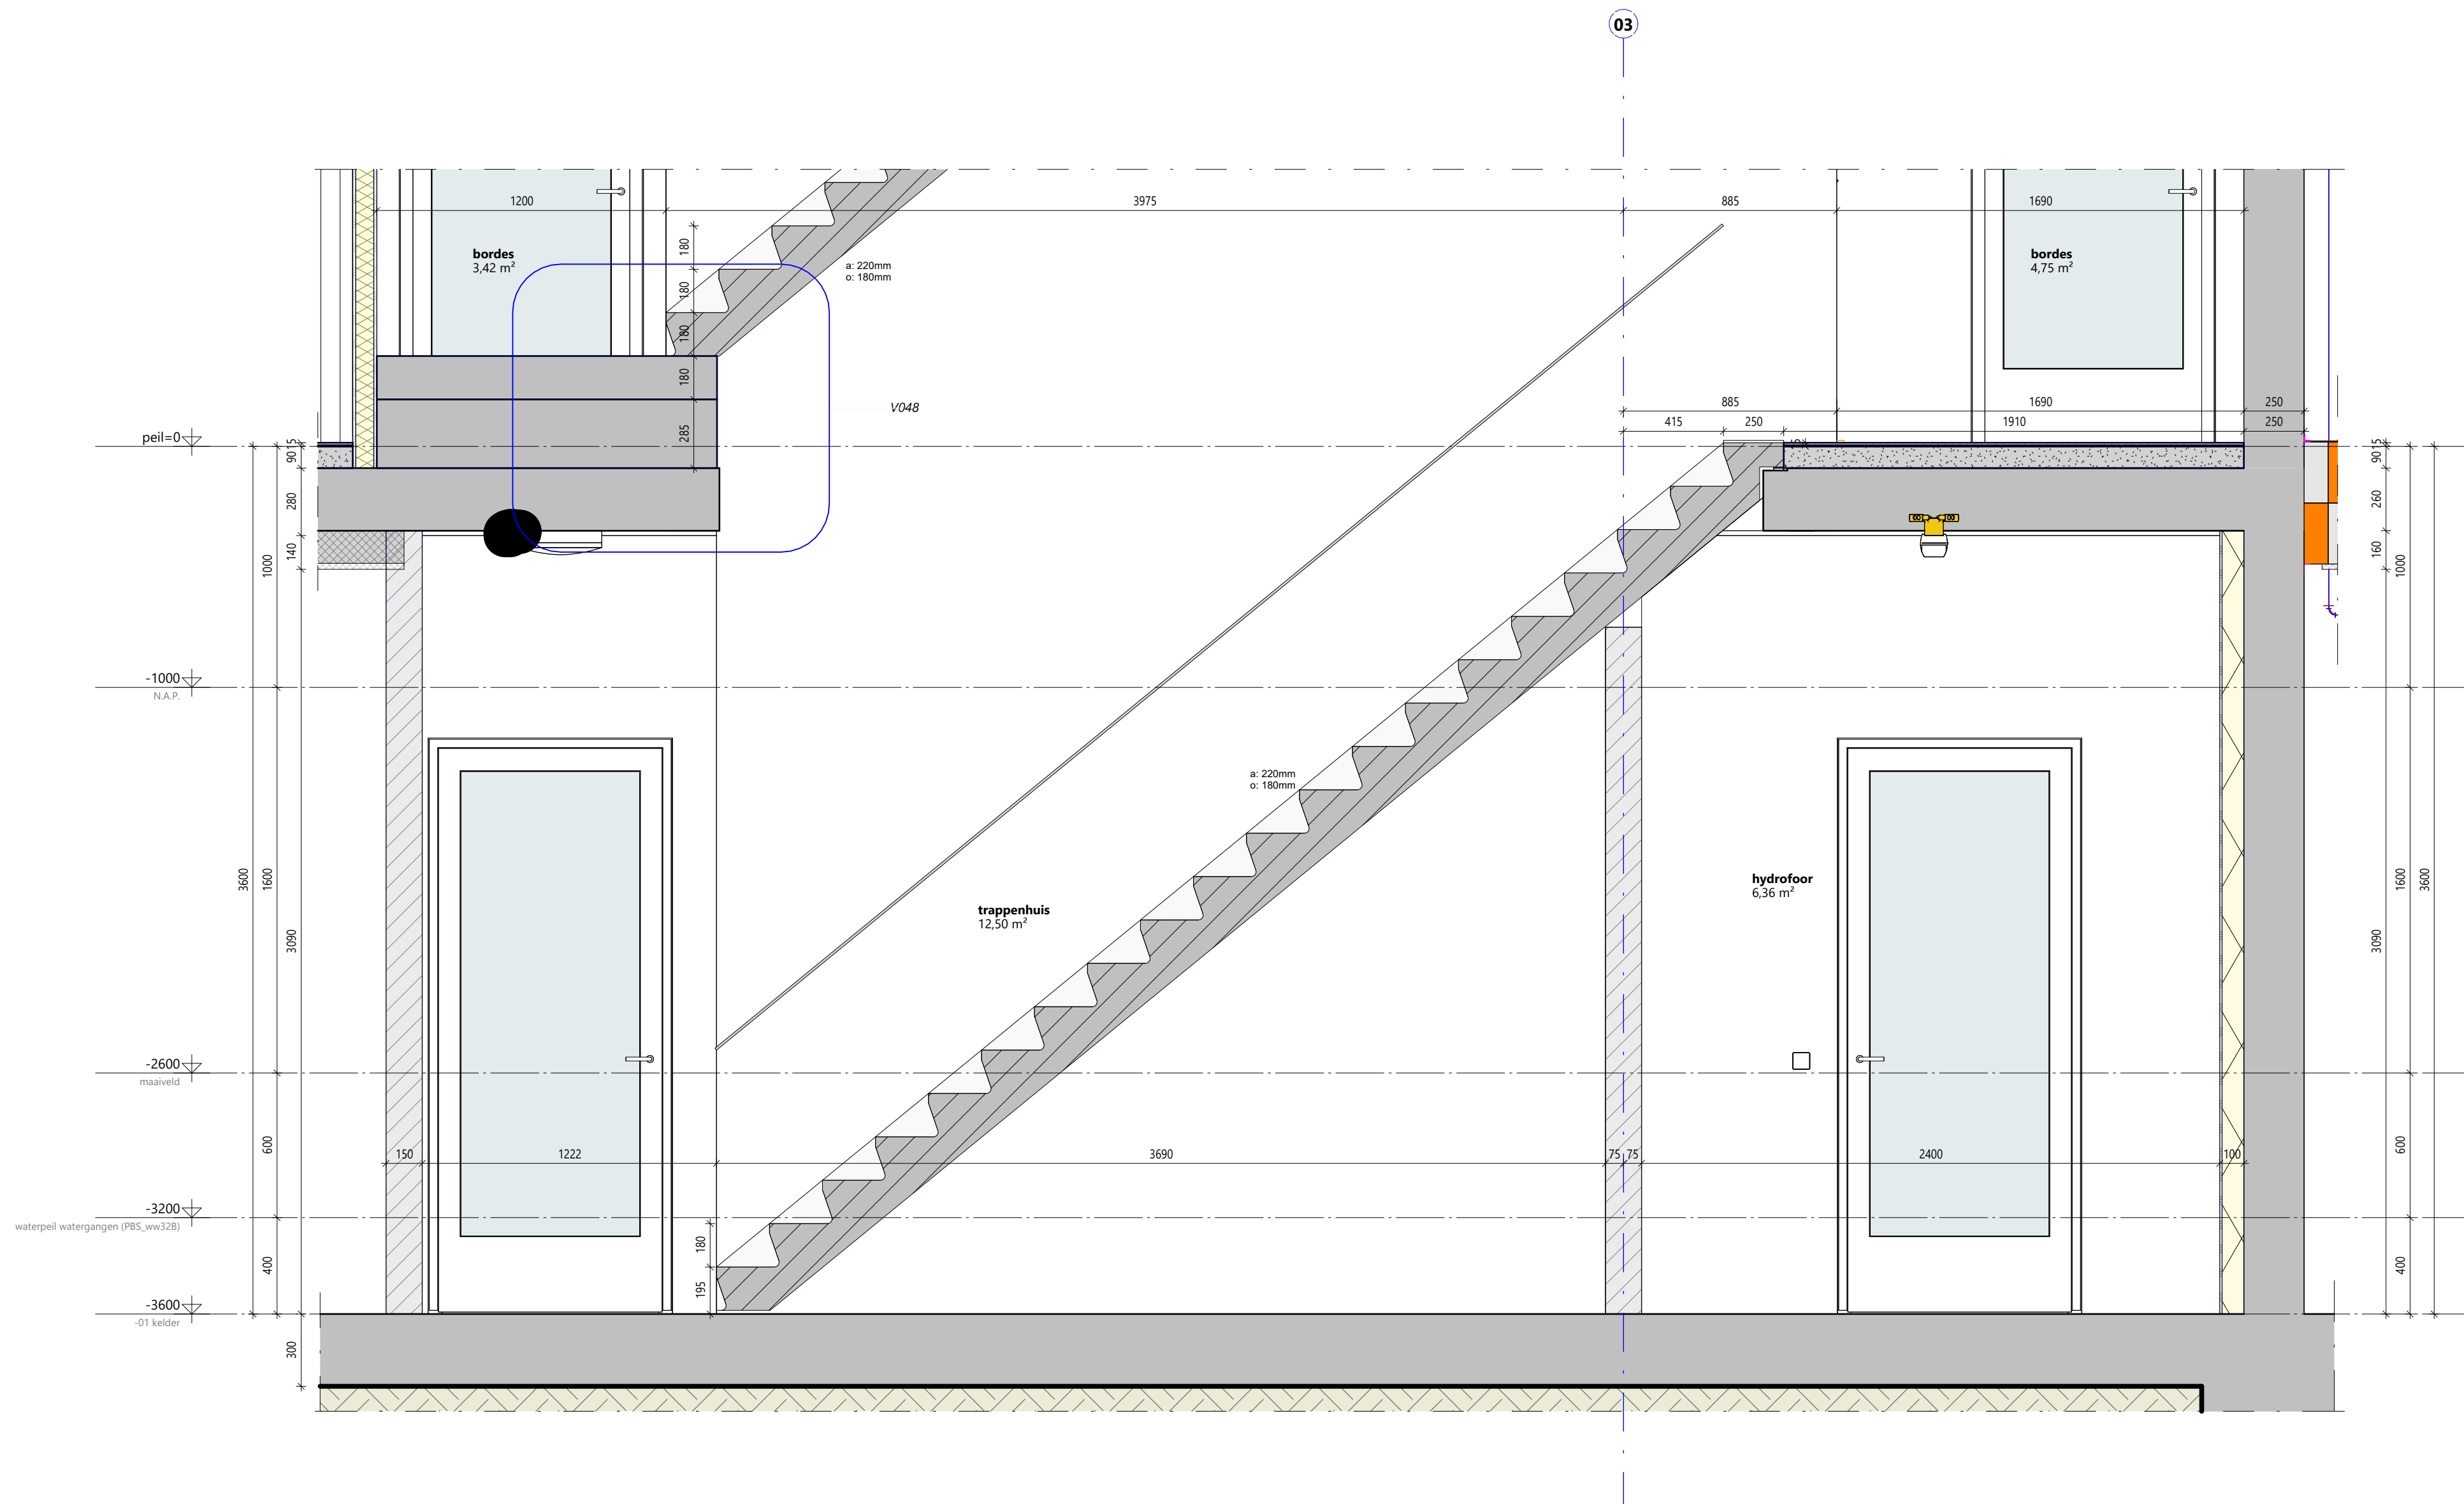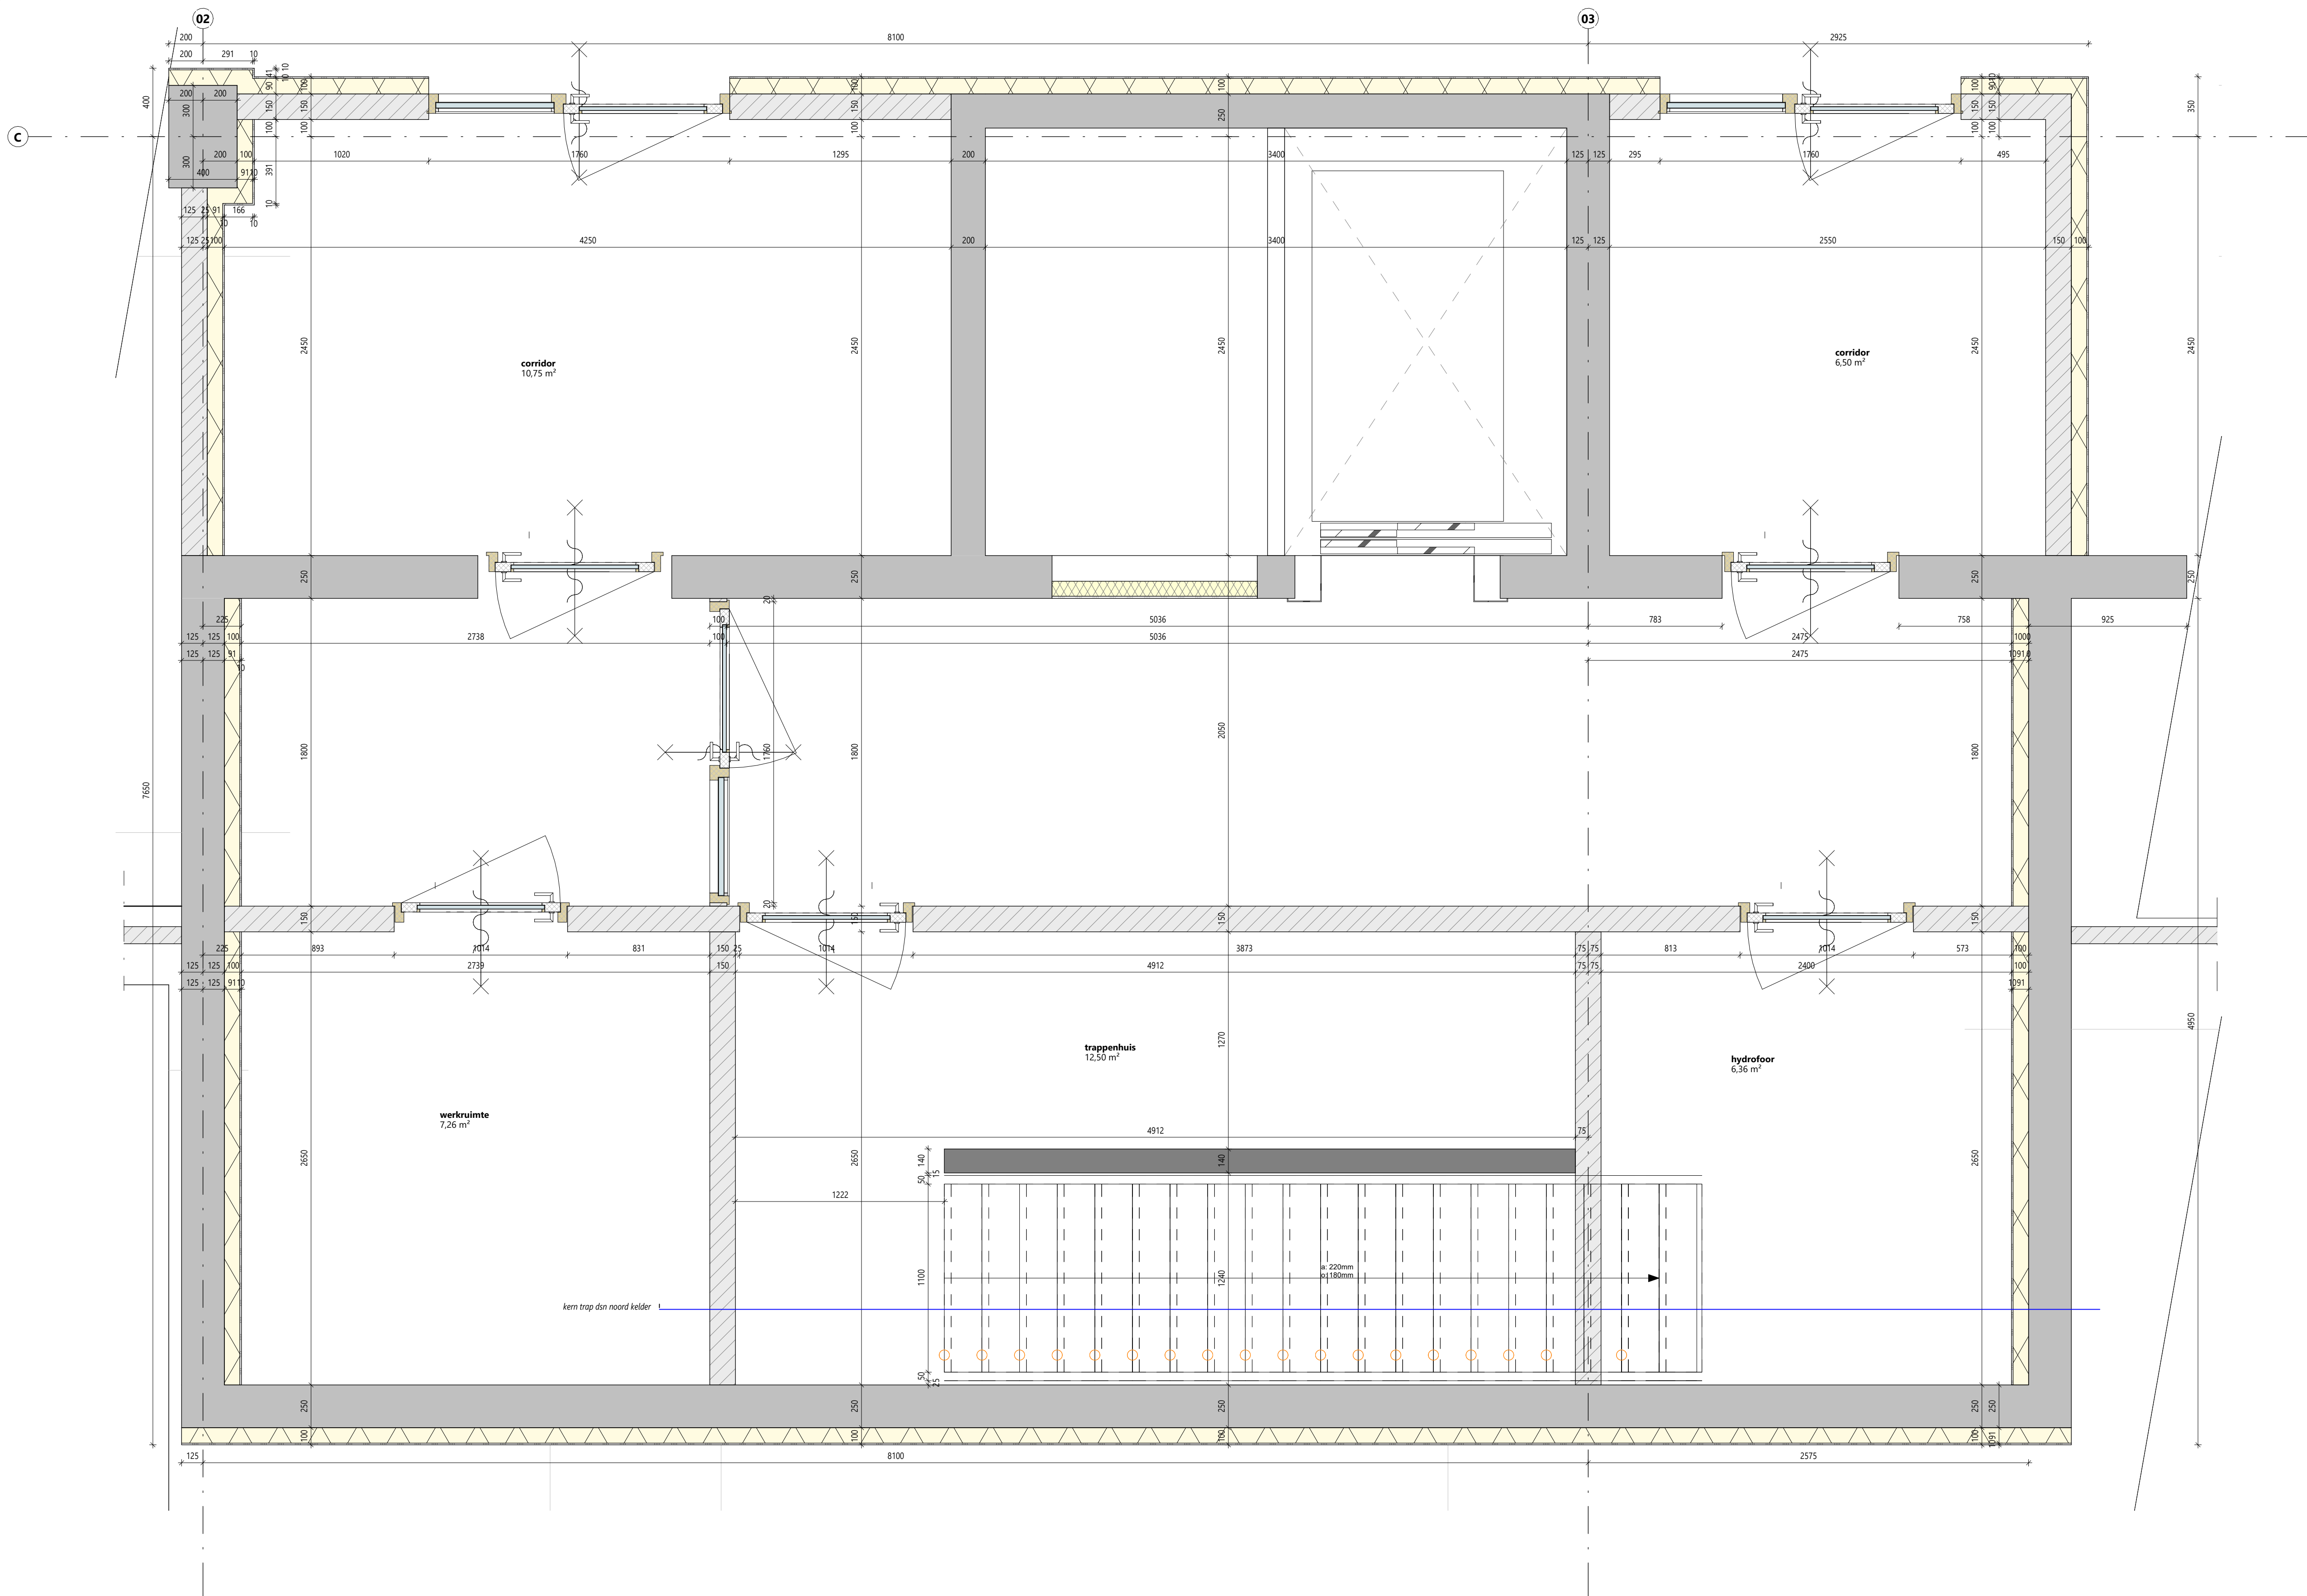

STUDIO
OXs

fragment kern noord kelder

Gouda Harderwijkweg
Harderwijkweg 4, Gouda

Opdrachtgever: Create Realstate Raul Godron

Projectnr: 2459
Fase: TO
Auteur: J.Kalthof

Formaat: A0
Schale: 1:20
1e datum: 10-11-2025
Status: Definitief
Tekeningsnr: TO-S11

Tekening ongeschikt voor uitvoeringsfase
Geprikt 8-11-2025 17:55:03
Ploeg: Architect: StudioOXs Architect: Gouda KOS/PWS, TO, BAK, OOS, etc.

3bm
Ingenieurs van oplossingen

Piekstraat 27
3071 EL Rotterdam
+31 (0)6 41 23 22 49
info@studiooxs.com

3BM Bouwkunde
Watersstraat 17
3335 LV Zoetermeer
Tel: 078 7600 256
jochem@3bm.co.nl
www.3bm.co.nl







Tekening ongeschikt voor uitvoeringsfase
Geprint 8-11-2025 17:55:05
Pad: Autodesk Docs\\2504 Parkway - Goeda K25/PVG 10_BWK_0

3BM Bouwkunde
Wettstraat 17
3335 LV Zwijndrecht
Tel: 078 7400 258
jochem@3bm.co.nl
www.3bm.co.nl



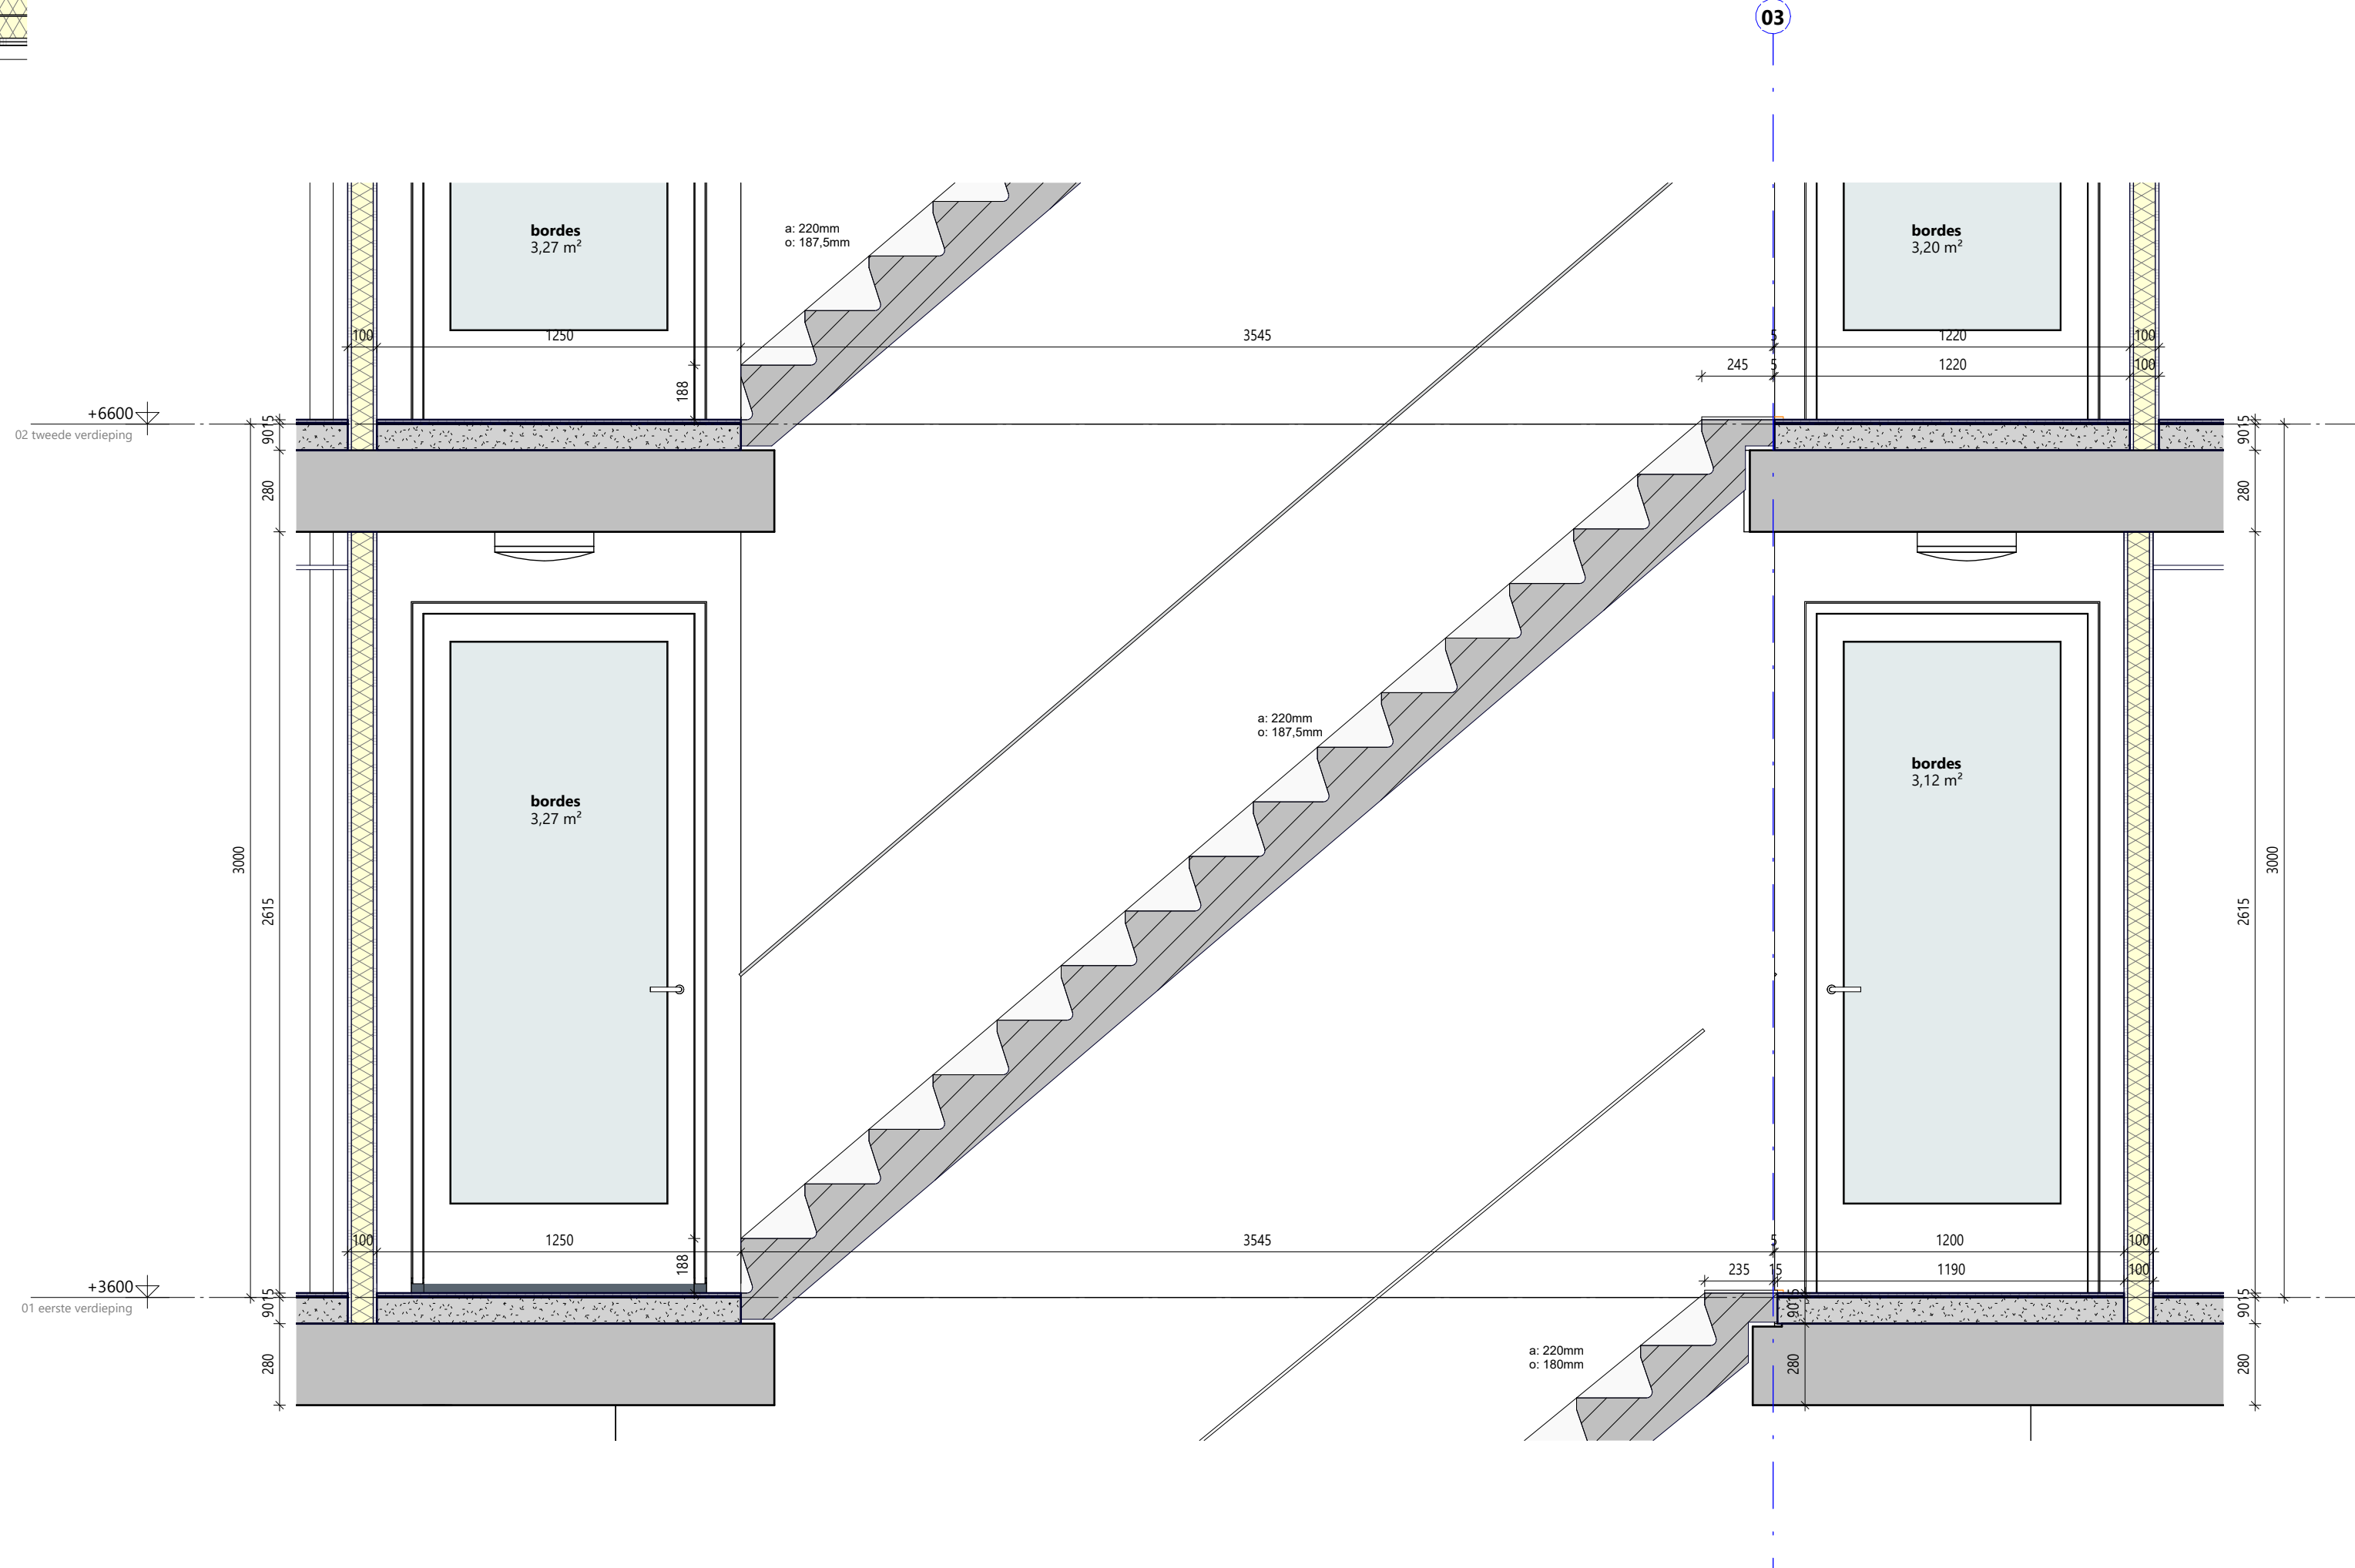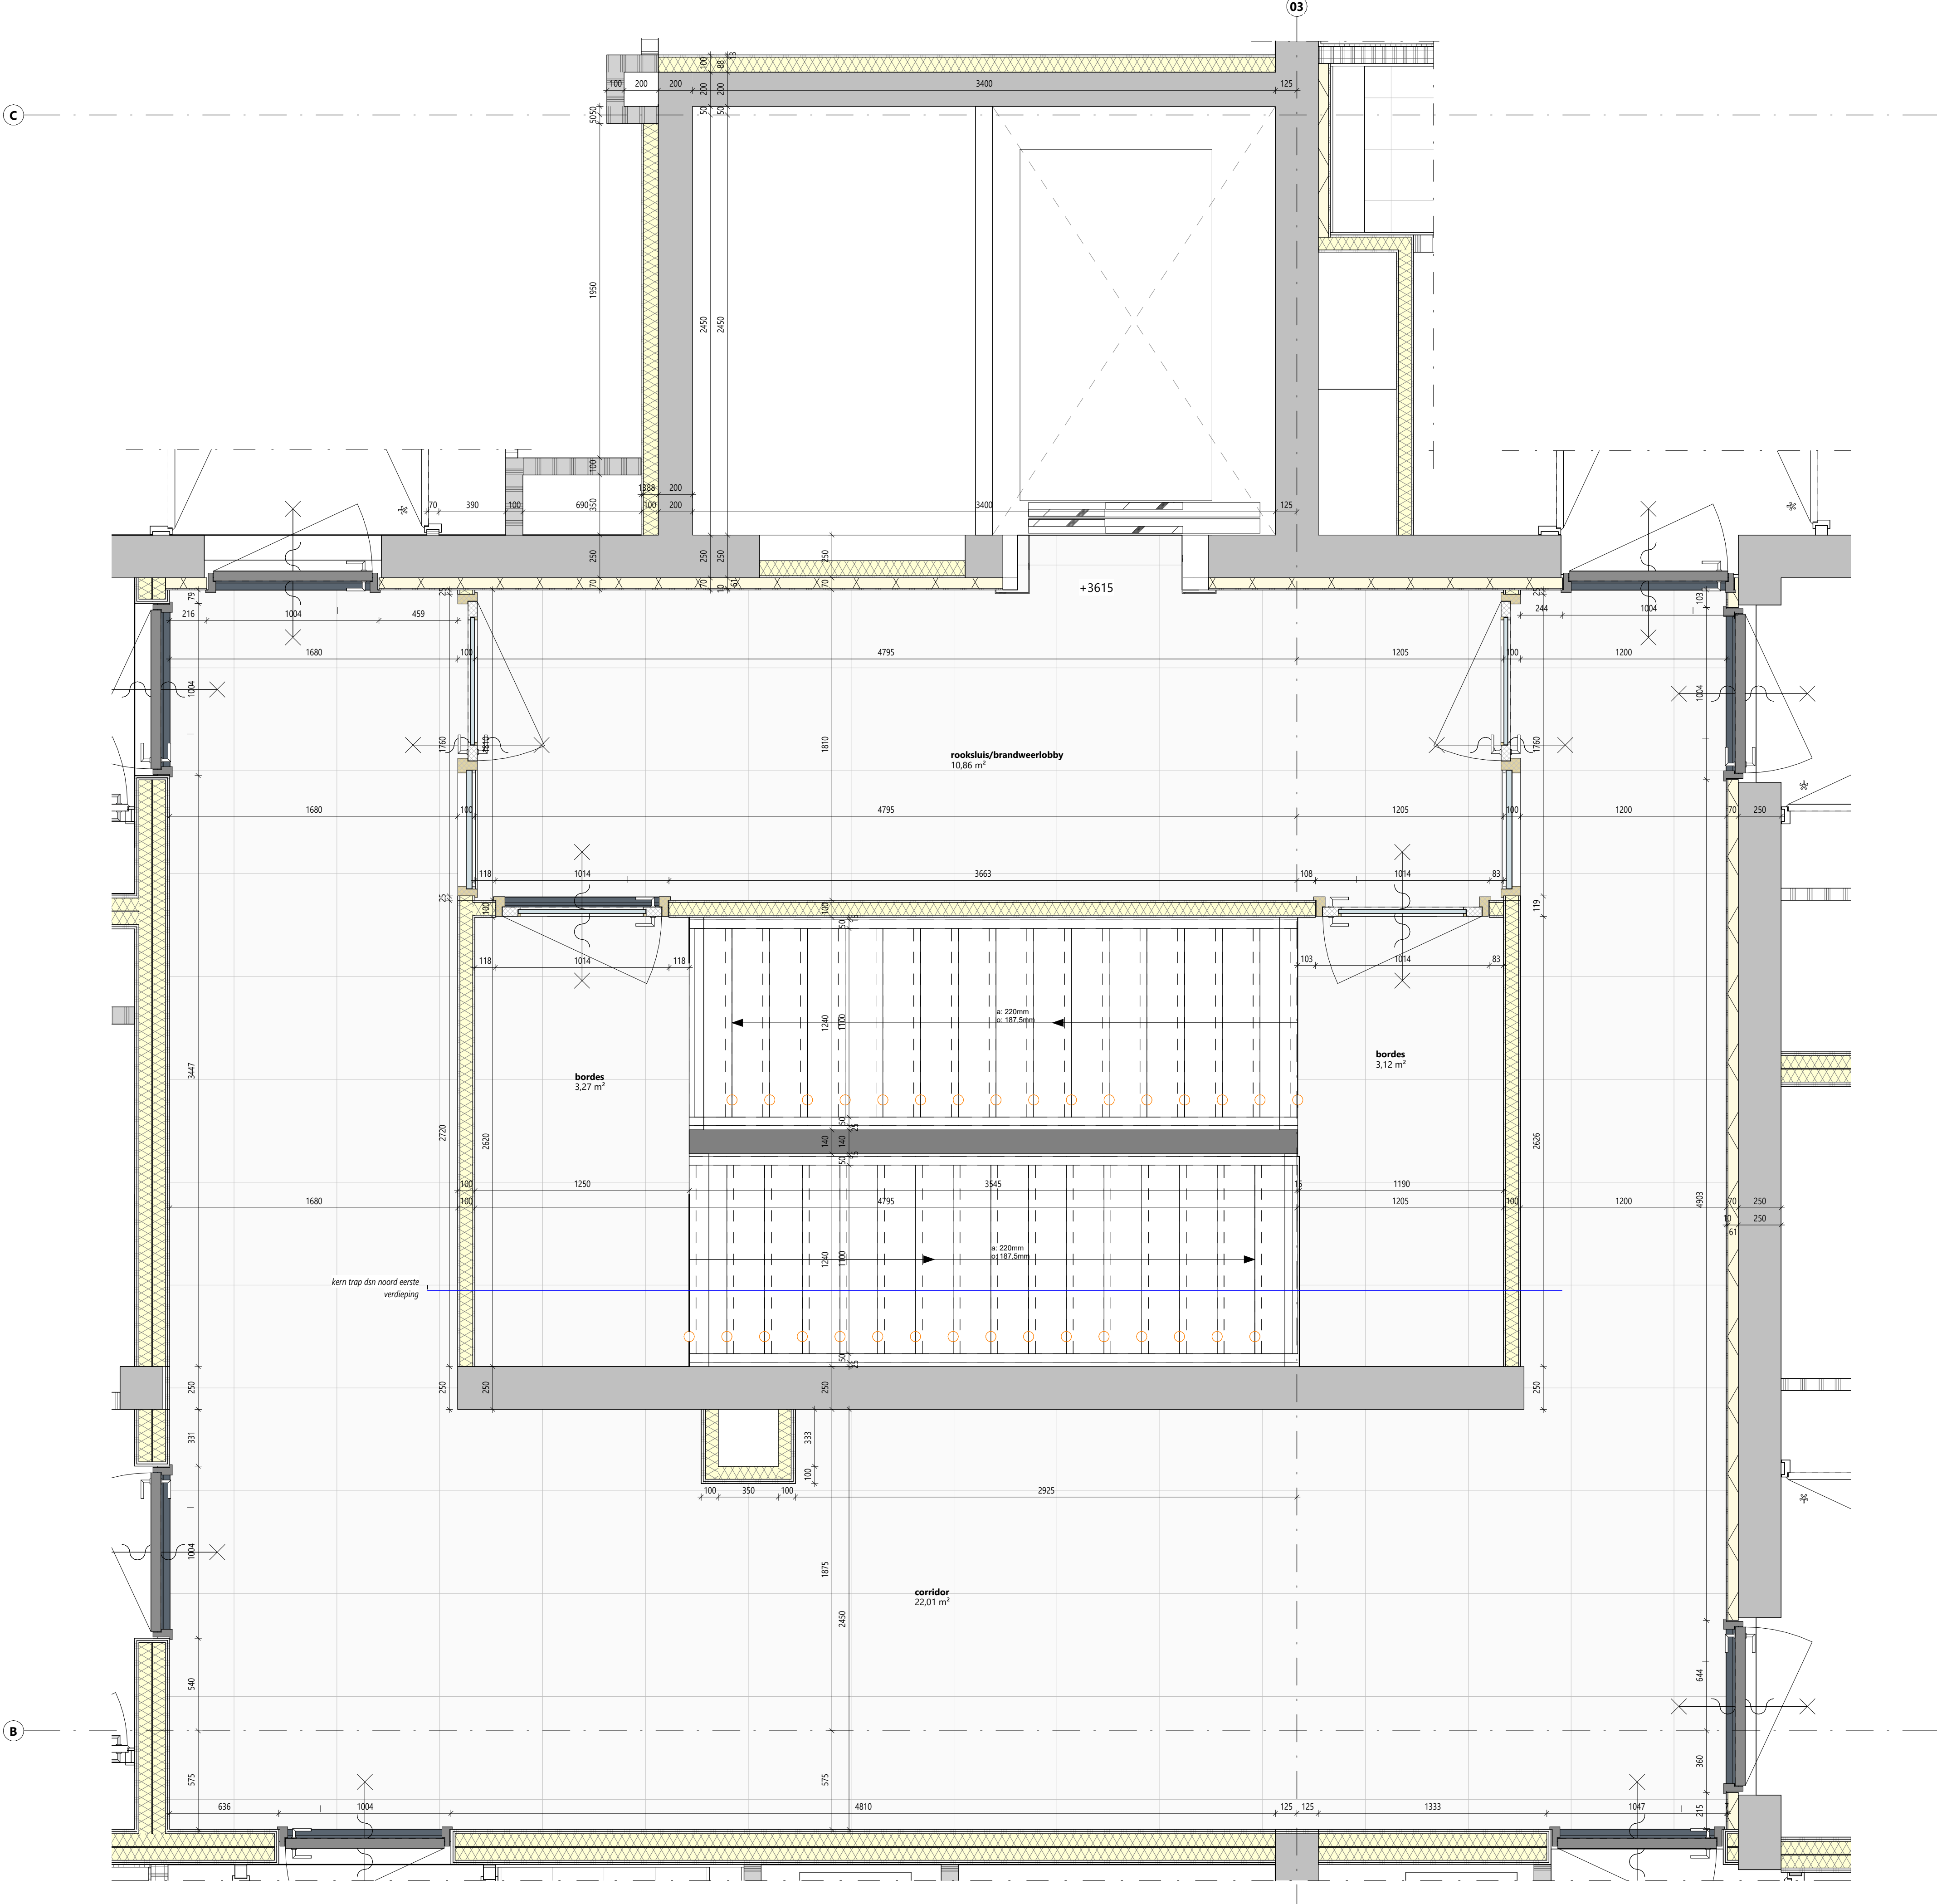

STUDIO
OXs

fragment kern noord 01-03 verdieping

Gouda Harderwijkweg 4, Gouda

Opdrachtgever: Create Realstate Raul Godron



Projectnr: 2459
Fase: TO
Auteur: JKalthof
Formaat: A0
Schale: 1:20
1e datum: 10-11-2025
Status: Definitief
Tekeningsnr: TO-S13

Tekening ongeschikt voor uitvoeringsfase
Geprikt 8-11-2025 17:55:07
Ploeg: Architect: Studio OXS
Gouda KOS/PGS, TO, BAK, DKS, etc.

Piekstraat 27
3071 EL Rotterdam
+31 (0)6 41 23 22 49
info@studiooxs.com

3BM Bouwkunde
Watersloot 17
3335 LV Zoeterwoude
Tel: 075 7465 256
jochem@3bm.nl
www.3bm.nl



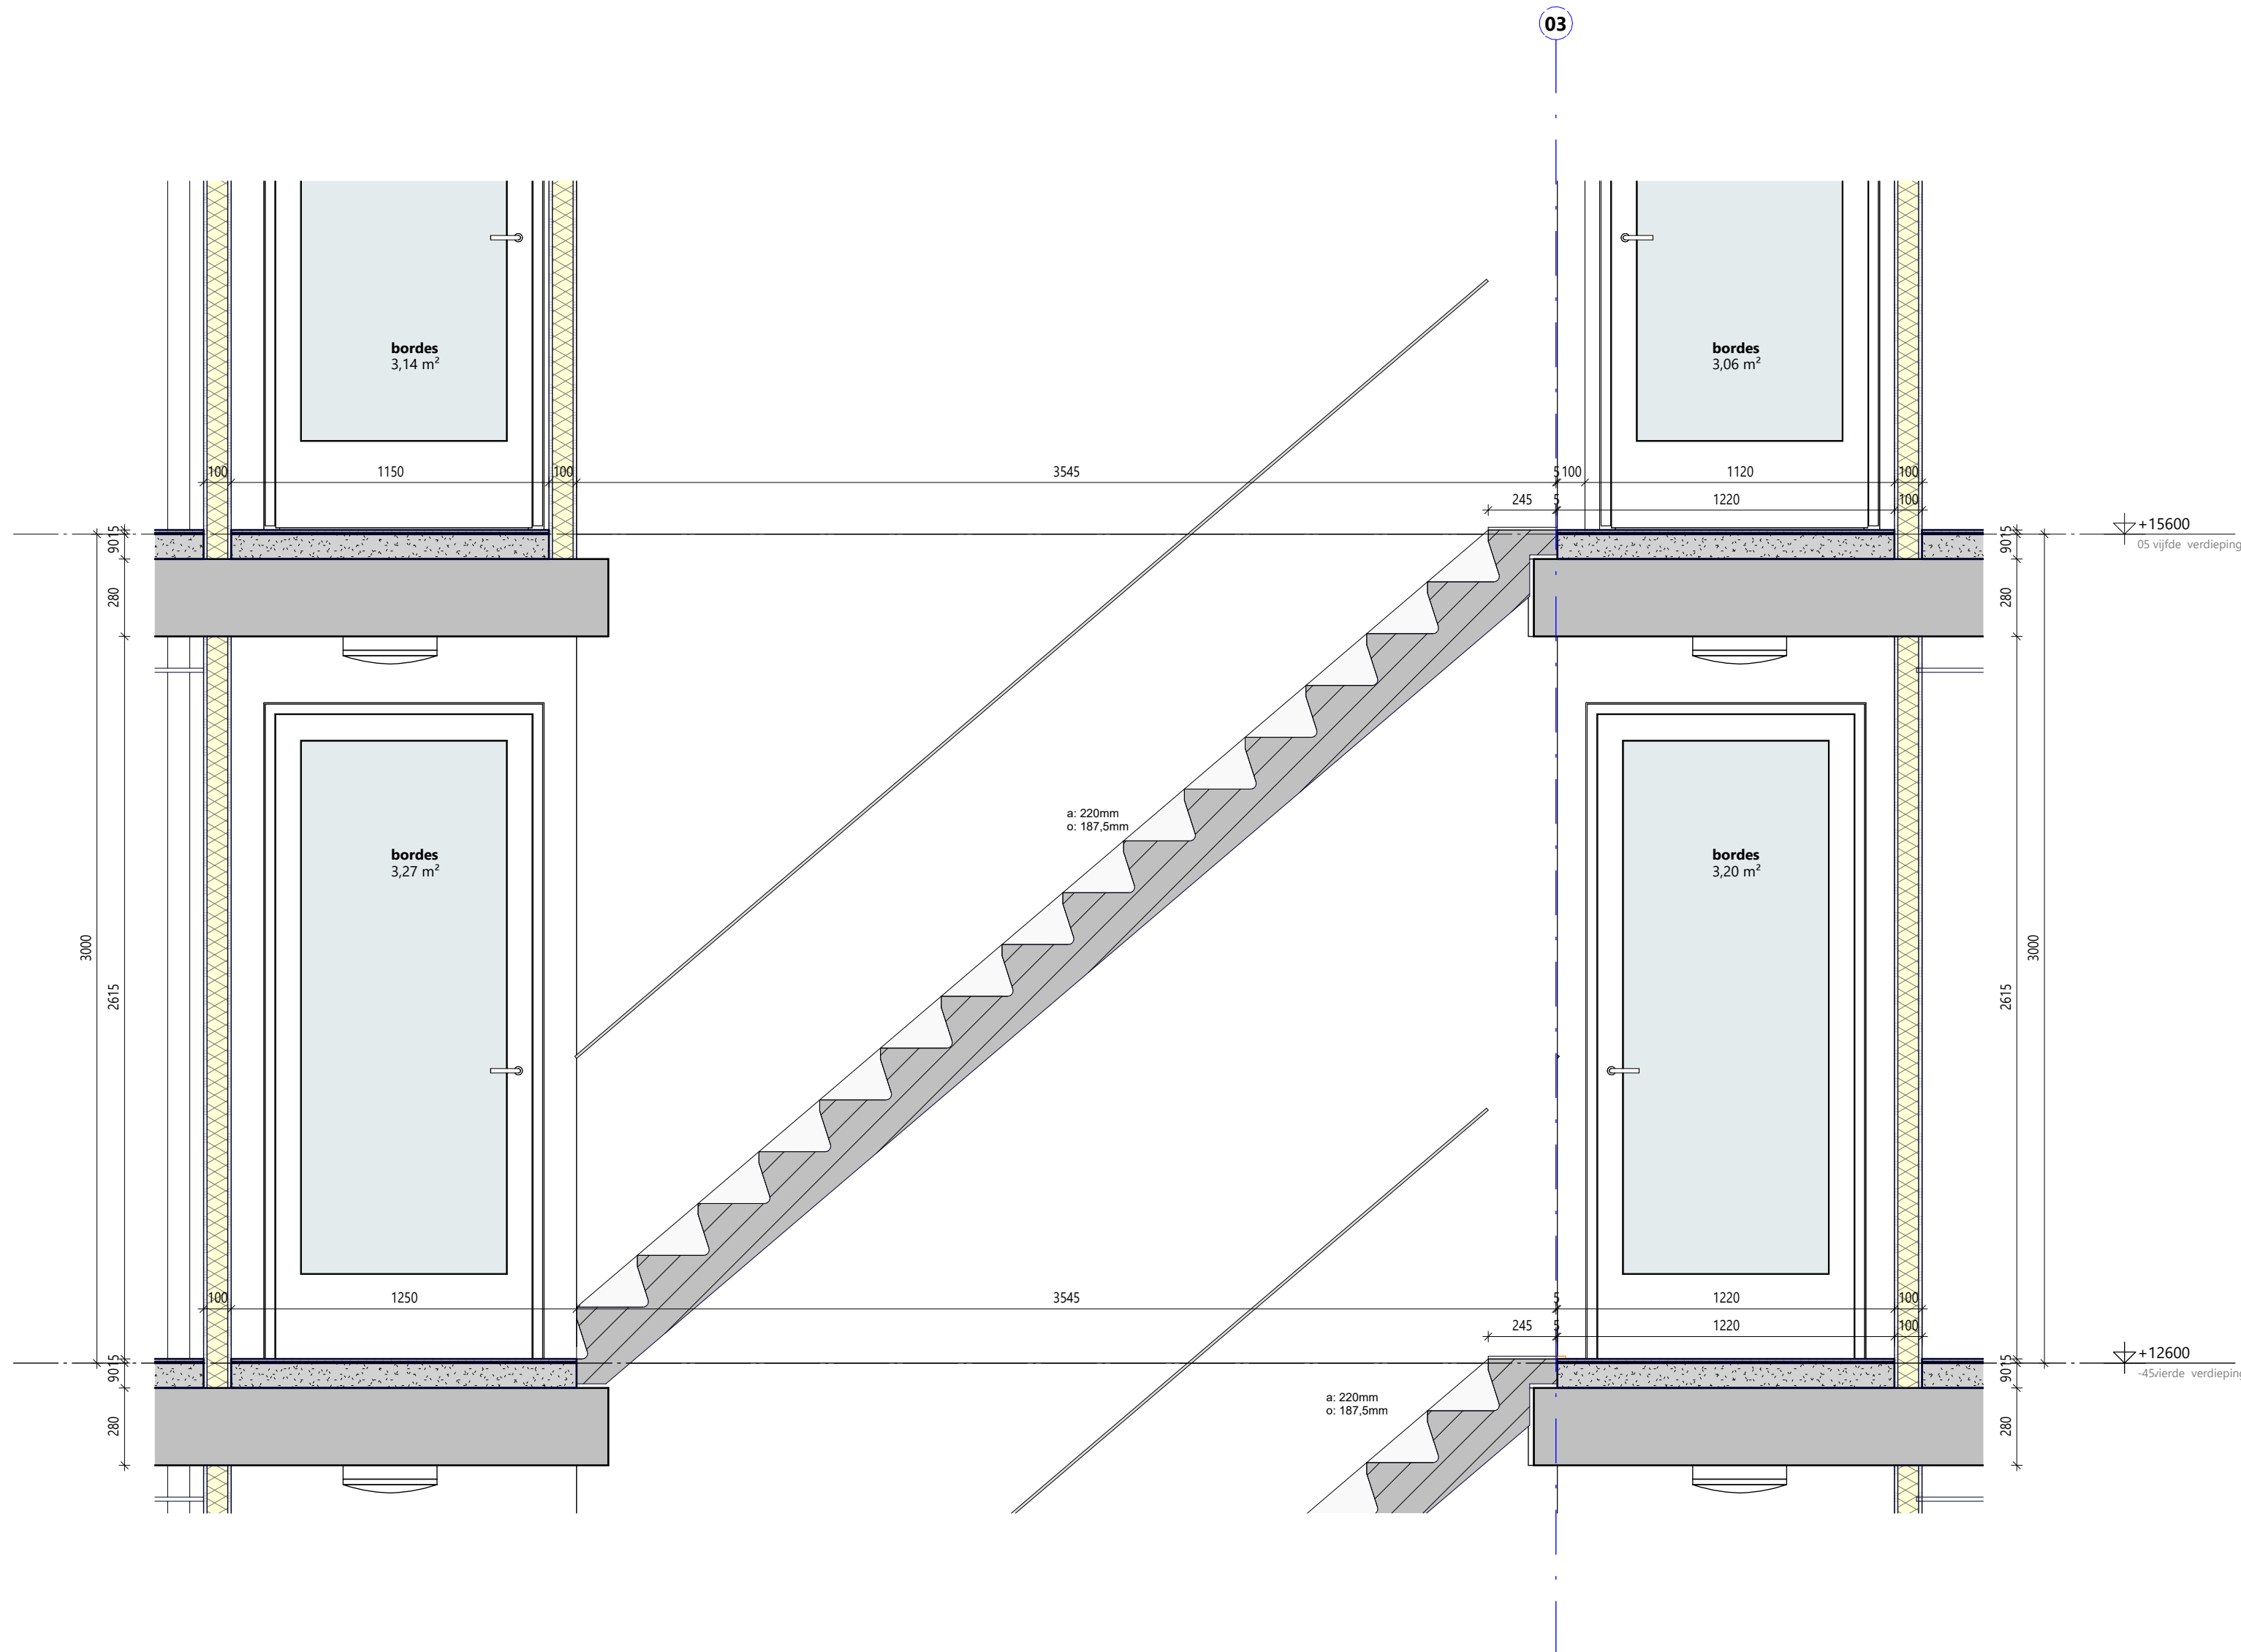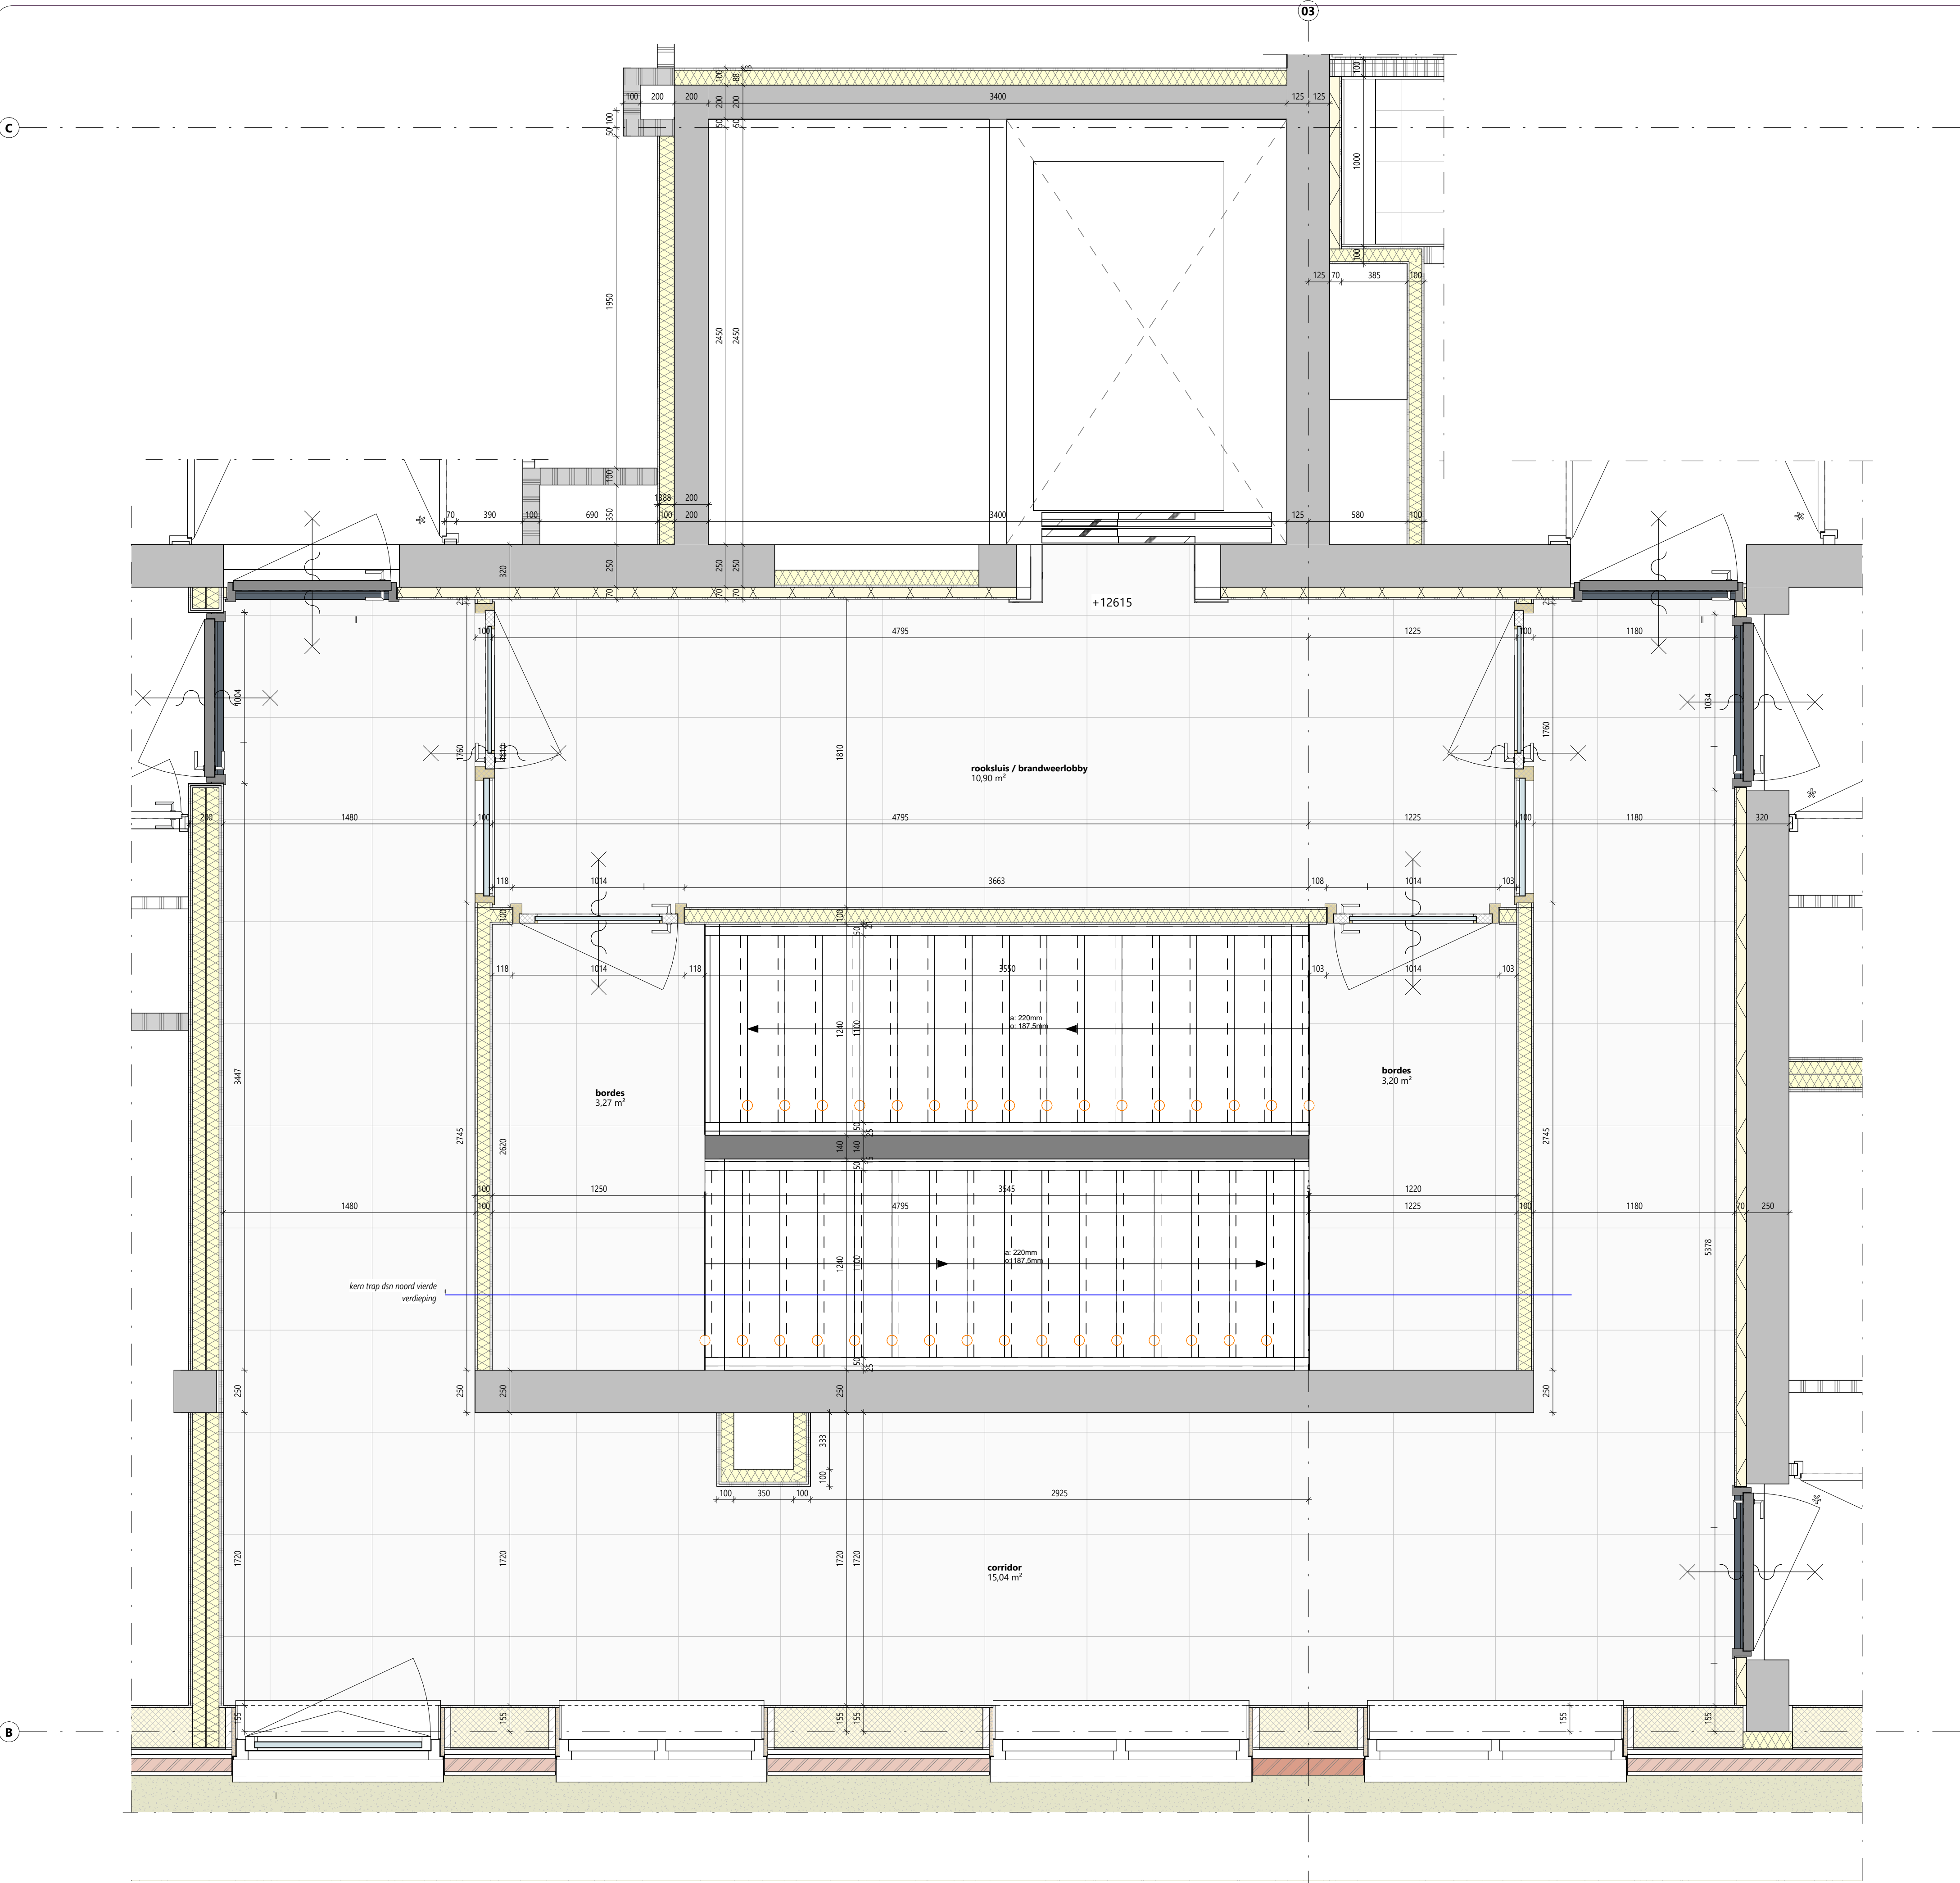

STUDIO
OXs

fragment kern noord 04 verdieping

Gouda Harderwijkweg 4, Gouda

Opdrachtgever: Create Realstate Raul Godron

Projectnr: 2459
Fase: TO
Auteur: J.Kalhof


Formaat: A0
Schale: 1:20
1e datum: 10-11-2025
Status: Definitief
Tekeningsnr: TO-S14

Tekening ongeschikt voor uitvoeringsfase
Geprint: 8-11-2025 17:55:09
Ploeg: Architect: StudioOXs Architect: Gouda KOLPWS, TO, BAK, OOS, etc.

Piekstraat 27
3071 EL Rotterdam
+31 (0)6 41 23 22 49
info@studiooxs.com

3BM Bouwkunde
Watersstraat 17
3335 LV Zoeterwoude
Tel: 078 7460 256
jochem@3bm.co.nl
www.3bm.co.nl



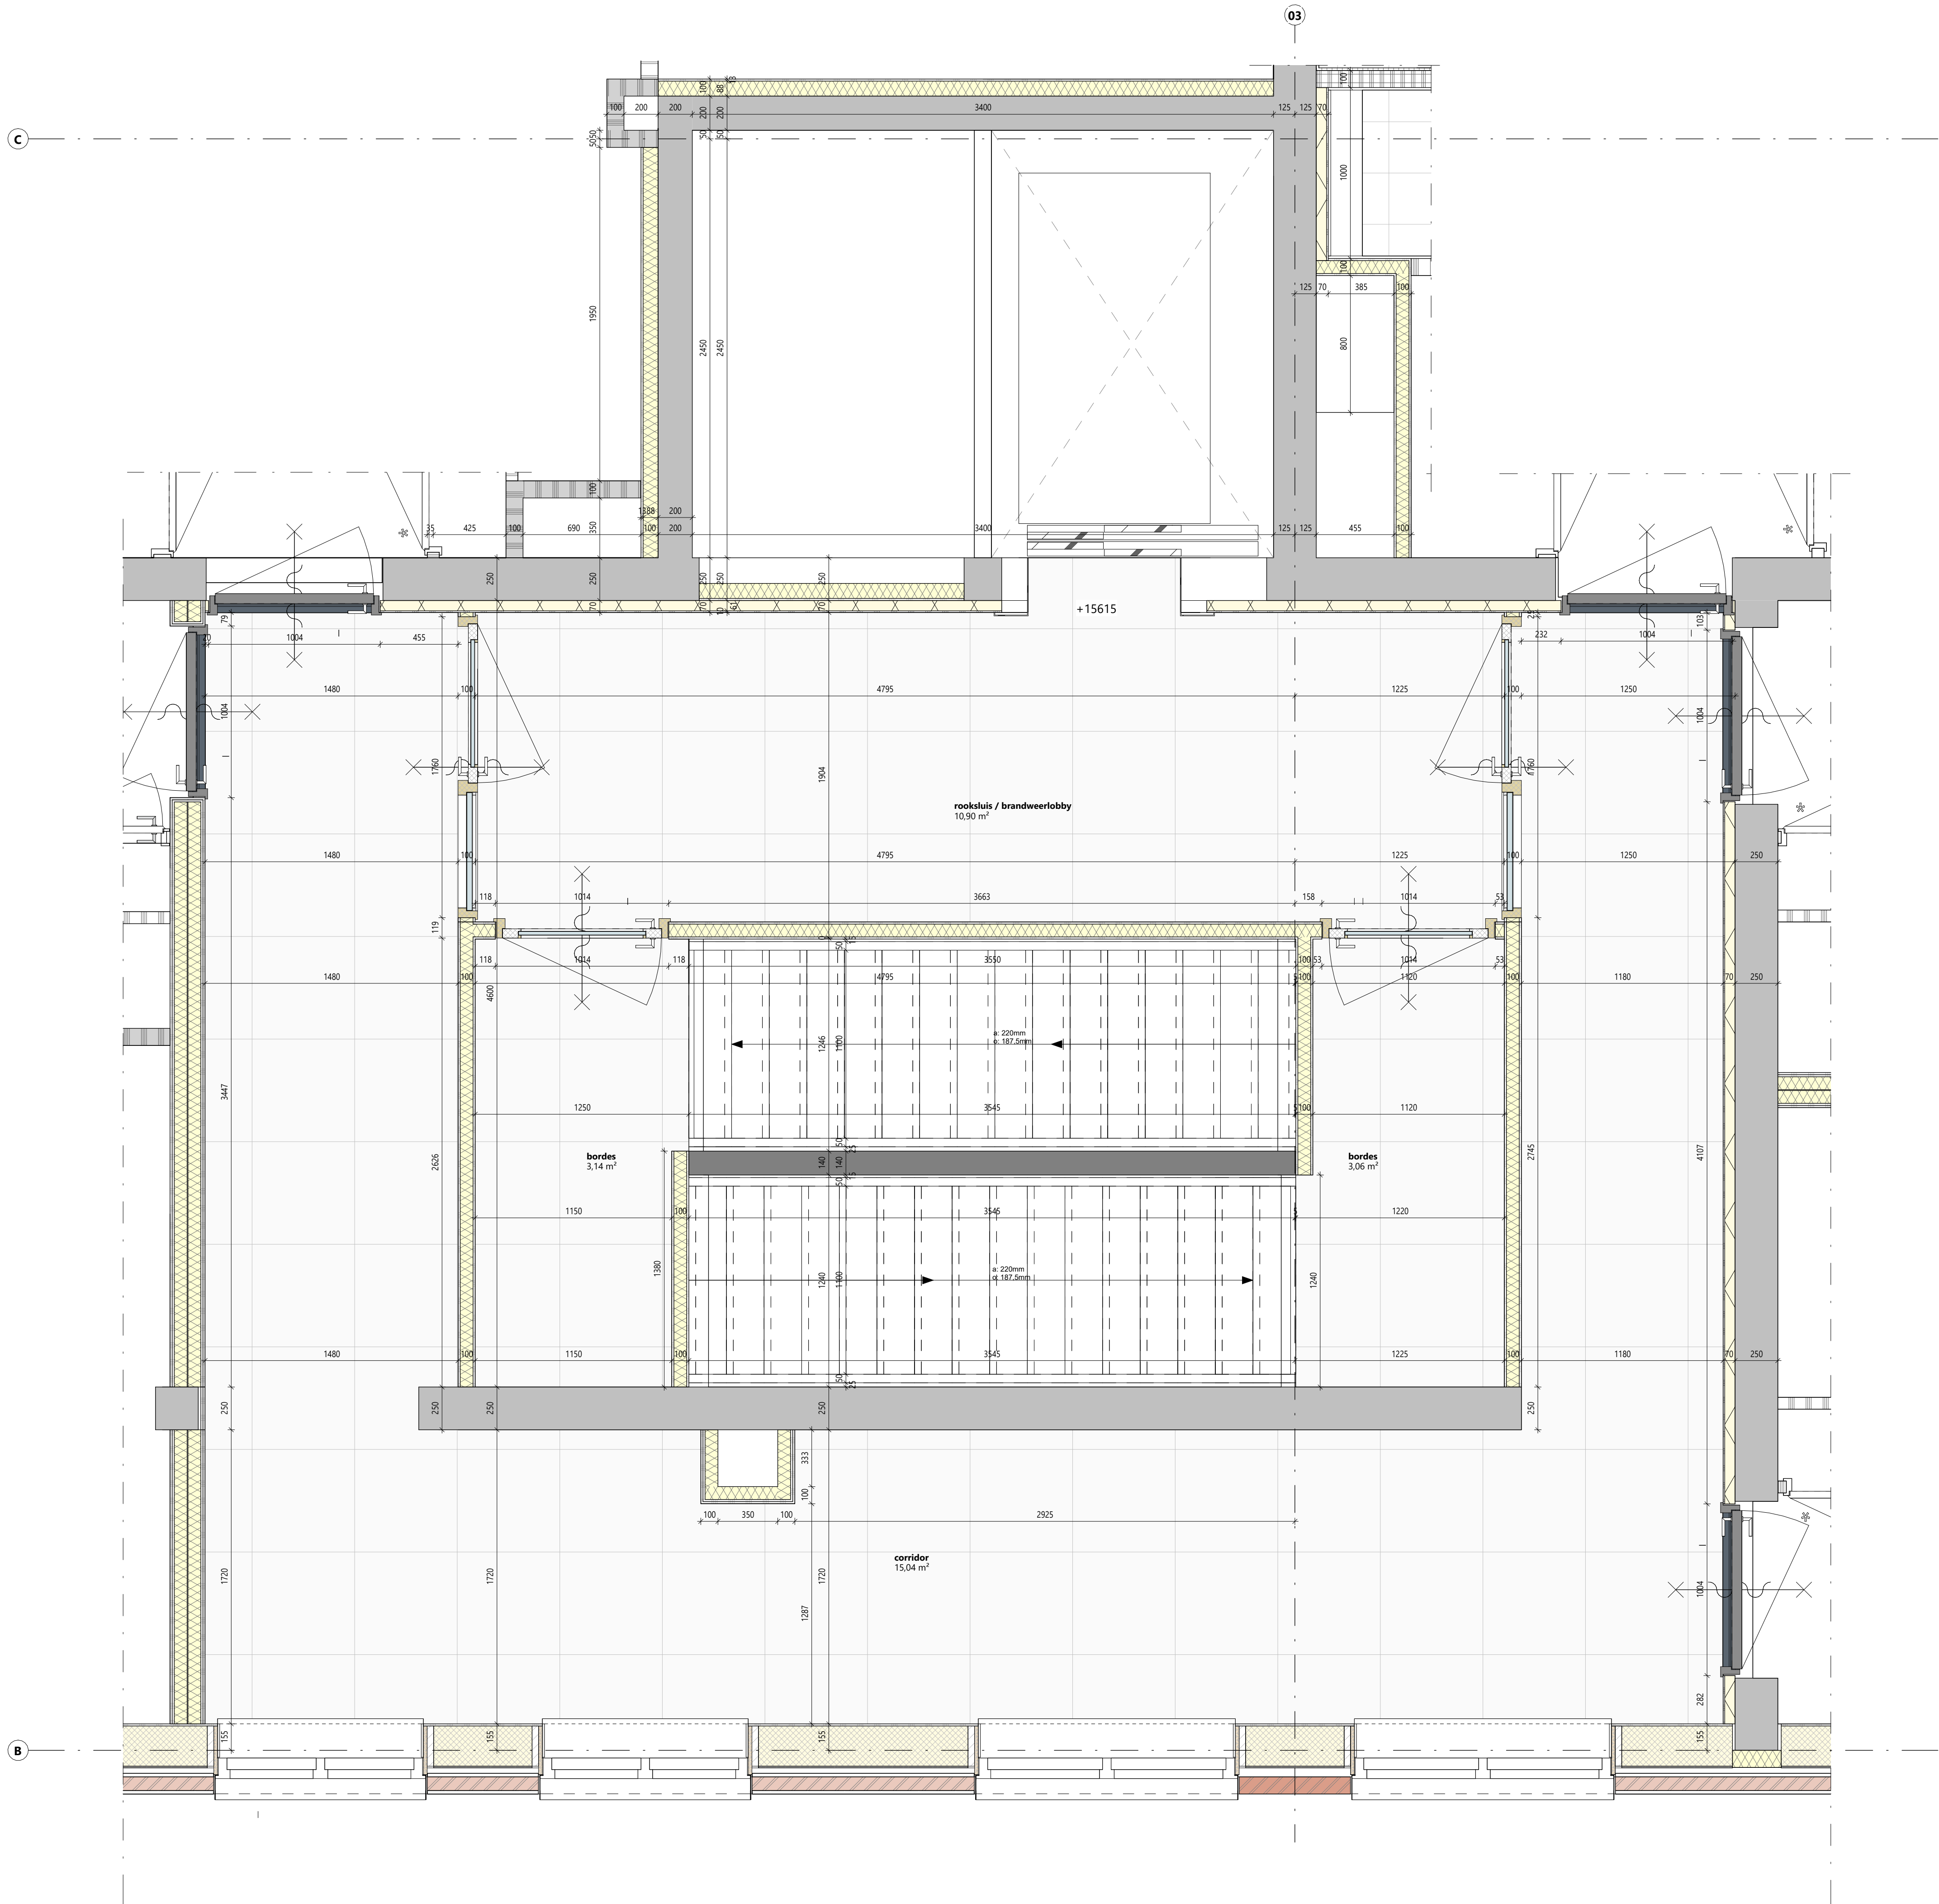

STUDIO
OXs

fragment kern noord 05 verdieping

Gouda Harderwijkweg
Harderwijkweg 4, Gouda

Opdrachtgever: Create Real Estate Raul Godron

Projectnr: 2459
Fase: TO
Auteur: JKolthof

Formaat: A1
Schaal: 1:20
1^e datum: 10-11-2025
Status: Definitief
Tekeningnr: TO-515

3bm
Ingenieurs van oplossingen



Tekening ongeschikt voor uitvoeringsfase
Geprint 8-11-2025 17:55:10

Piekstraat 27
3071 EL Rotterdam
+31 (0)6 41 23 22 49
info@studiooxs.com

3BM Bouwkunde
Wattstraat 17
3335 LV Zwijndrecht

Tel: 078 7400 258
jochem@3bm.co.nl
www.3bm.co.nl



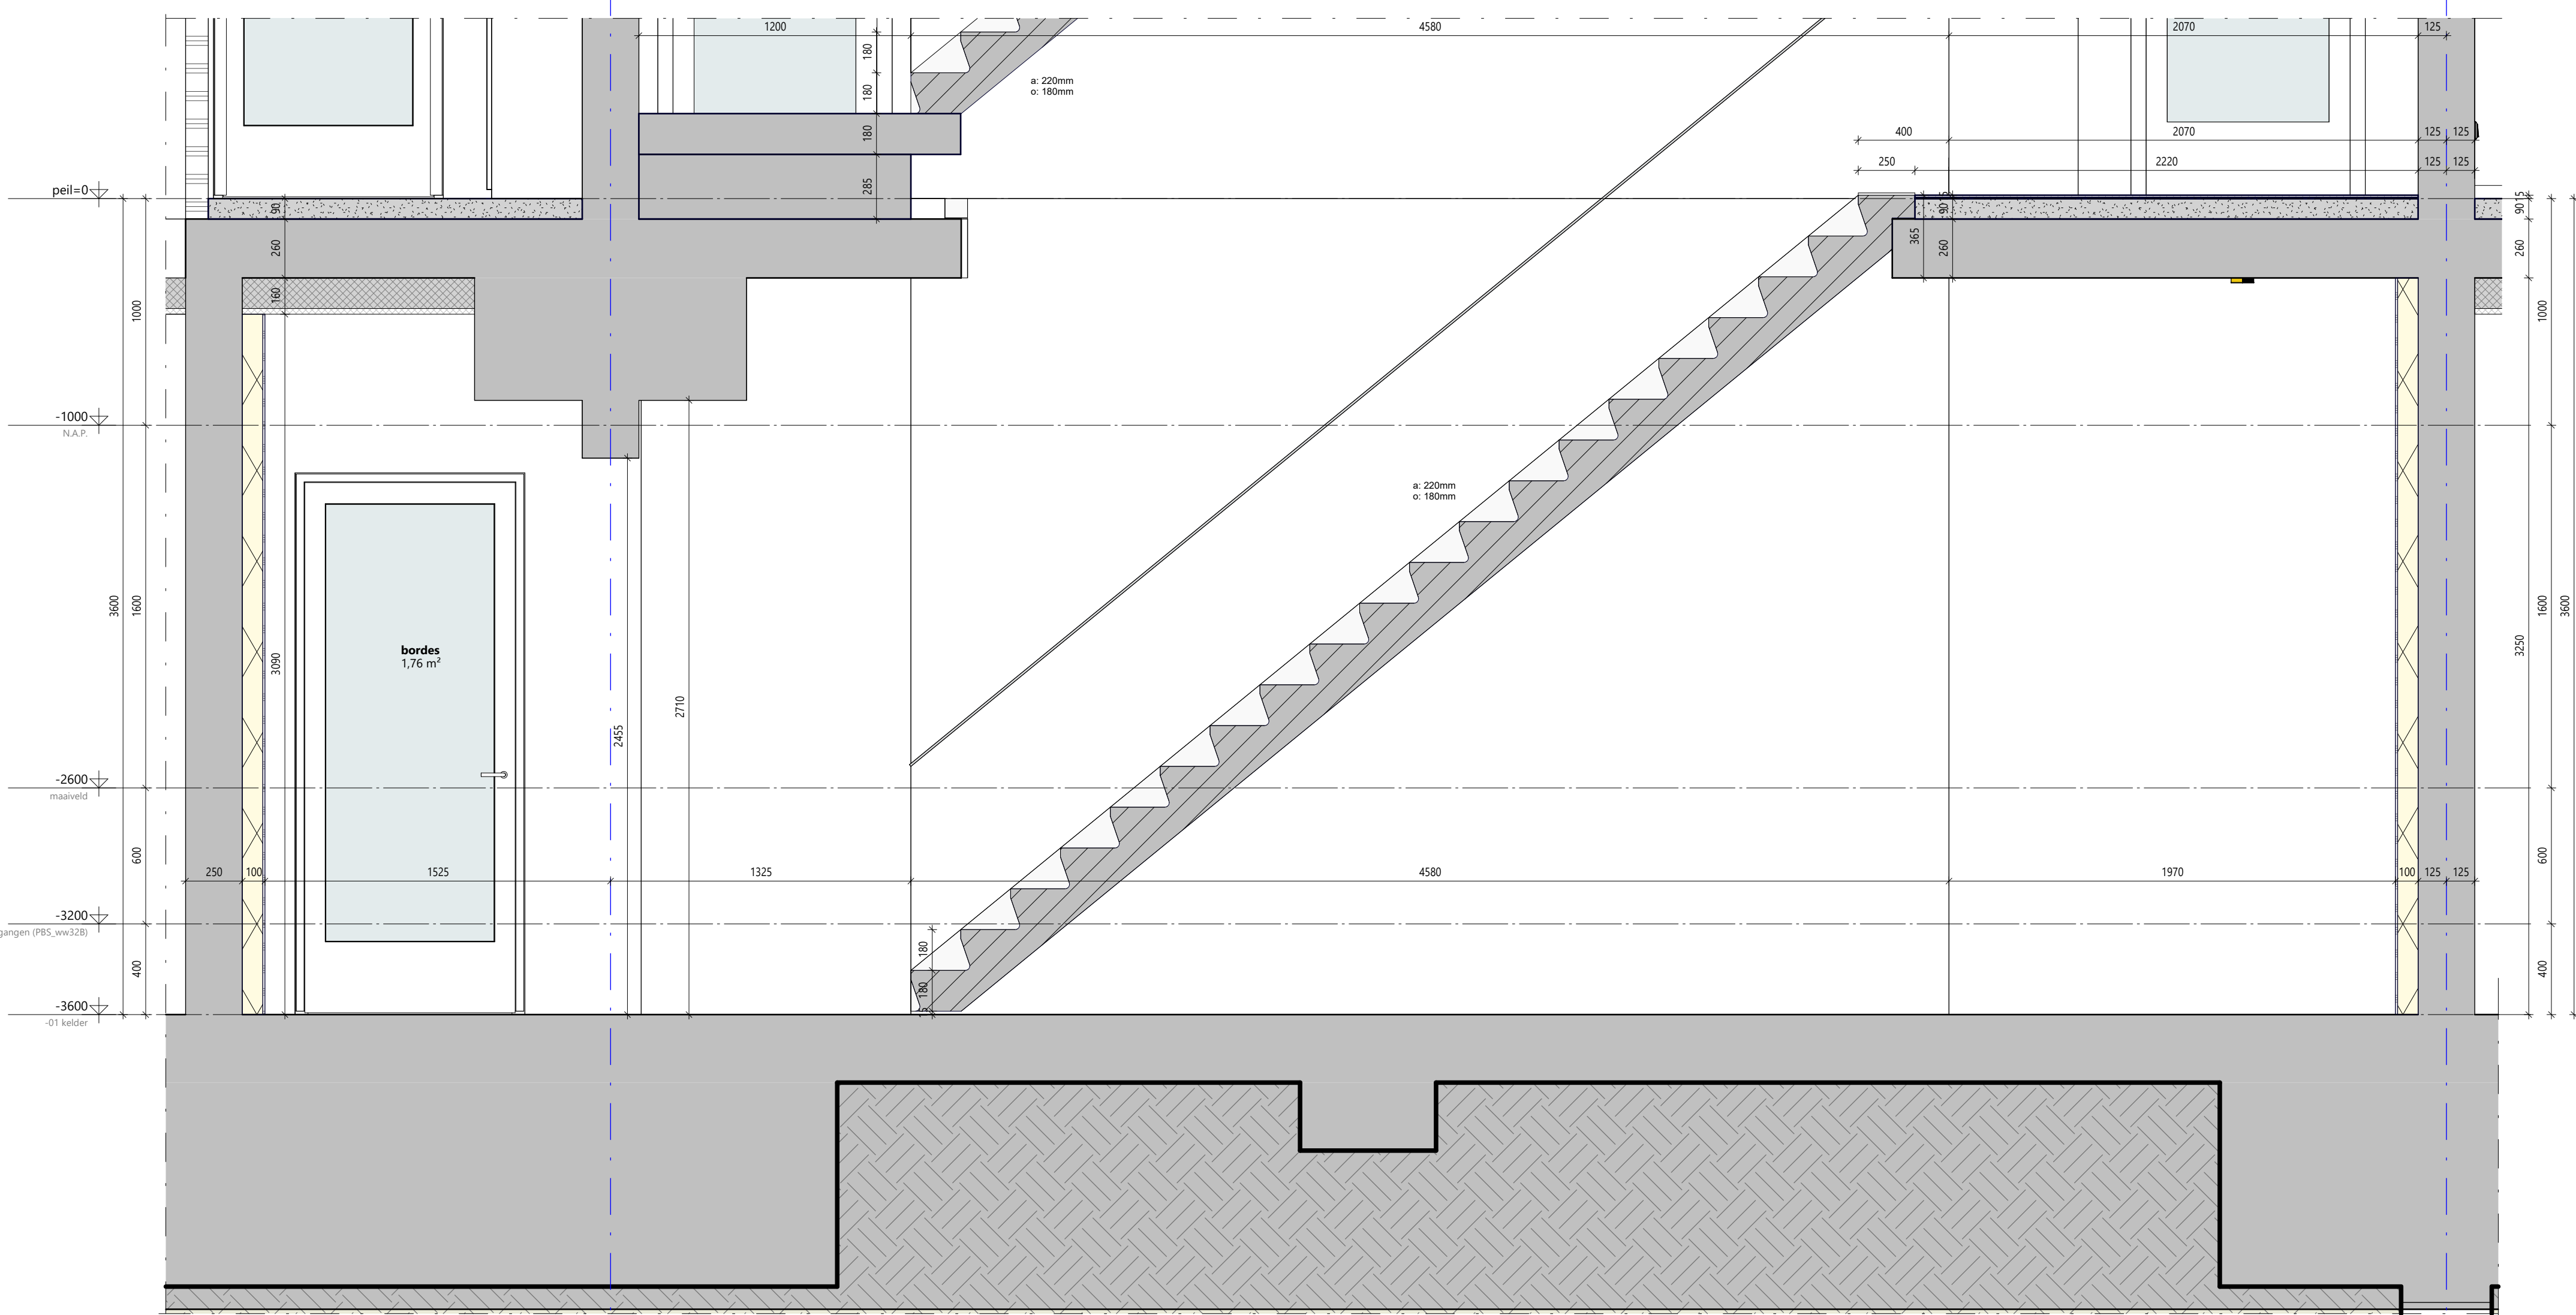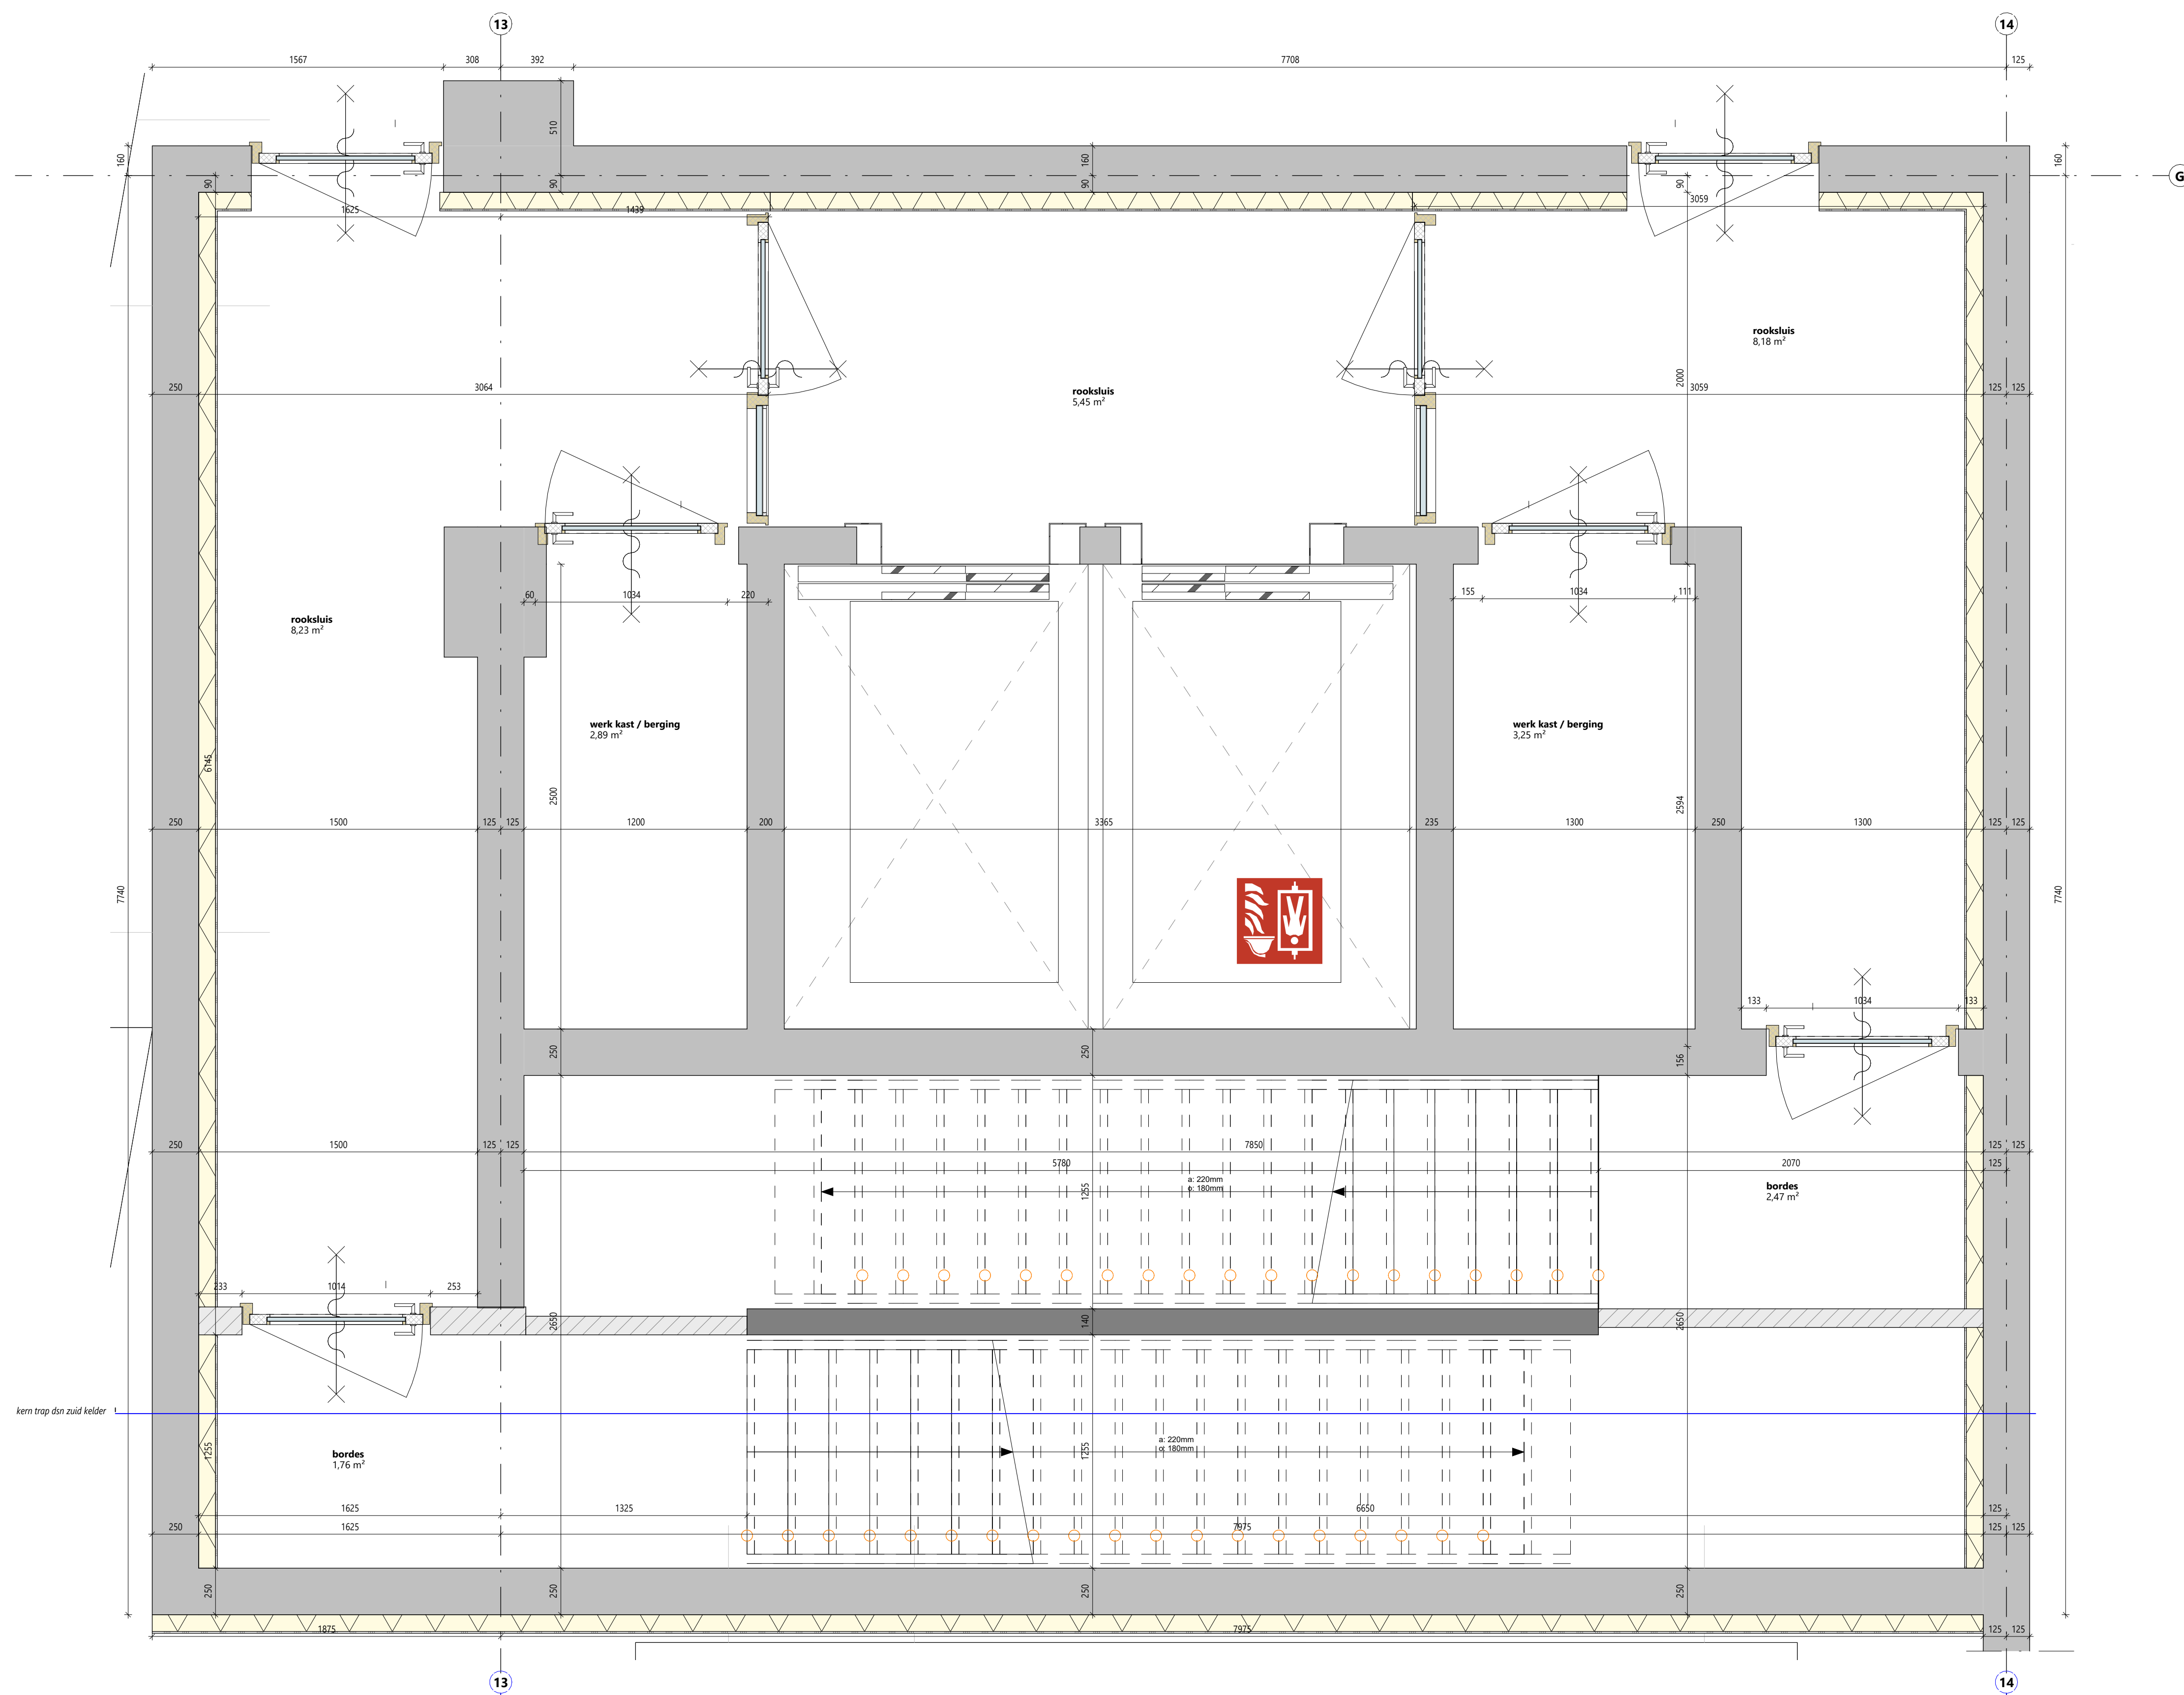

STUDIO
OXs

fragment kern zuid kelder

Gouda Harderwijkweg
Harderwijkweg 4, Gouda

Opdrachtgever: Create Realstate Raul Godron

Projectnr: 2459
Fase: TO
Auteur: J.Kalthof

Formaat: A0
Schale: 1:20
1e datum: 10-11-2025
Status: Definitief
Tekeningnr: TO-S16



3bm
Ingenieurs van oplossingen

Tekening ongeschikt voor uitvoeringsfase
Geprint: 8-11-2025 17:55:12
Ploeg: Architect: StudioOXs, Tekenaar: Gouda KOS/PWS, TO: BWM, DKS, etc.

Piekstraat 27
3071 EL Rotterdam
+31 (0)6 41 23 22 49
info@studiooxs.com

3BM Bouwkunde
Watersstraat 17
3335 LV Zoeterwoud
Tel: 075 7600 256
jochem@3bm.co.nl
www.3bm.co.nl



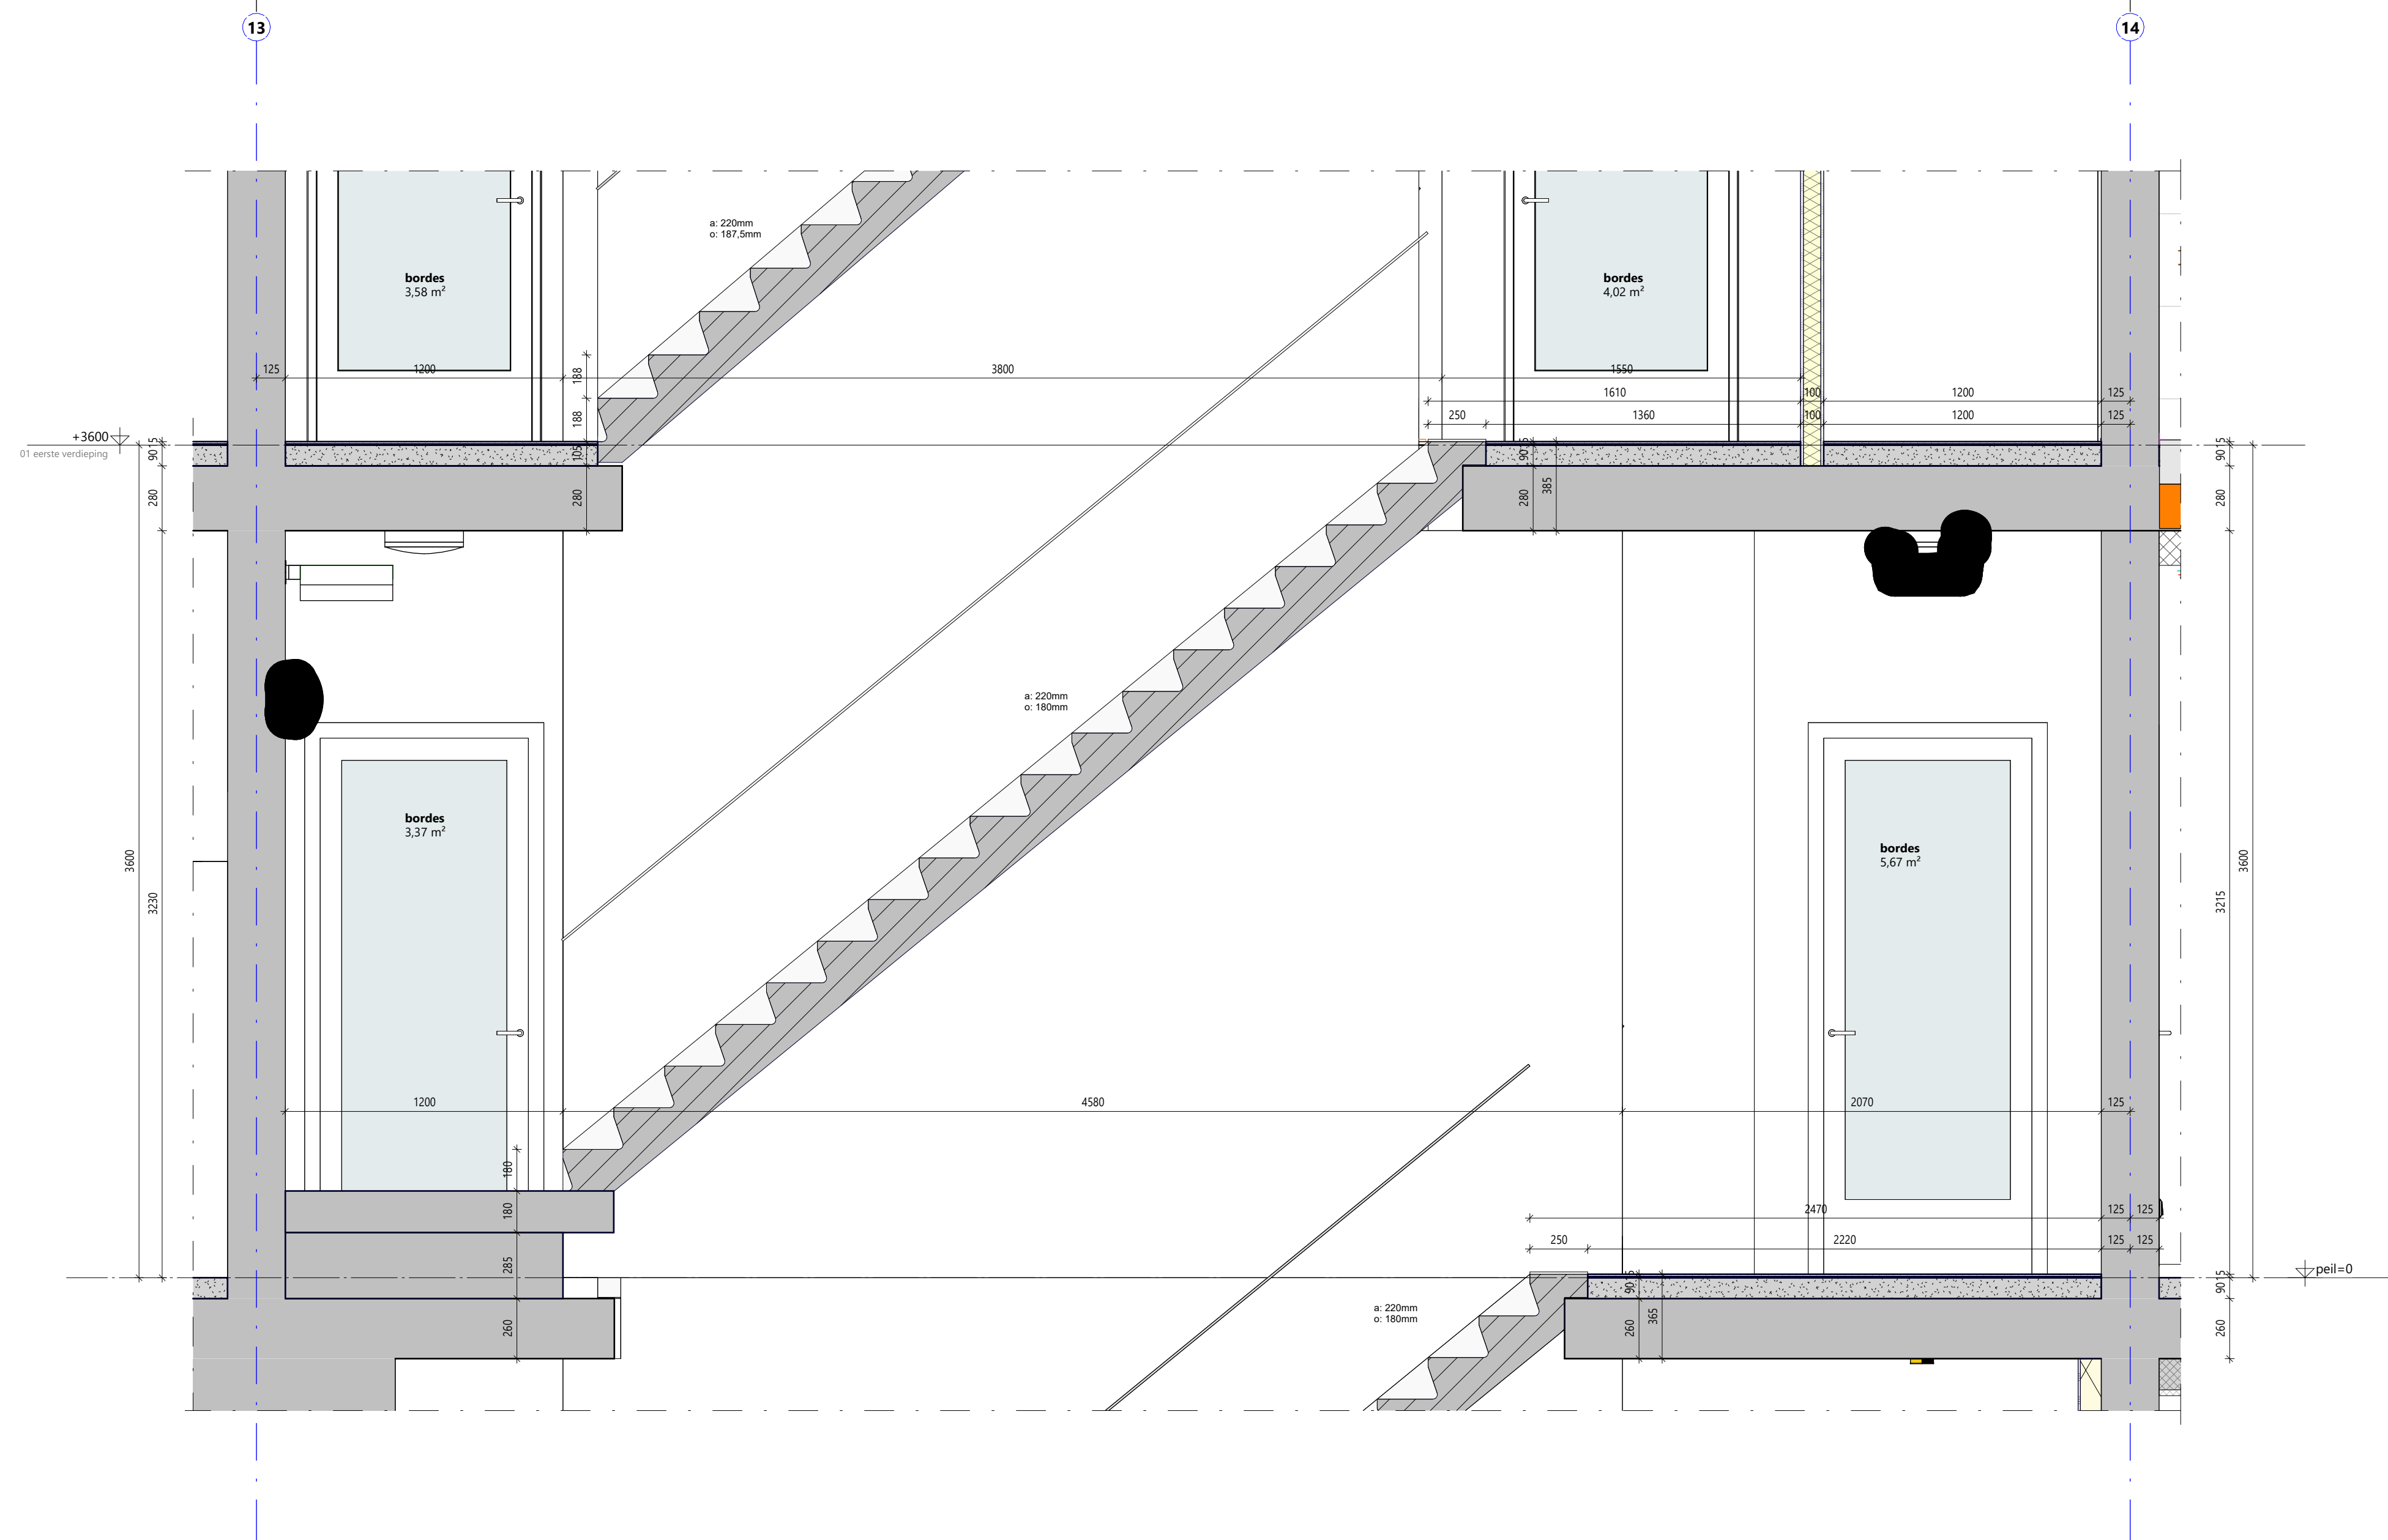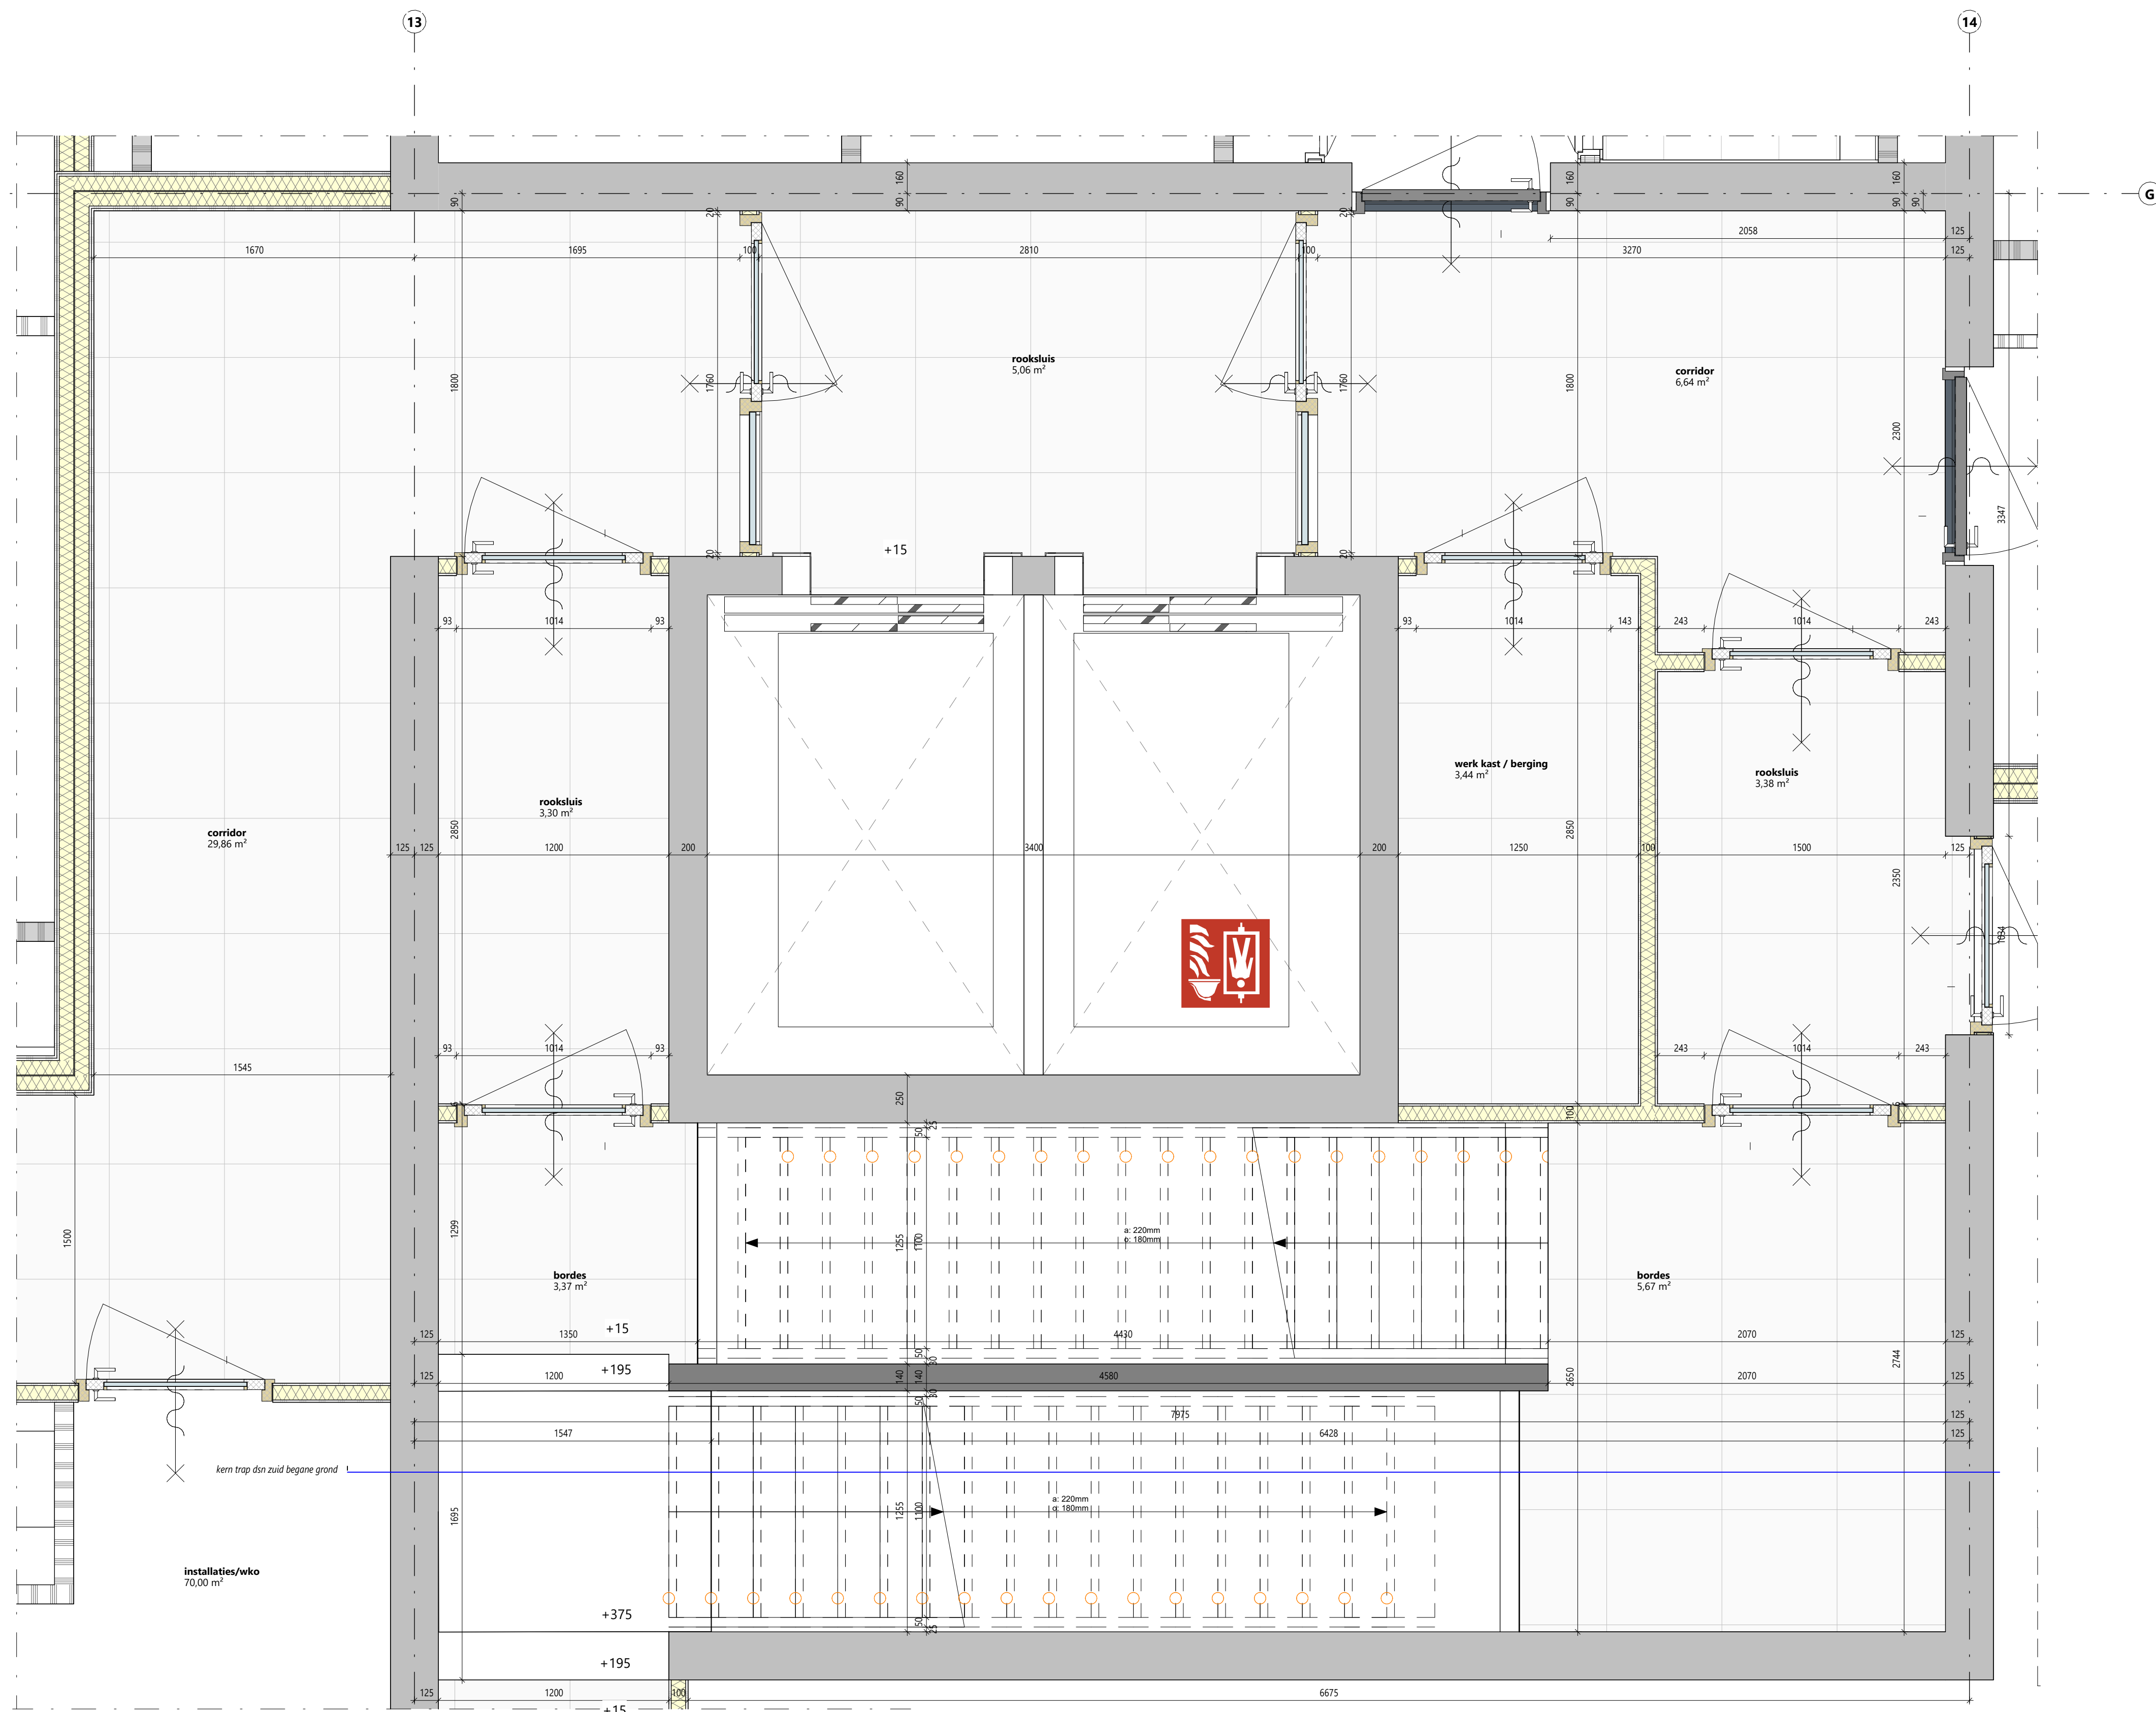

STUDIO
OXs

fragment kern zuid begane grond

Gouda Harderwijkweg
Harderwijkweg 4, Gouda

Opdrachtgever: Create Real Estate Raul Godron

Projectnr: 2459
Fase: TO
Auteur: J.Kalthof

Formaat: A0
Schaal: 1:20
1^o datum: 10-11-2025
Status: Definitief
Tekeningnr: TO-S17


3bm
Ingenieurs van oplossingen


Tekening ongeschikt voor uitvoeringsfase
Geprikt 8-11-2025 17:55:15
Ploeg: Architect: Dries van Oort / Gouda: Kees Pijls, To: Raul Godron

Piekstraat 27
3071 EL Rotterdam
+31 (0)6 41 23 22 49
info@studiooxs.com

3BM Bouwkunde
Watersstraat 17
3335 LV Zoetermeer
Tel: 078 7600 256
jochem@3bm.nl
www.3bm.nl



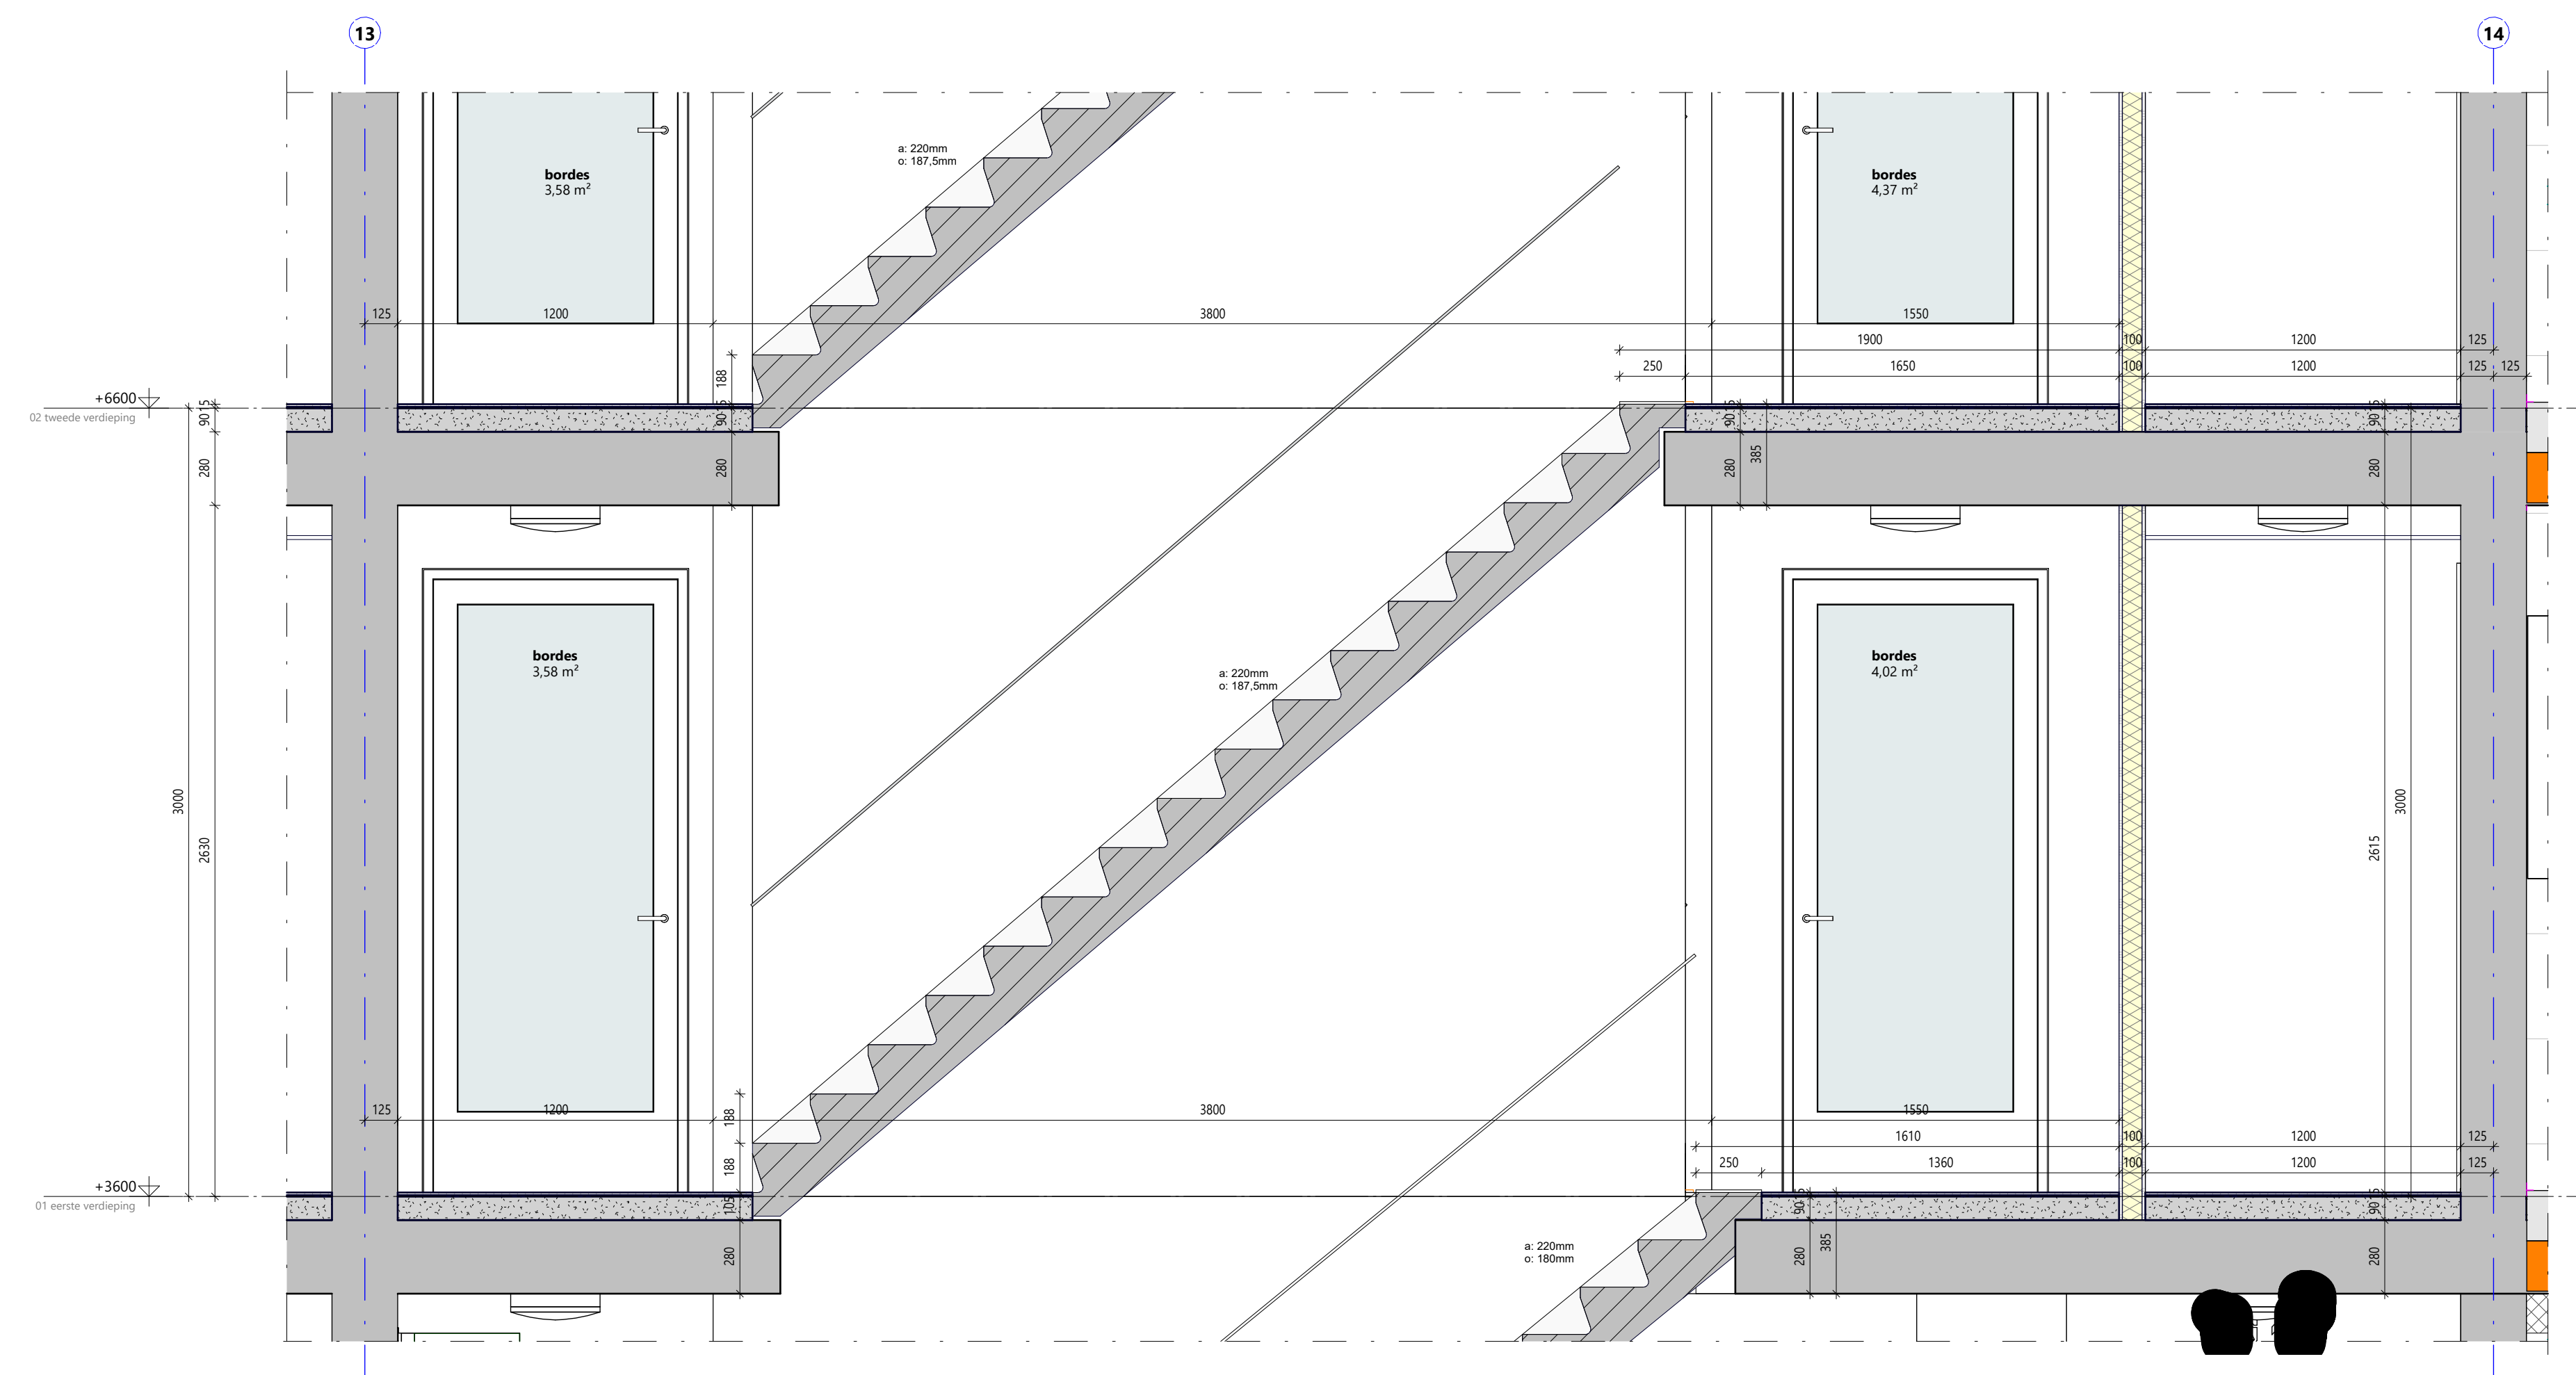

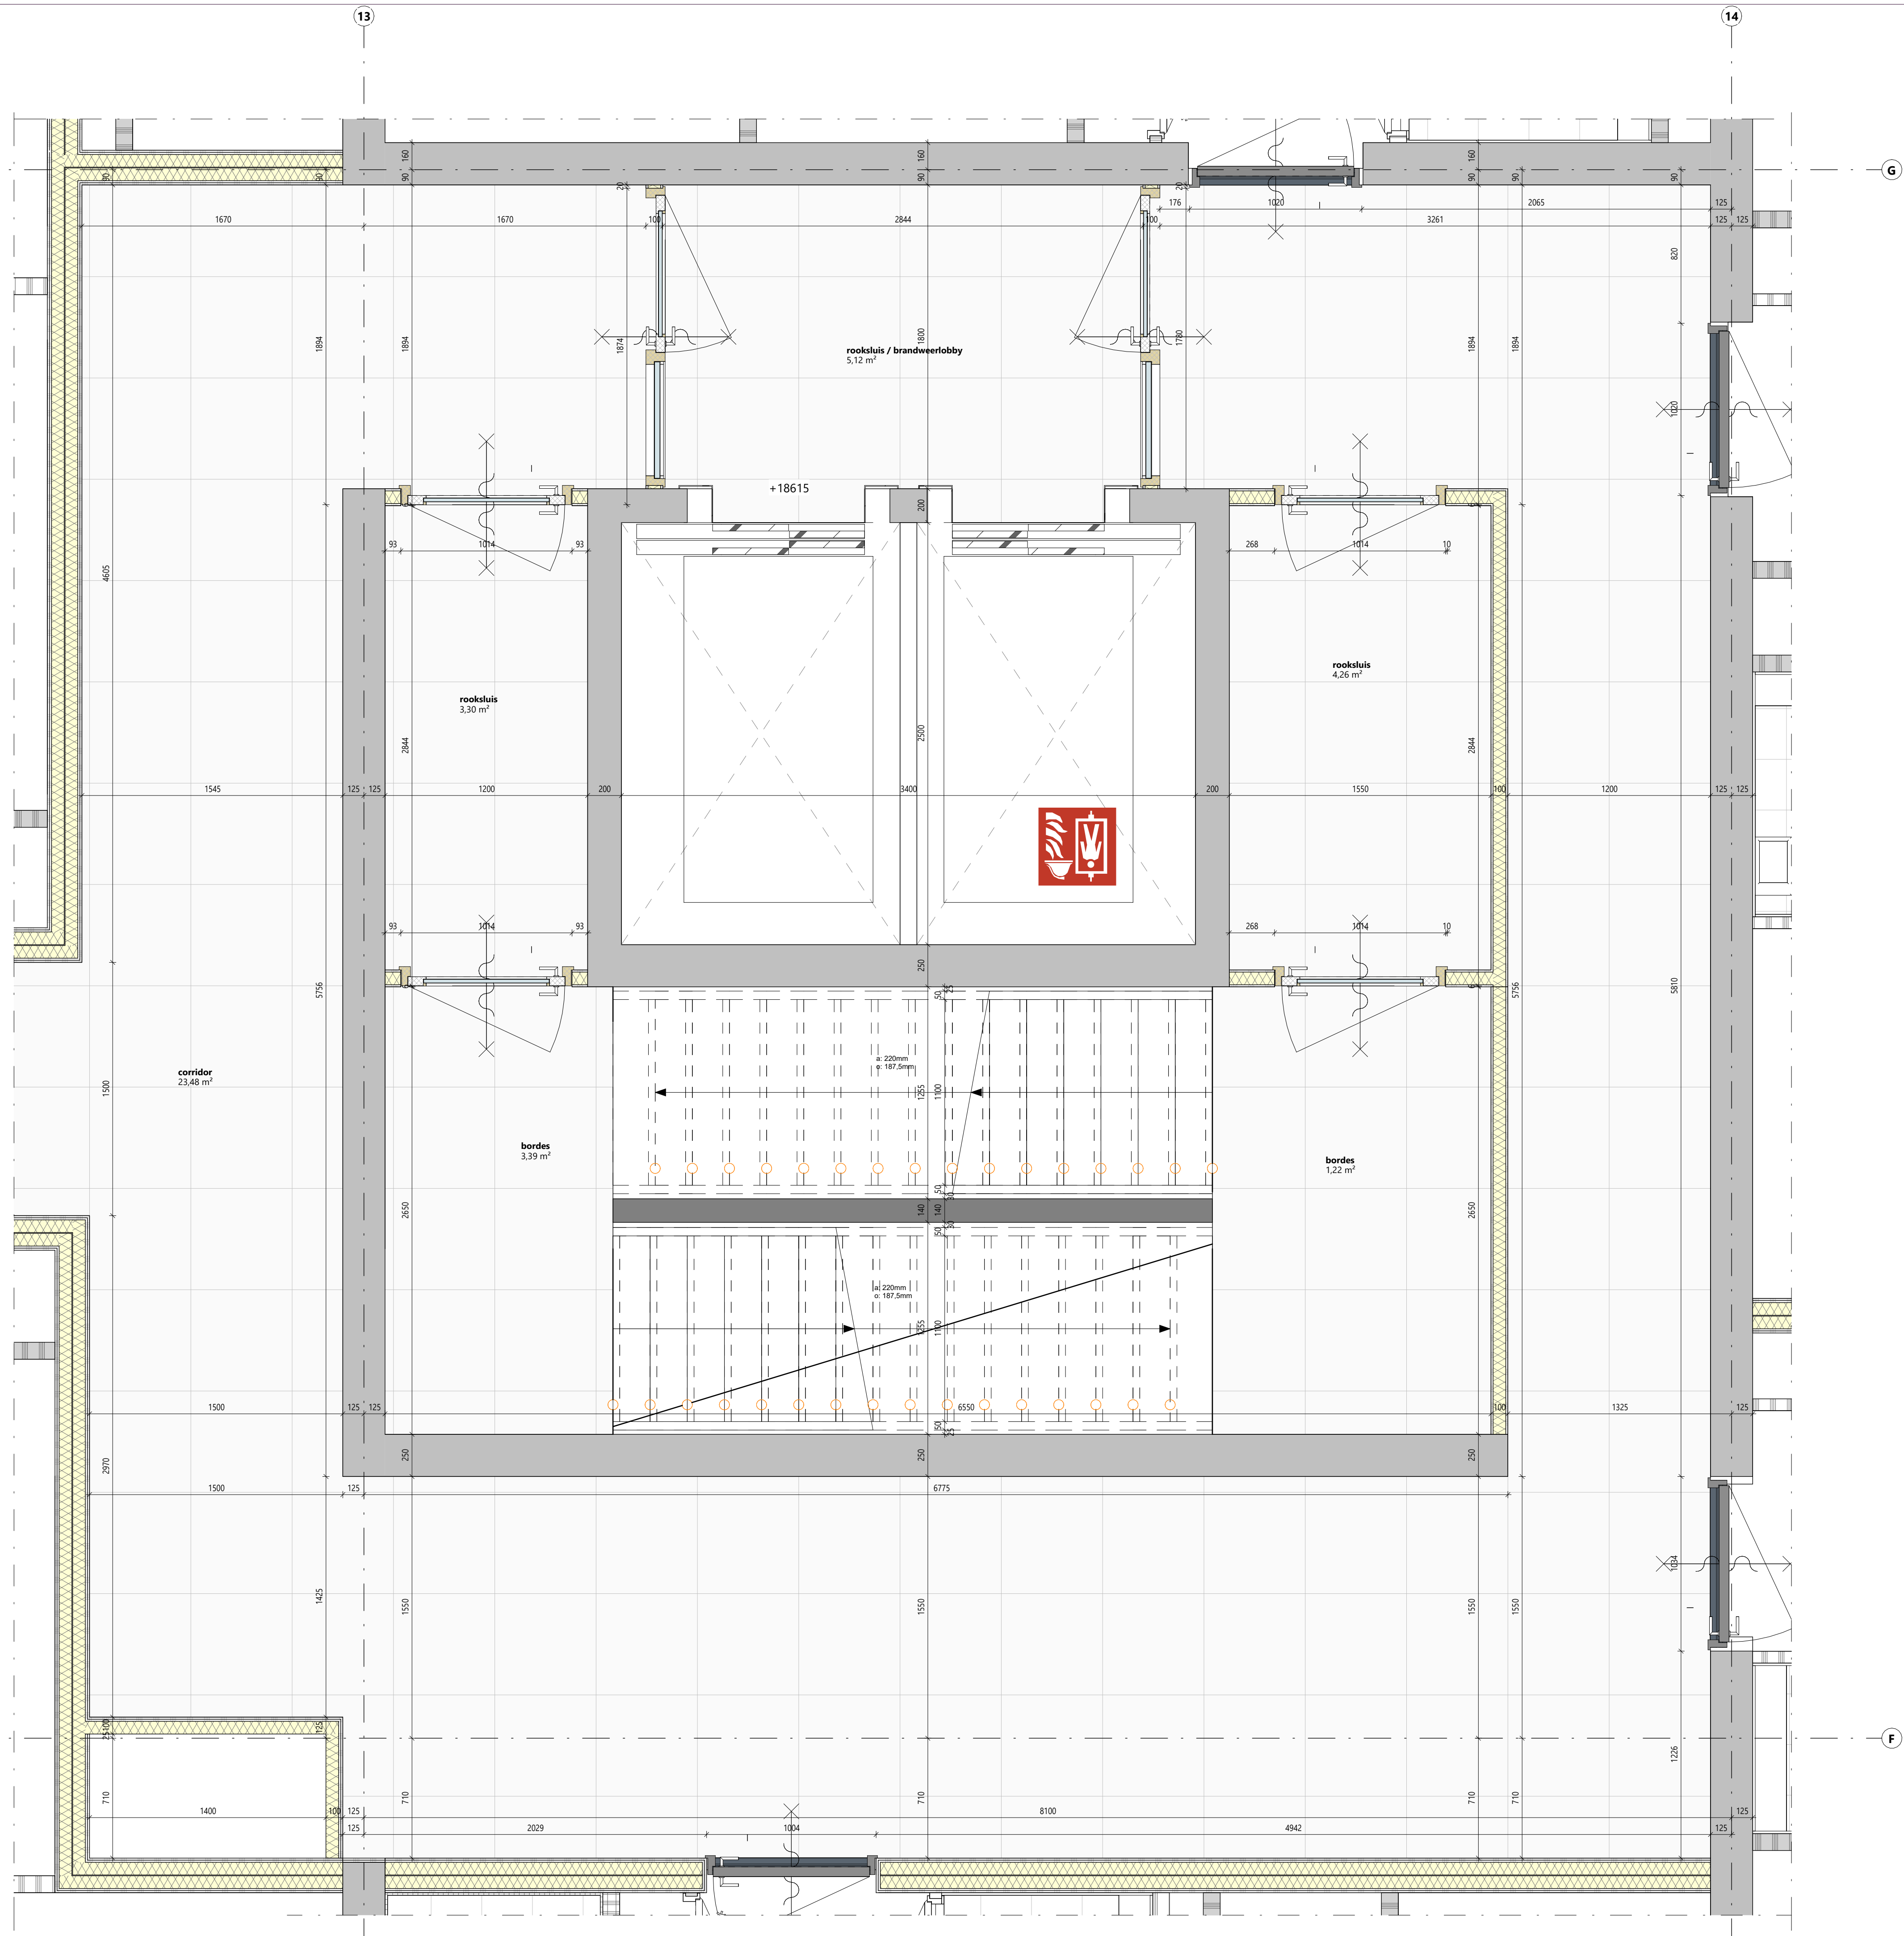

STUDIO
OXs

fragment kern zuid 06 verdieping

Gouda Harderwijkweg
Harderwijkweg 4, Gouda

Opdrachtgever: Create Realstate Raul Godron

Projectnr: 2459
Fase: TO
Auteur: JKolthof

Formaat: A1
Schaal: 1:20
1^e datum: 10-11-2025
Status: Definitief
Tekeningnr: TO-519


3bm
Ingenieurs van oplossingen

Tekening ongeschikt voor uitvoeringsfase
Geprint 8-11-2025 17:55:17

Piekstraat 27
3071 EL Rotterdam
+31 (0)6 41 23 22 49
info@studiooxs.com

3BM Bouwkunde
Wattstraat 17
3335 LV Zwijndrecht
Tel: 078 7400 258
jochem@3bm.co.nl
www.3bm.co.nl



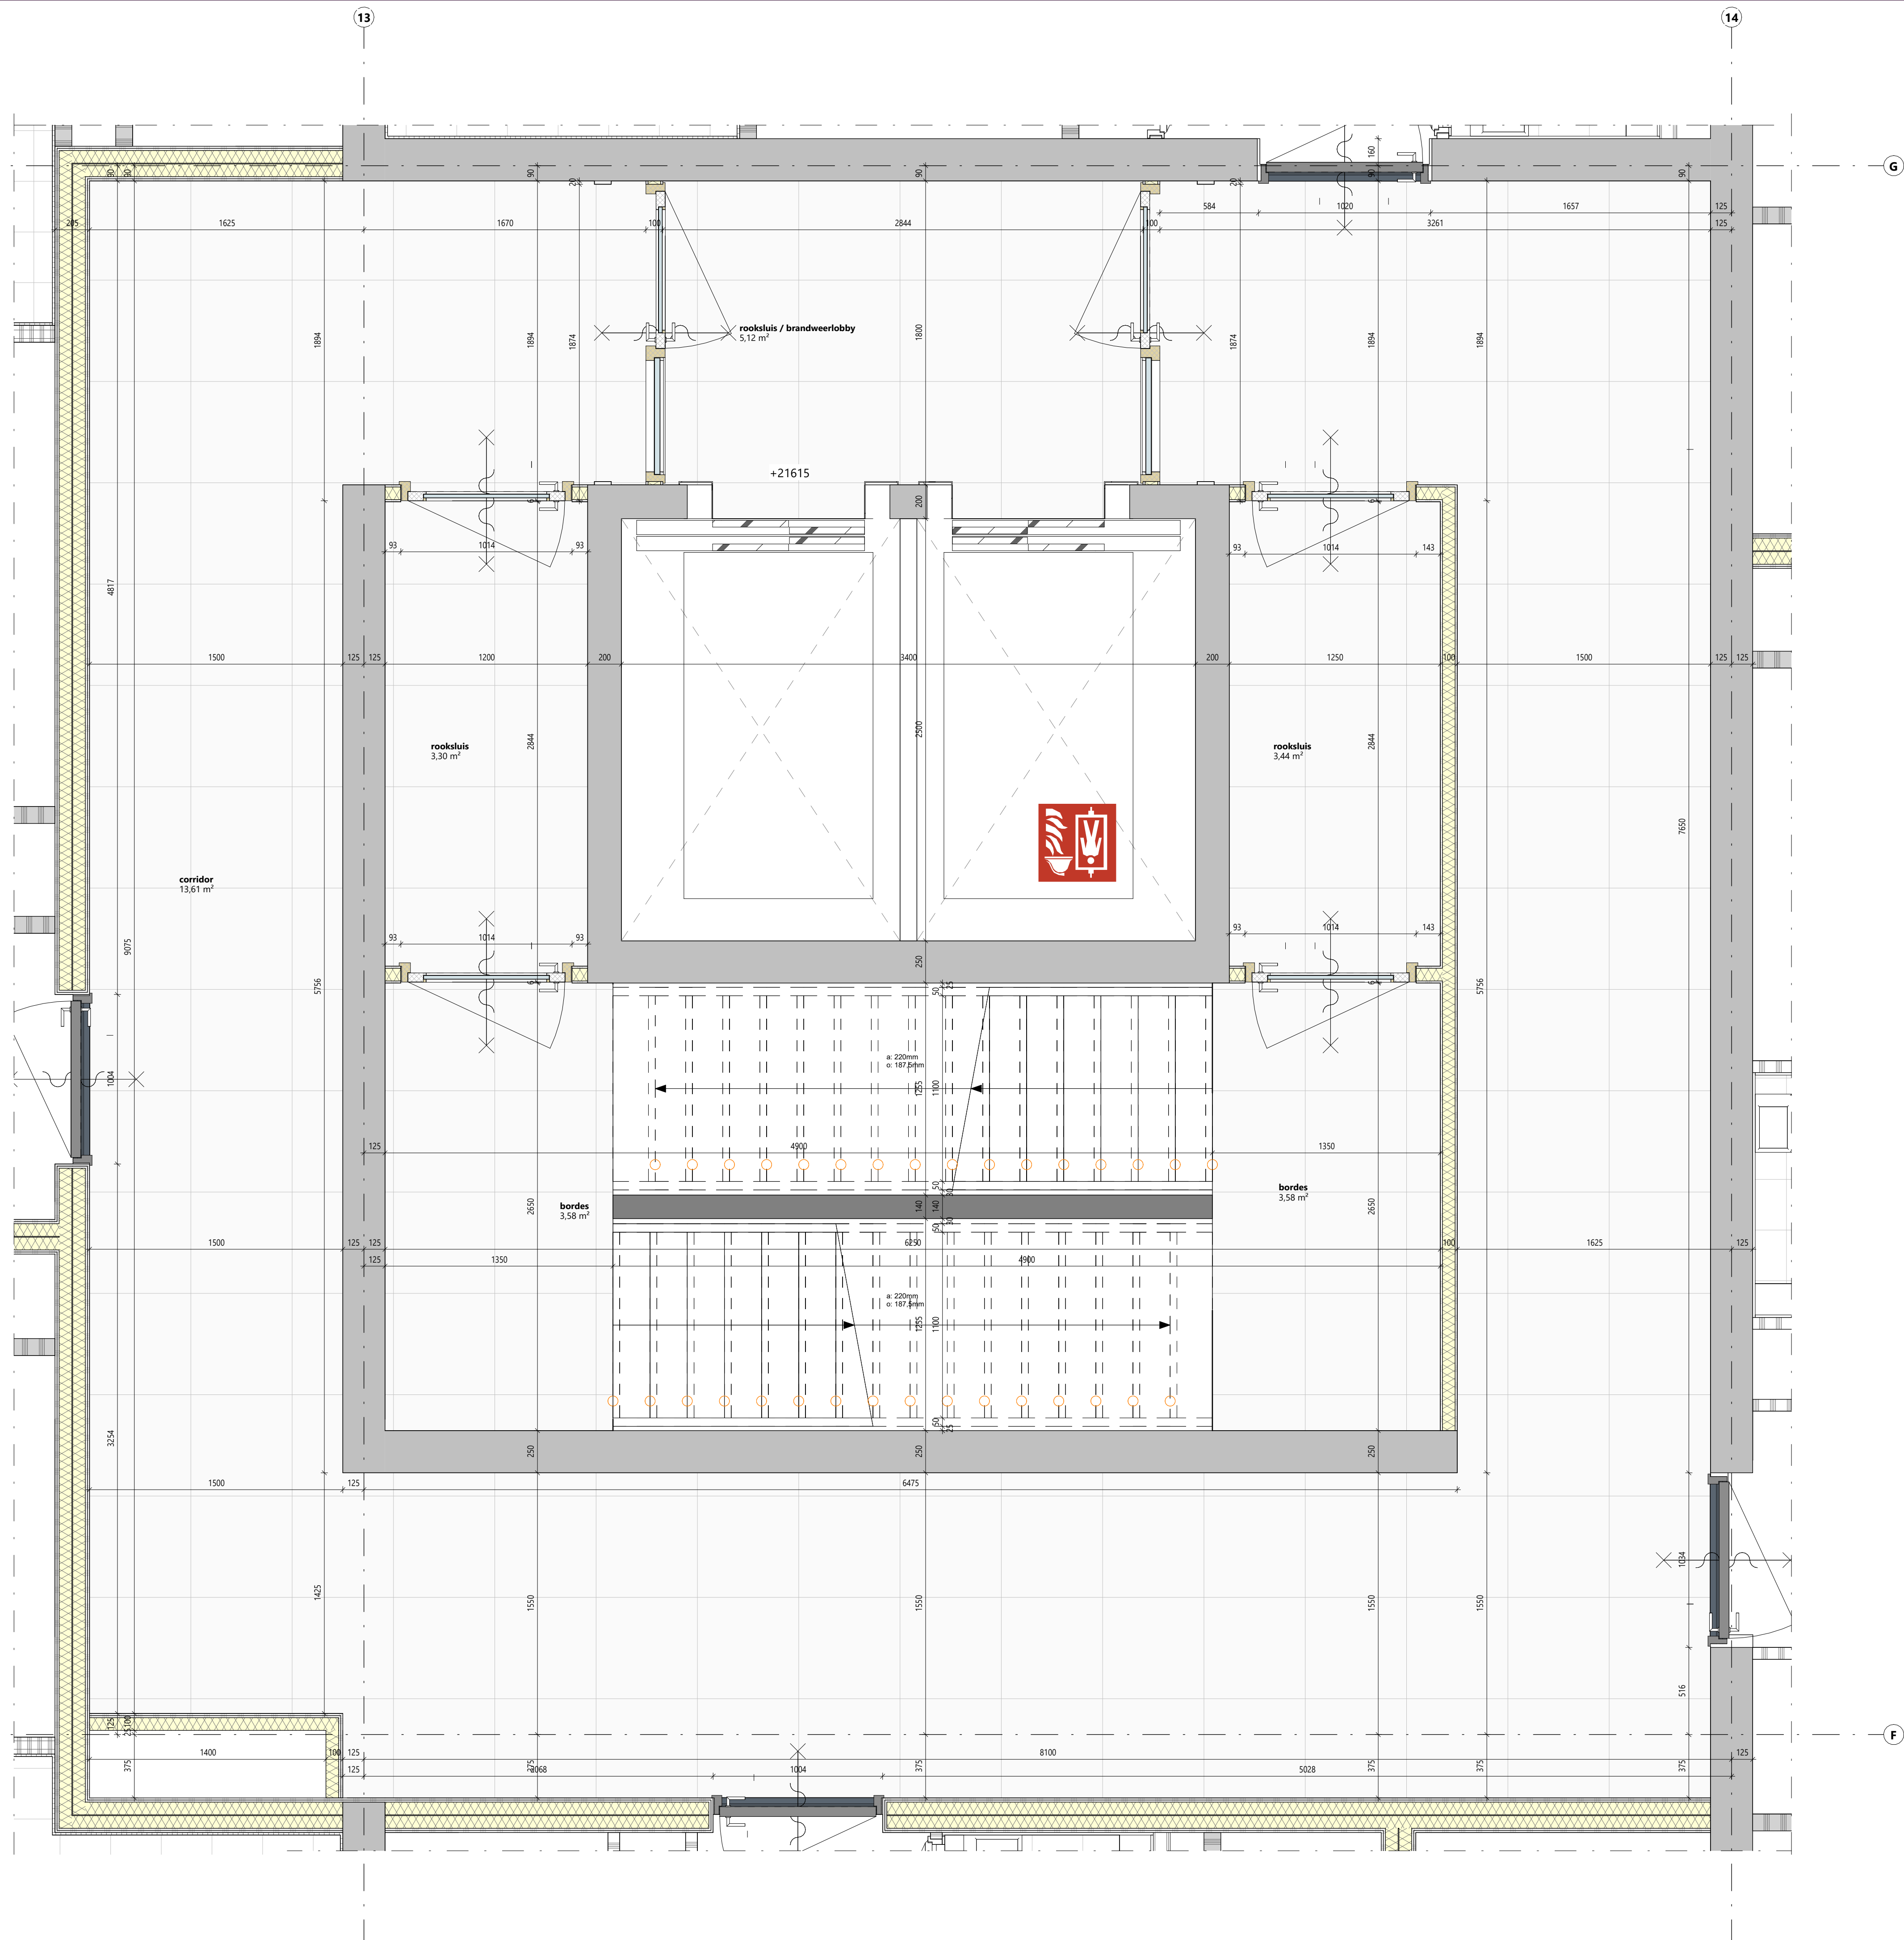

STUDIO
OXs

fragment kern zuid 07-10 verdieping

Gouda Harderwijkweg
Harderwijkweg 4, Gouda

Opdrachtgever: Create Real Estate Raul Godron

Projectnr: 2459
Fase: TO
Auteur: JKolthof

Formaat: A1
Schaal: 1:20
1^e datum: 10-11-2025
Status: Definitief
Tekeningnr: TO-520

3bm
Ingenieurs van oplossingen



Tekening ongeschikt voor uitvoeringsfase
Geprint 8-11-2025 17:55:18

Piekstraat 27
3071 EL Rotterdam
+31 (0)6 41 23 22 49
info@studiooxs.com

3BM Bouwkunde
Wattstraat 17
3335 LV Zwijndrecht

Tel: 078 7400 258
jochem@3bm.co.nl
www.3bm.co.nl



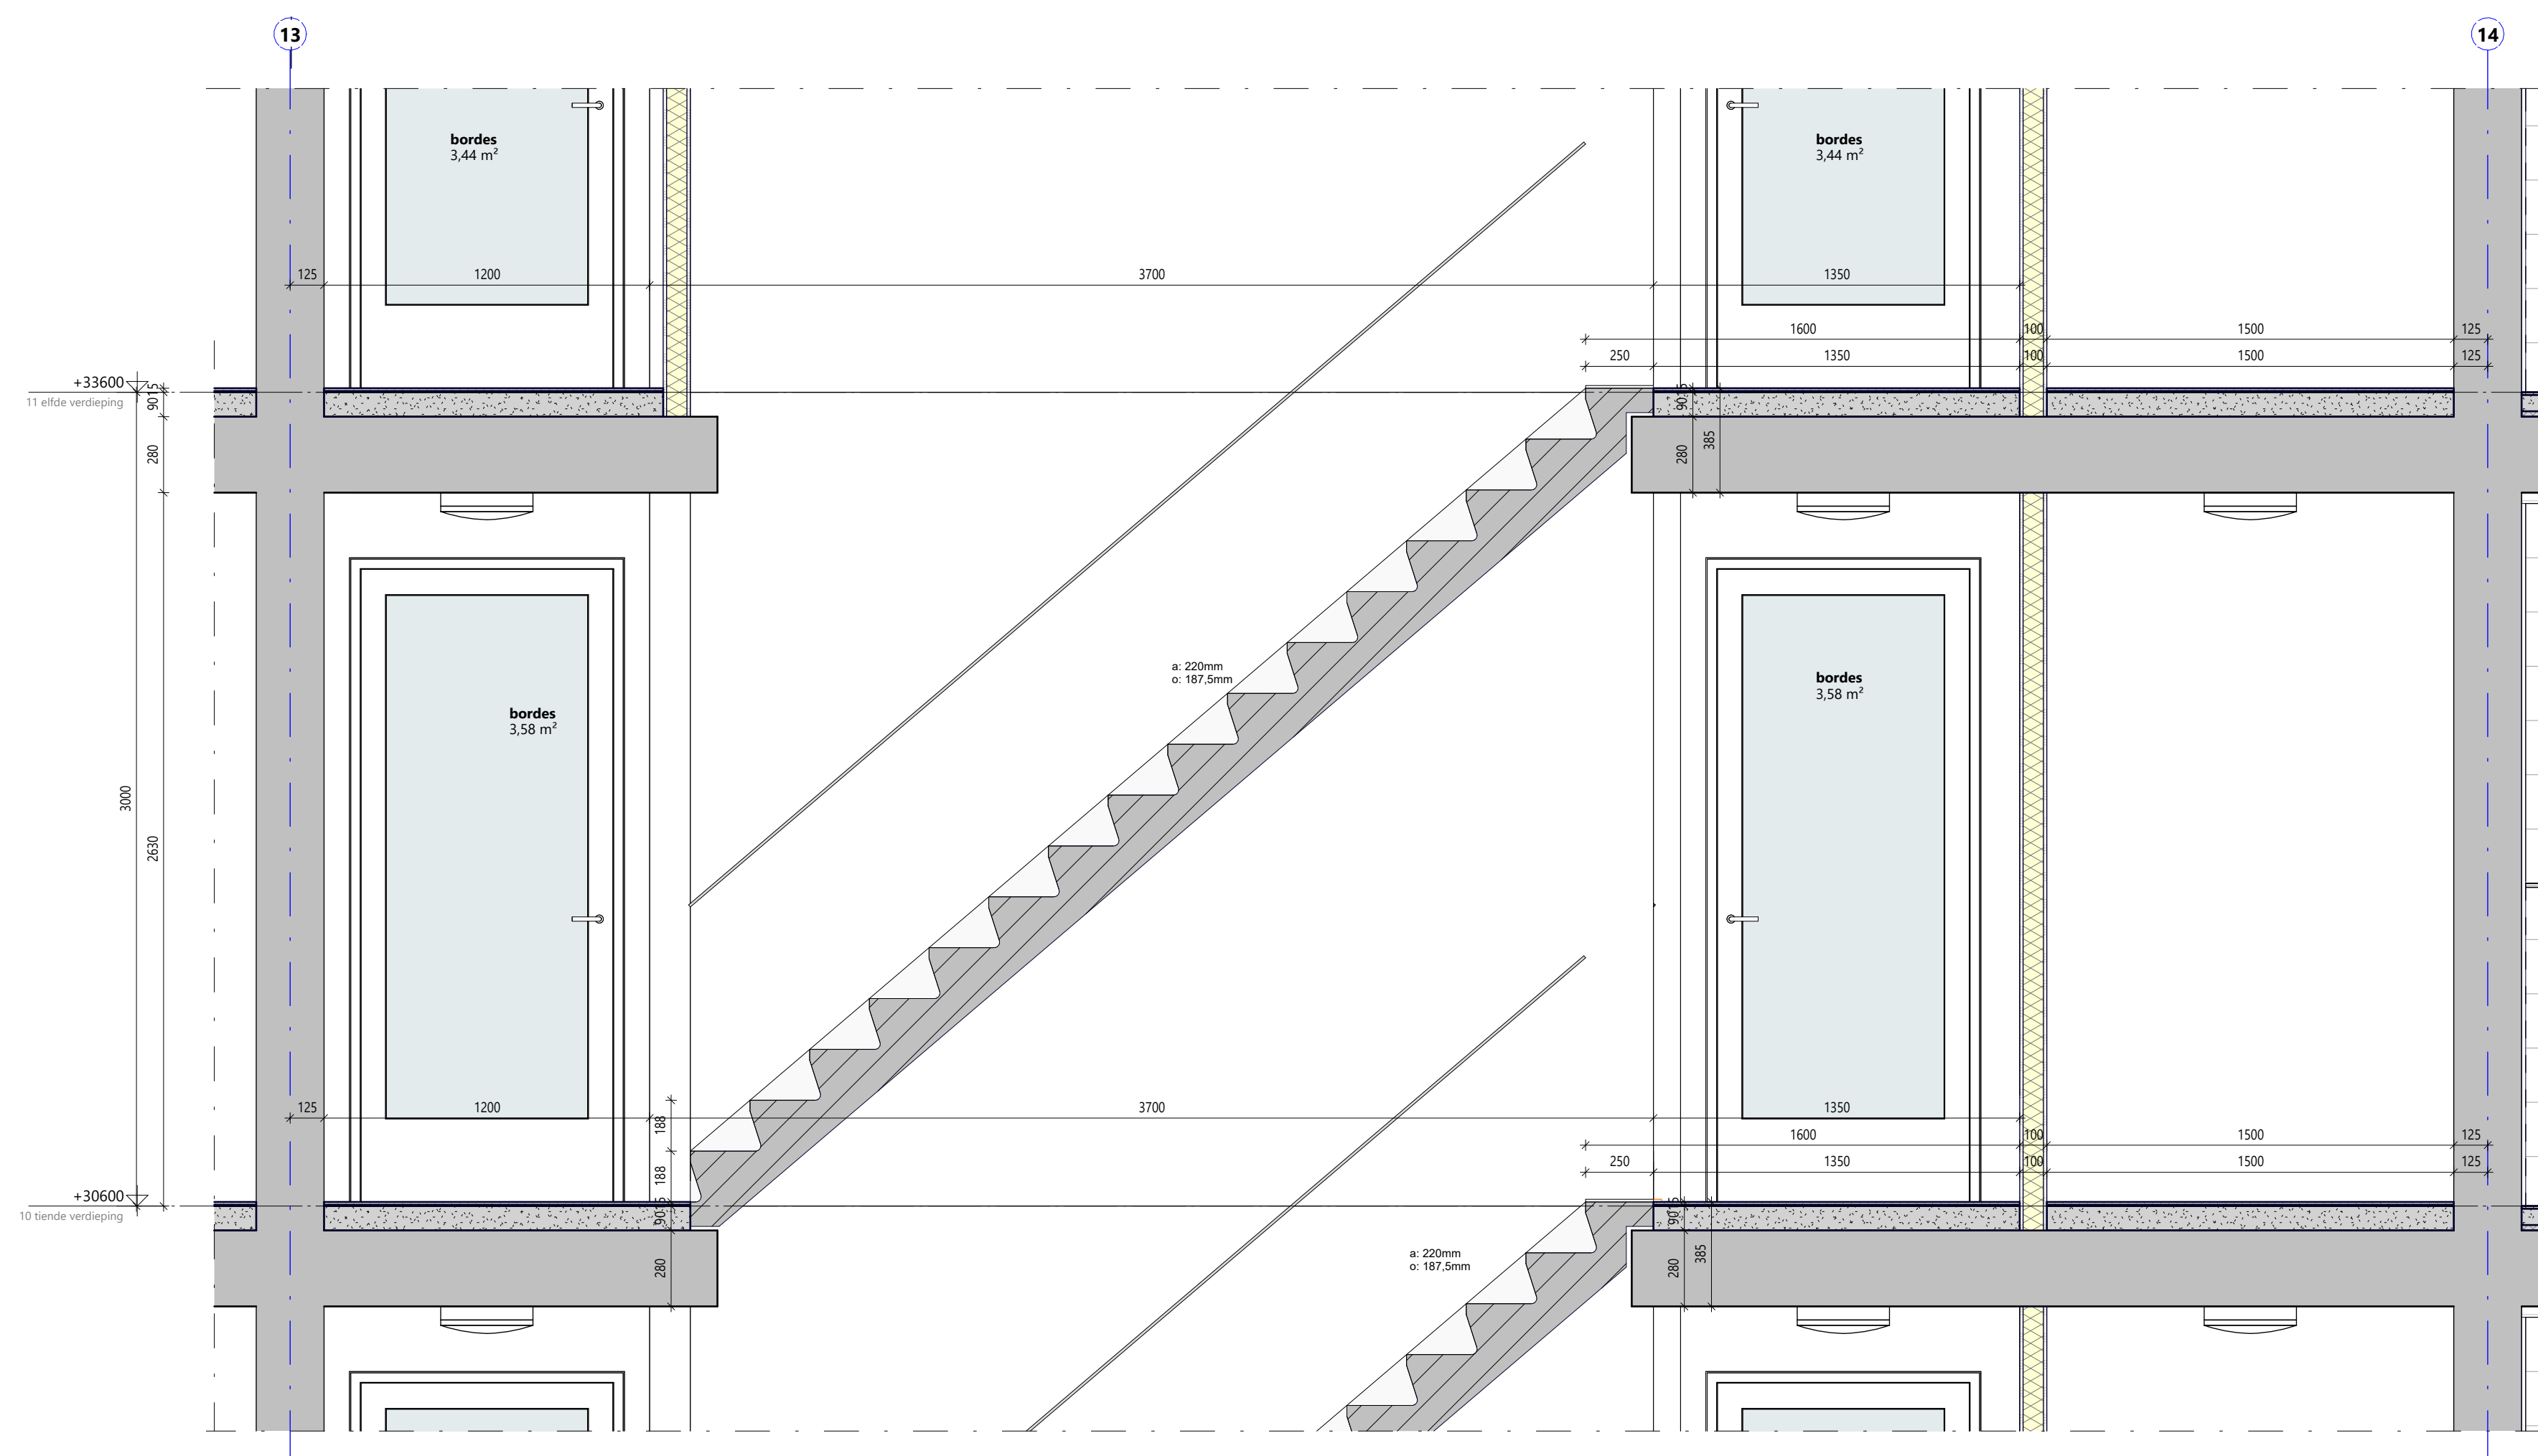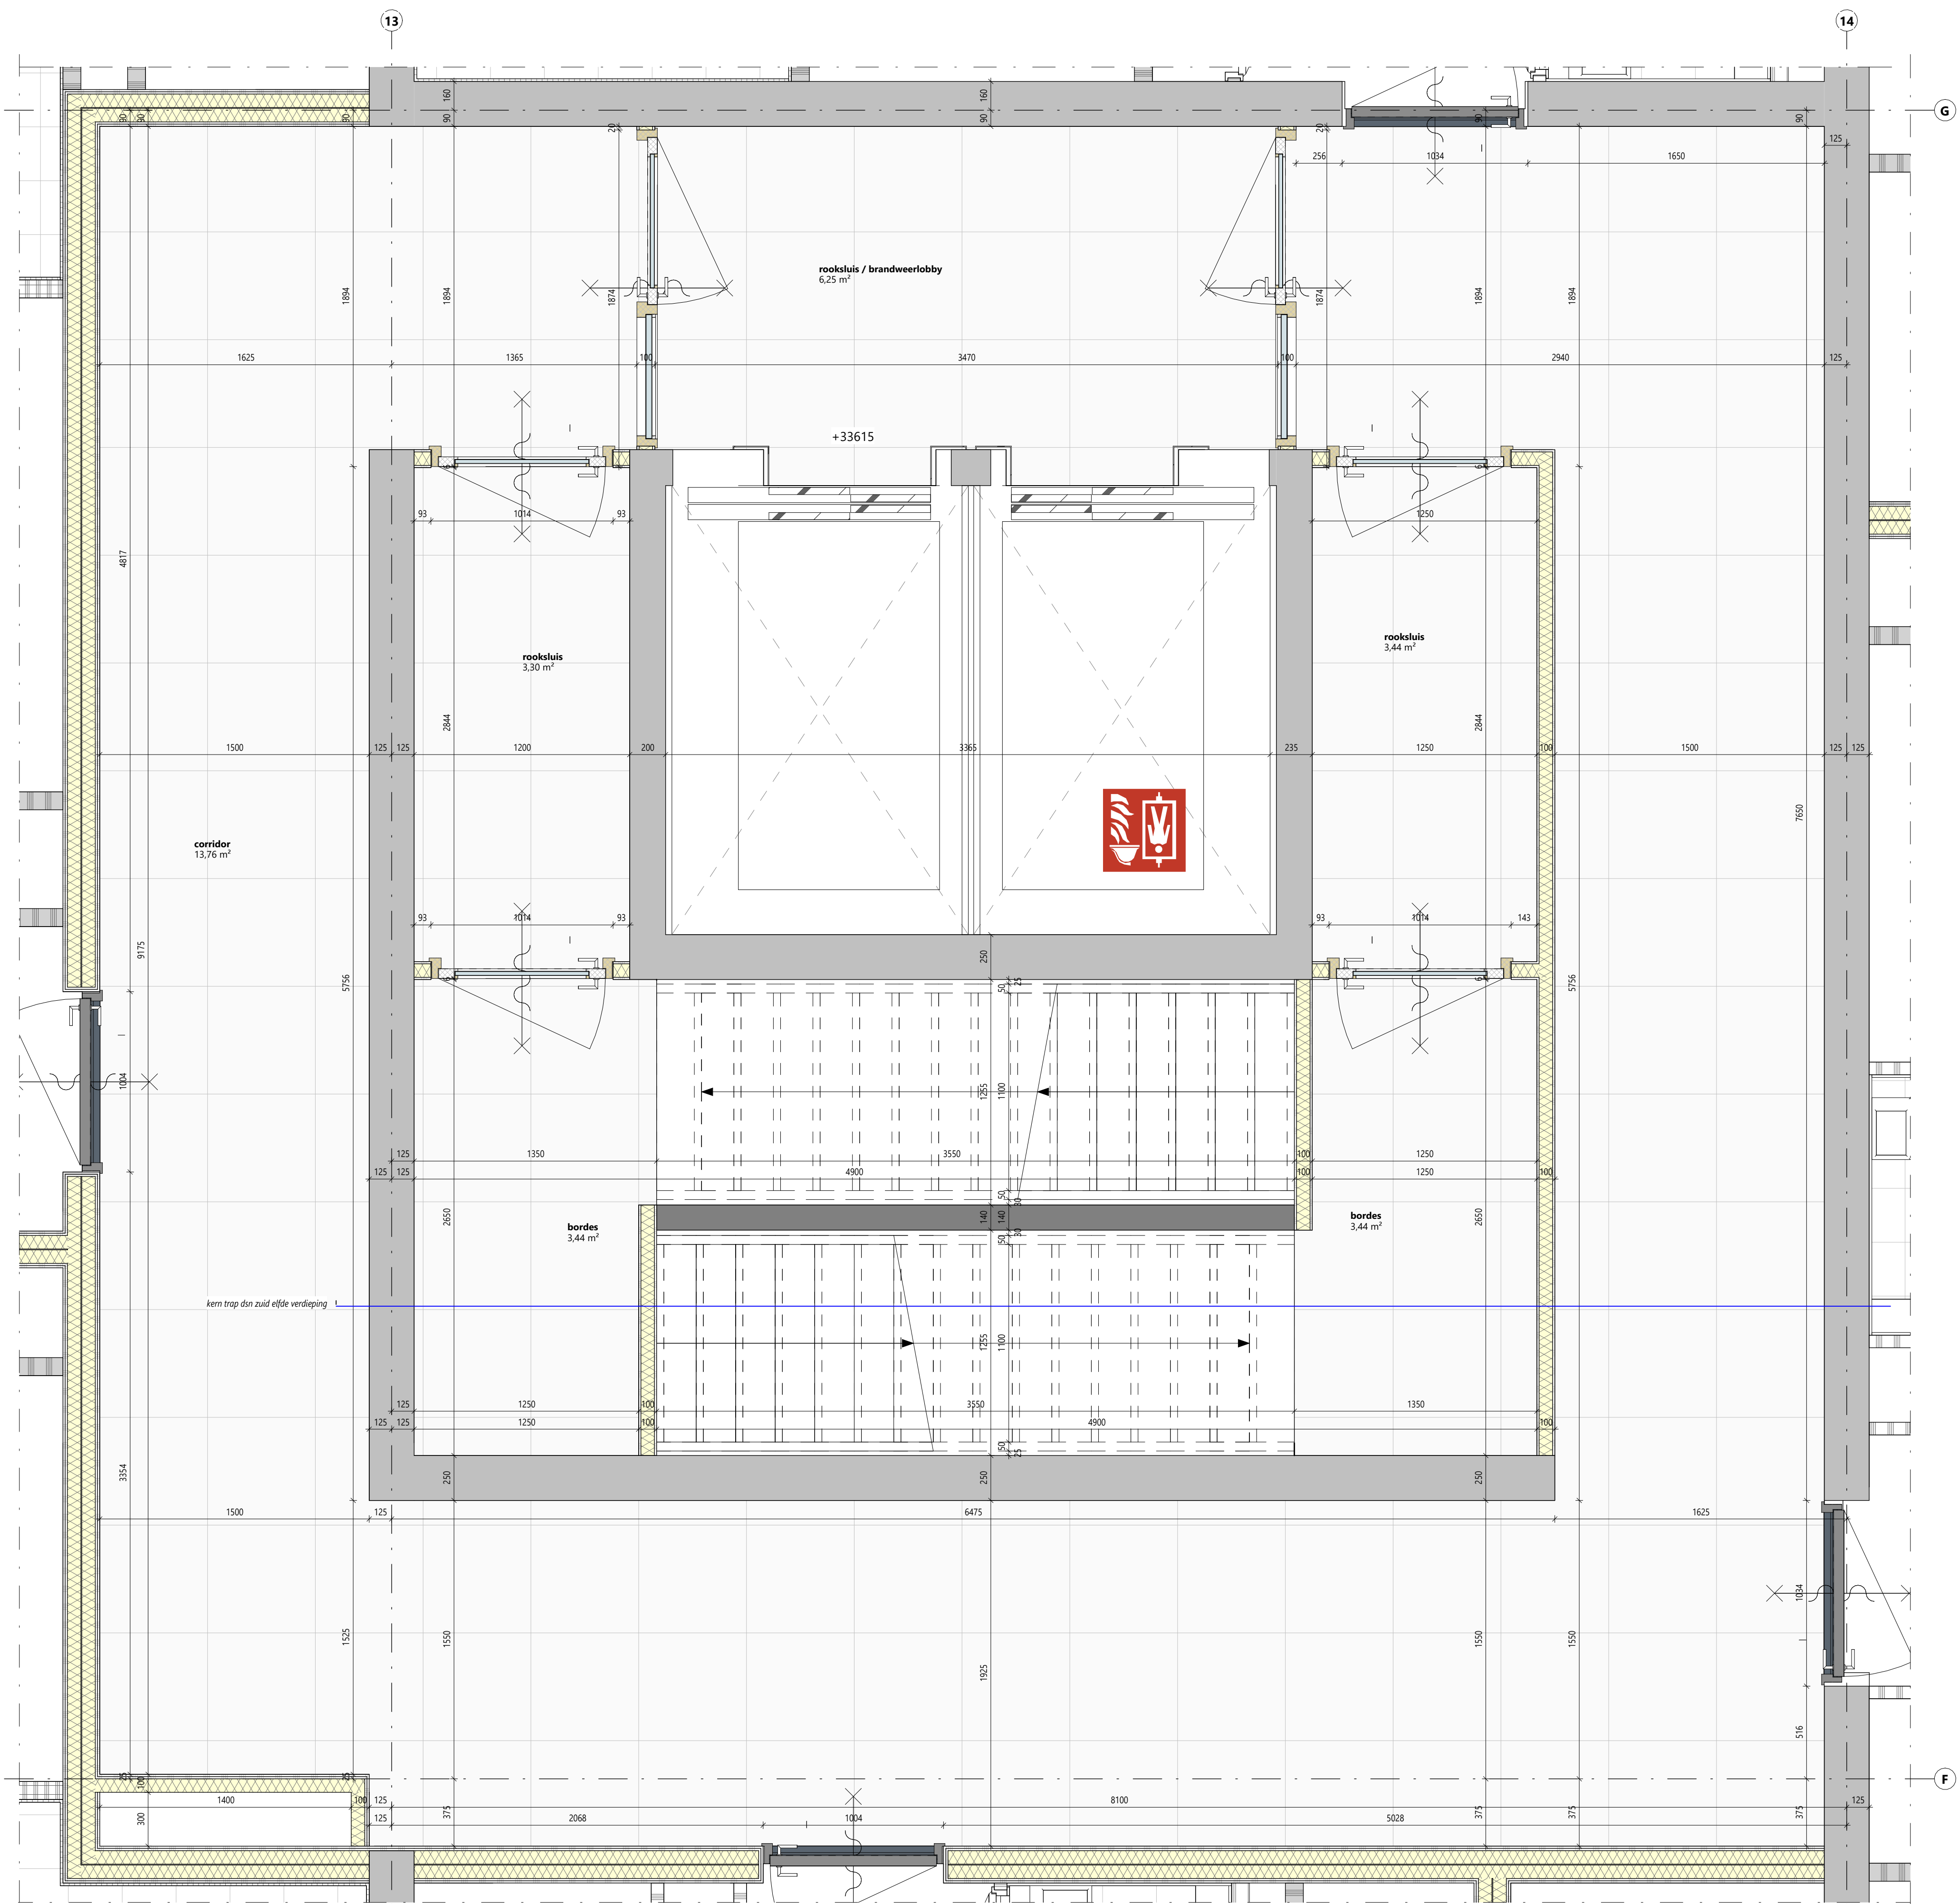

STUDIO
OXs

fragment kern zuid 11 verdieping

Gouda Harderwijkweg
Harderwijkweg 4, Gouda

Opdrachtgever: Create Realstate Raul Godron

Projectnr: 2459
Fase: TO
Auteur: J.Kalhof

Formaat: A0
Schale: 1:20
1^o datum: 10-11-2025
Status: Definitief
Tekeningnr: TO-S21


3bm
Ingenieurs van oplossingen

Tekening ongeschikt voor uitvoeringsfase
Geprint: 8-11-2025 17:55:20
Ploeg: Architect: Dries van der Vliet, Gouda: Kees van der Vliet, TO: Raul Godron

Piekstraat 27
3071 EL Rotterdam
+31 (0)6 41 23 22 49
info@studiooxs.com

3BM Bouwkunde
Watersstraat 17
3335 LV Zoetermeer
Tel: 078 7400 256
jochem@3bm.co.nl
www.3bm.co.nl



 

STUDIO
OXs

fragment plg hellingbaan

Gouda Harderwijkweg
Harderwijkweg 4, Gouda

Opdrachtgever: Create Real Estate Raul Godron

Project:
T10
Auteur:
J. Kothof

Schaal:
1:25
T10-11-2023
Status:
Definitief
Tekening:
T10-522

3bm
Ingenieurs van oplossingen

Tekening ongeschikt voor uitvoeringsfase
Geprijsd 8-11-2023 17:55:23

Piekstraat 27
3071 EL Rotterdam
+31 (0)6 41 23 22 49
info@studiooxs.com

3BM Bouwkunde
Wattstraat 17
3333 LV Zoelrecht
Tel: 078 1402 258
info@3bm.nl
www.3bm.nl

